AGUSTUS 2026

Project

Perencanaan Rumah Hunian
satu lantai TYPE 65,
Alamat : Bantaran Nila, Lampung.

ARCHILLES
STUDIO

DED


(Detail Engineering Design)

ARCHILLES
STUDIO

ARSITEKTUR

CODE :

ARS

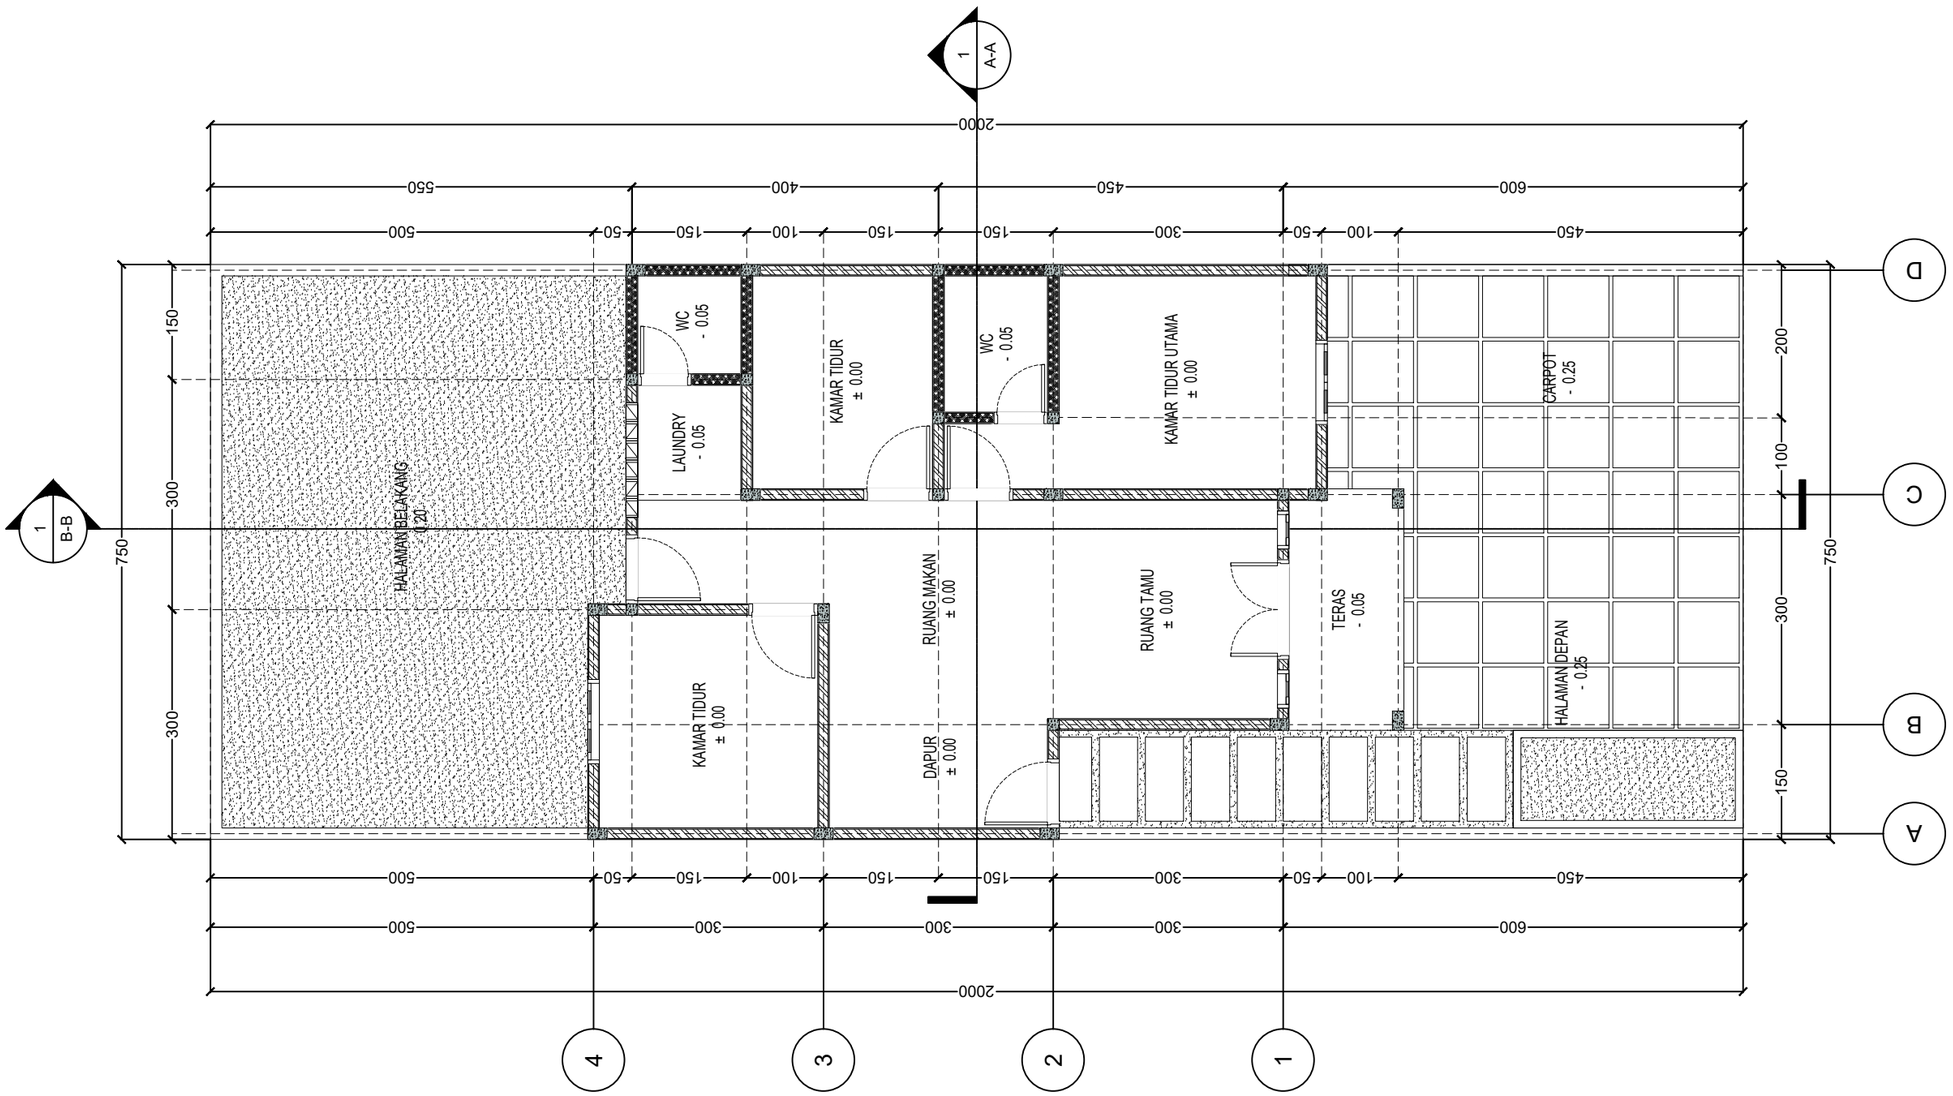

CODE
ARS

DENAH

SKALA 1 : 80

ARCHILLES STUDIO

KETERANGAN :

PROJECT :

PERENCANAAN RUMAH HUNIAN
TYPE 65

LOKASI :

BANTARAN NILA, LAMPUNG

OWNER :


.....

PERENCANA :

ARCHILLES TEAM

JUDUL GAMBAR	SKALA

TOTAL HALAMAN	CODE	NO HALAMAN

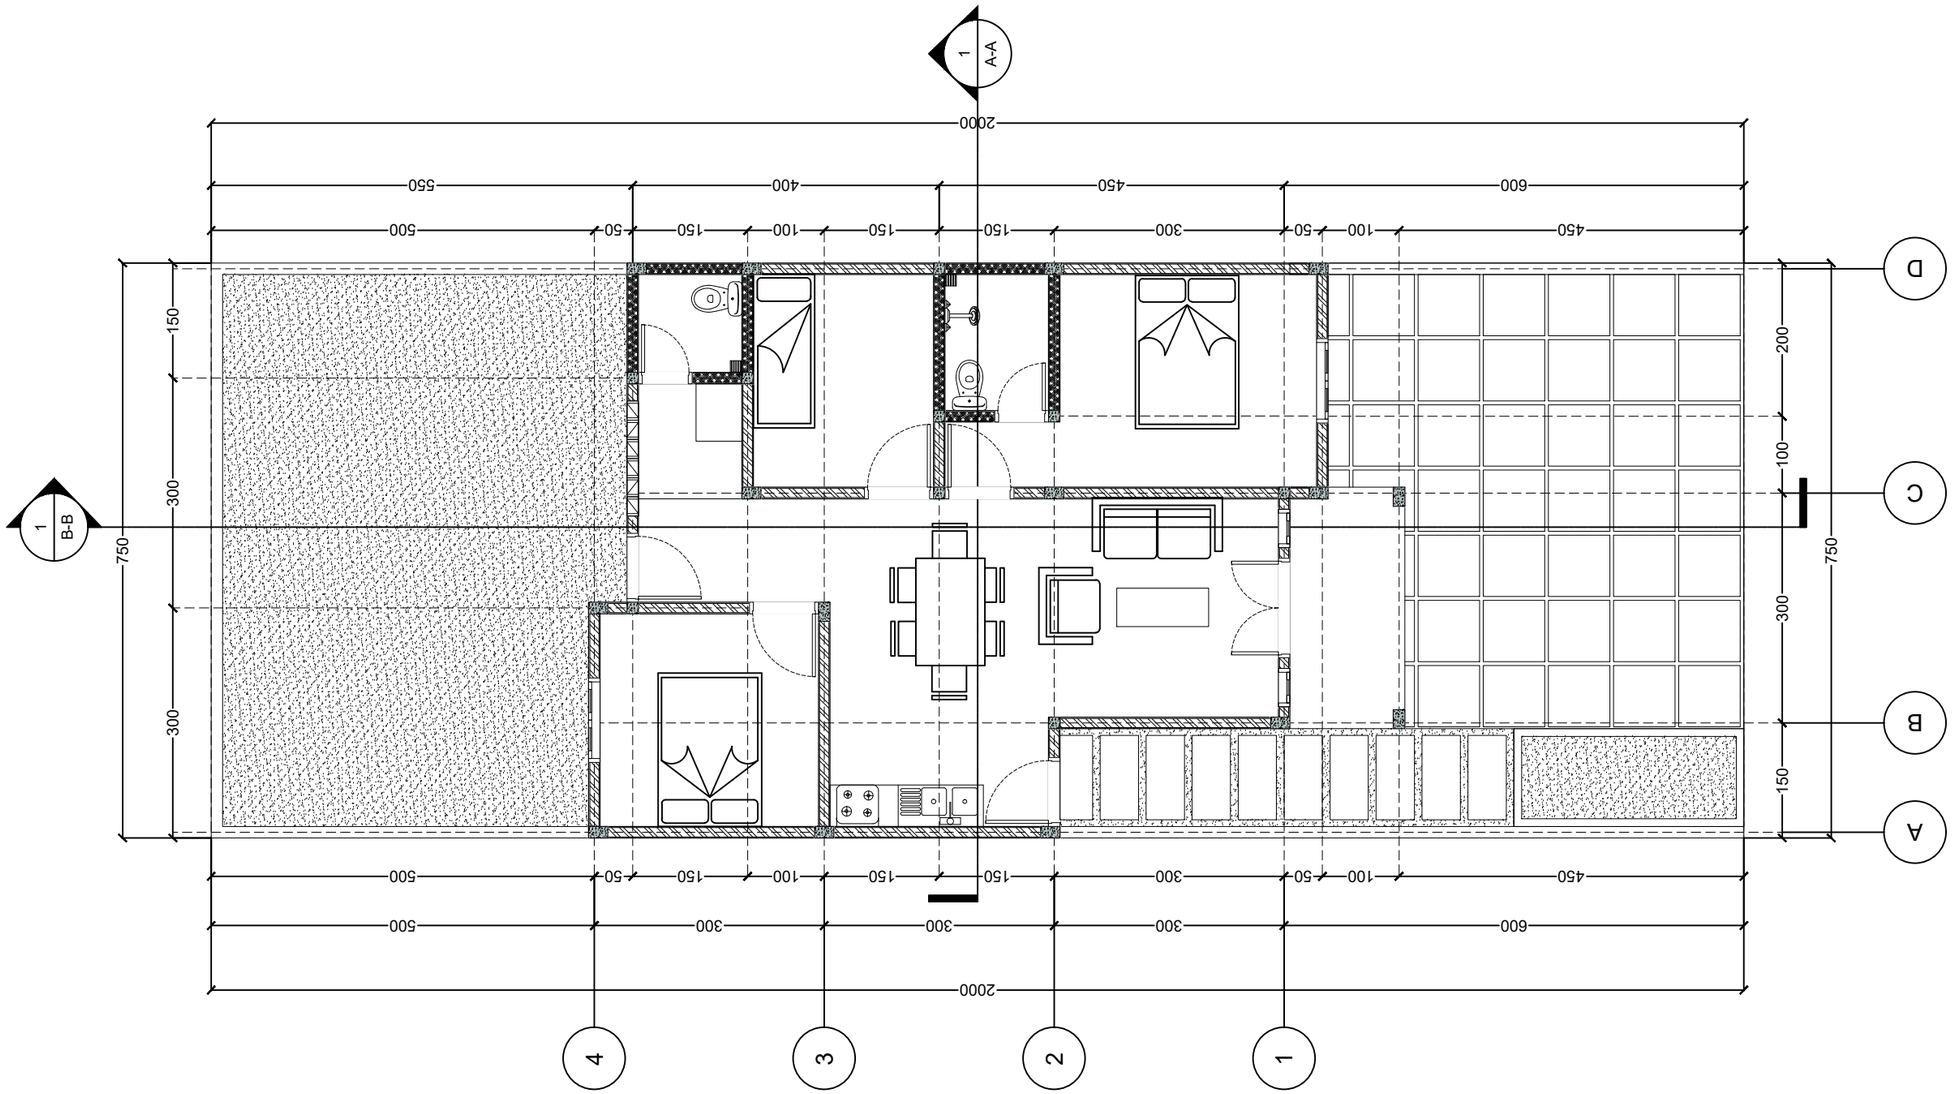

CODE
ARS

DENAH LAY OUT

SKALA 1 : 80

ARCHILLES STUDIO

KETERANGAN :

PROJECT :

PERENCANAAN RUMAH HUNIAN
TYPE 65

LOKASI :

BANTARAN NILA, LAMPUNG

OWNER :

.....

PERENCANA :

ARCHILLES TEAM

JUDUL GAMBAR	SKALA


TOTAL HALAMAN	CODE	NO HALAMAN



CODE
ARS

TAMPAK DEPAN

SKALA 1 : 80

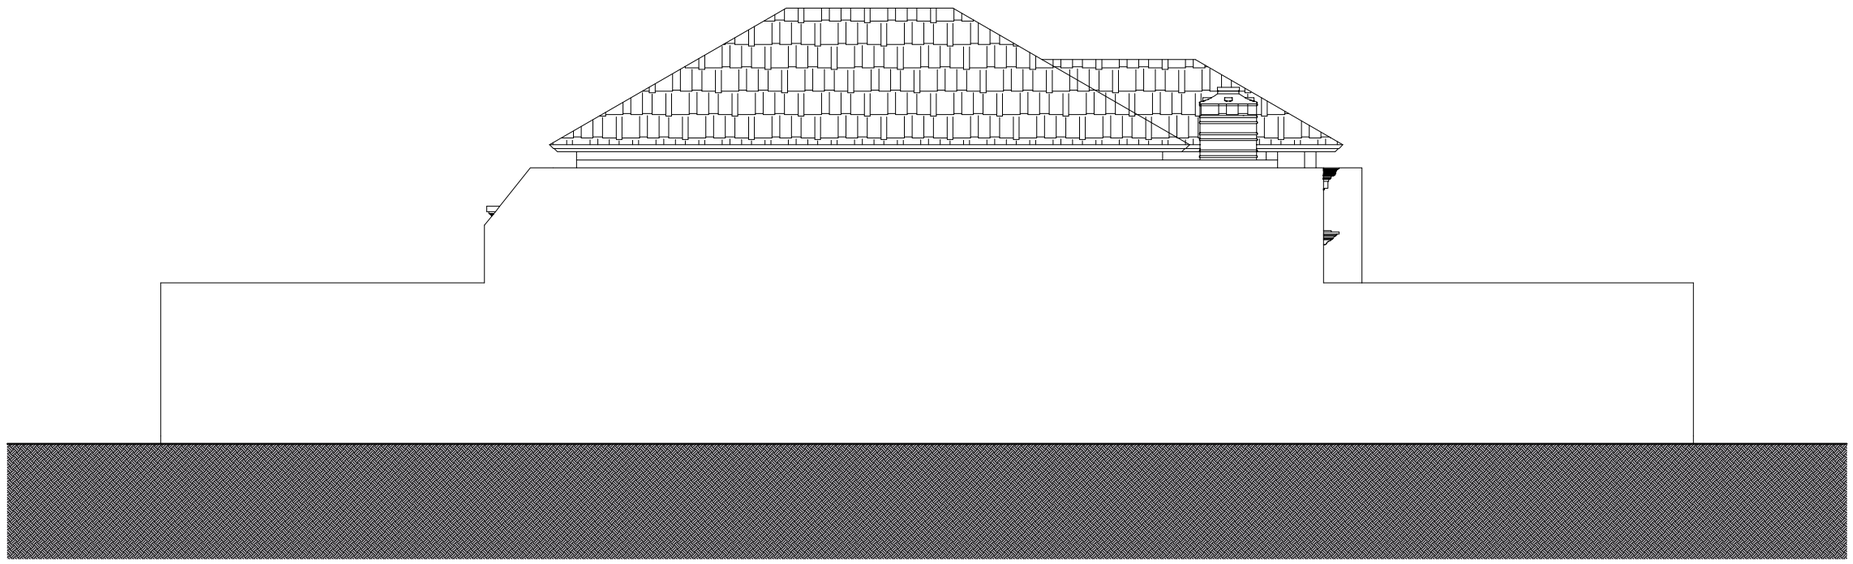

CODE
ARS

TAMPAK SAMPING KANAN

SKALA 1 : 80

ARCHILLES STUDIO

KETERANGAN :

PROJECT :

PERENCANAAN RUMAH HUNIAN
TYPE 65

LOKASI :

BANTARAN NILA, LAMPUNG

OWNER :

.....

PERENCANA :

ARCHILLES TEAM

JUDUL GAMBAR	SKALA


TOTAL HALAMAN	CODE	NO HALAMAN



CODE
ARS

TAMPAK BELAKANG

SKALA 1 : 80

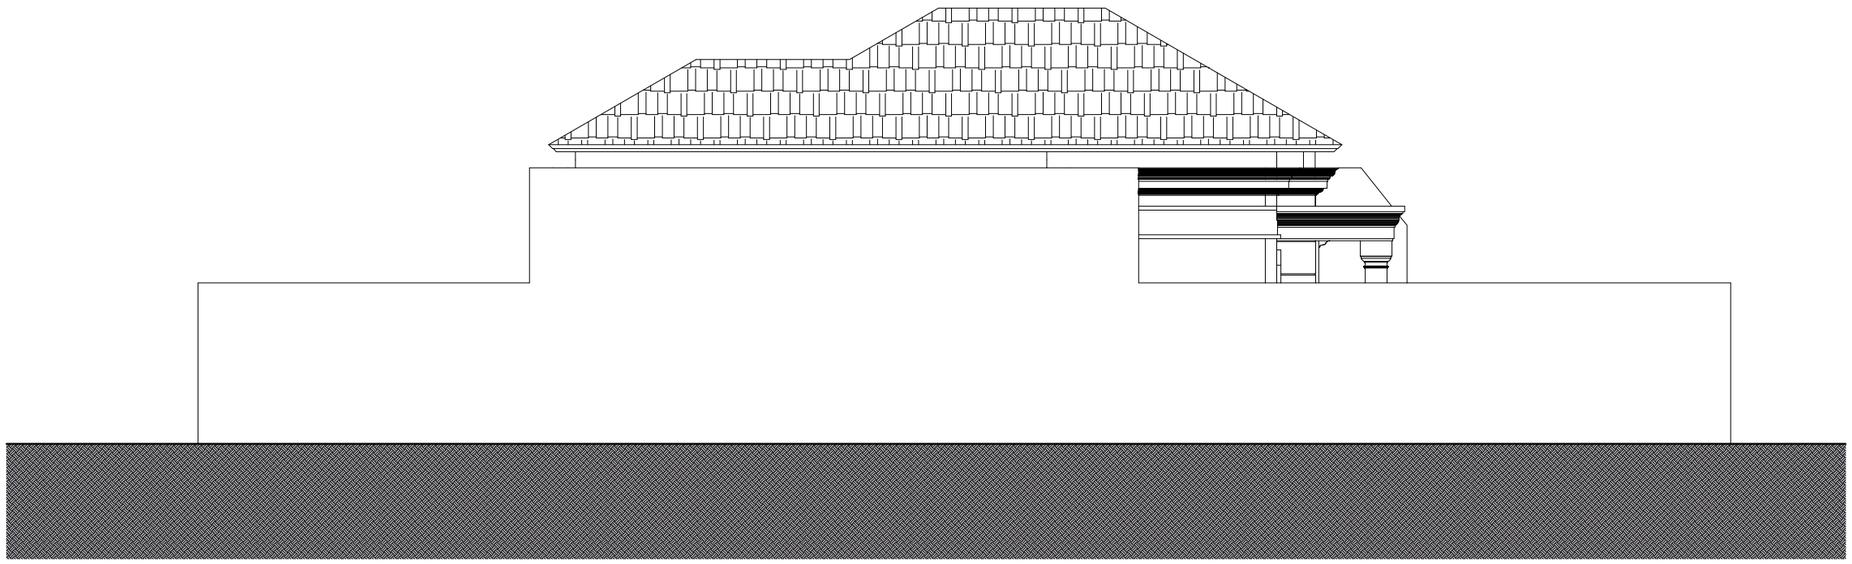

CODE
ARS

TAMPAK SAMPING KIRI

SKALA 1 : 80

ARCHILLES STUDIO

KETERANGAN :

PROJECT :

PERENCANAAN RUMAH HUNIAN
TYPE 65

LOKASI :

BANTARAN NILA, LAMPUNG

OWNER :


.....

PERENCANA :

ARCHILLES TEAM

JUDUL GAMBAR	SKALA

TOTAL HALAMAN	CODE	NO HALAMAN

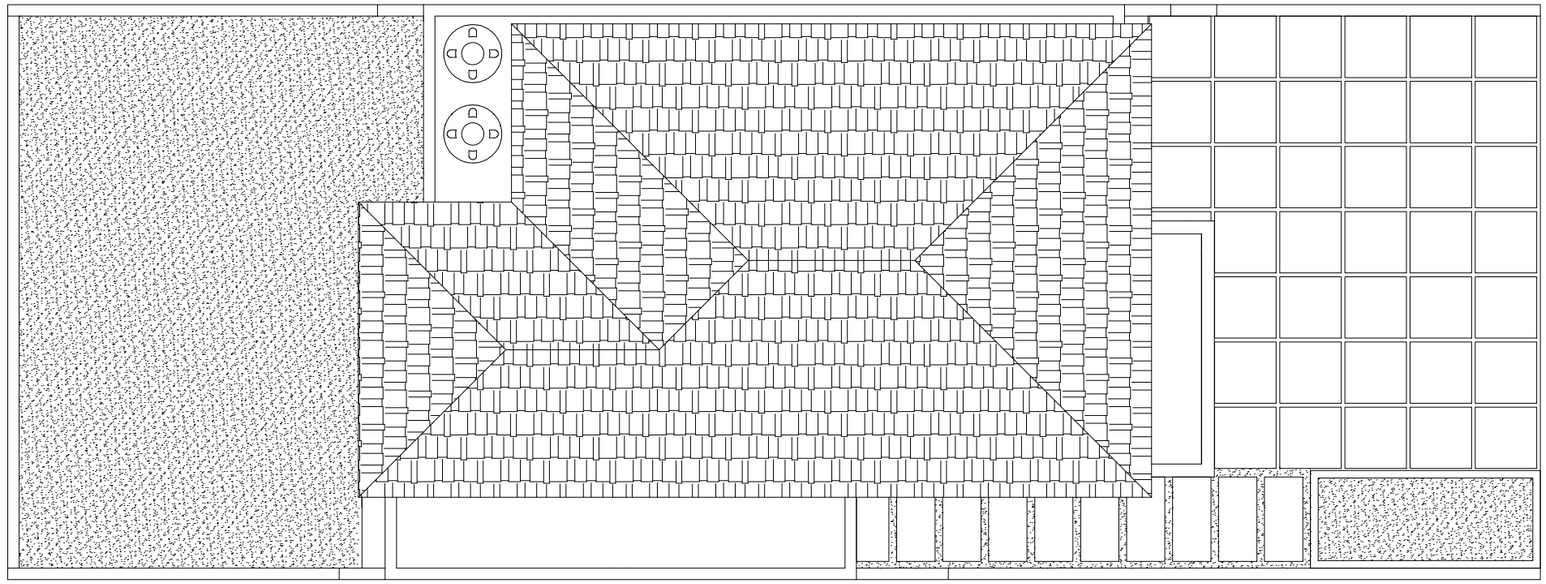

CODE
ARS

TAMPAK ATAS

SKALA 1 : 80

ARCHILLES STUDIO

KETERANGAN :

PROJECT :

PERENCANAAN RUMAH HUNIAN
TYPE 65

LOKASI :

BANTARAN NILA, LAMPUNG

OWNER :


.....

PERENCANA :

ARCHILLES TEAM

JUDUL GAMBAR	SKALA

TOTAL HALAMAN	CODE	NO HALAMAN

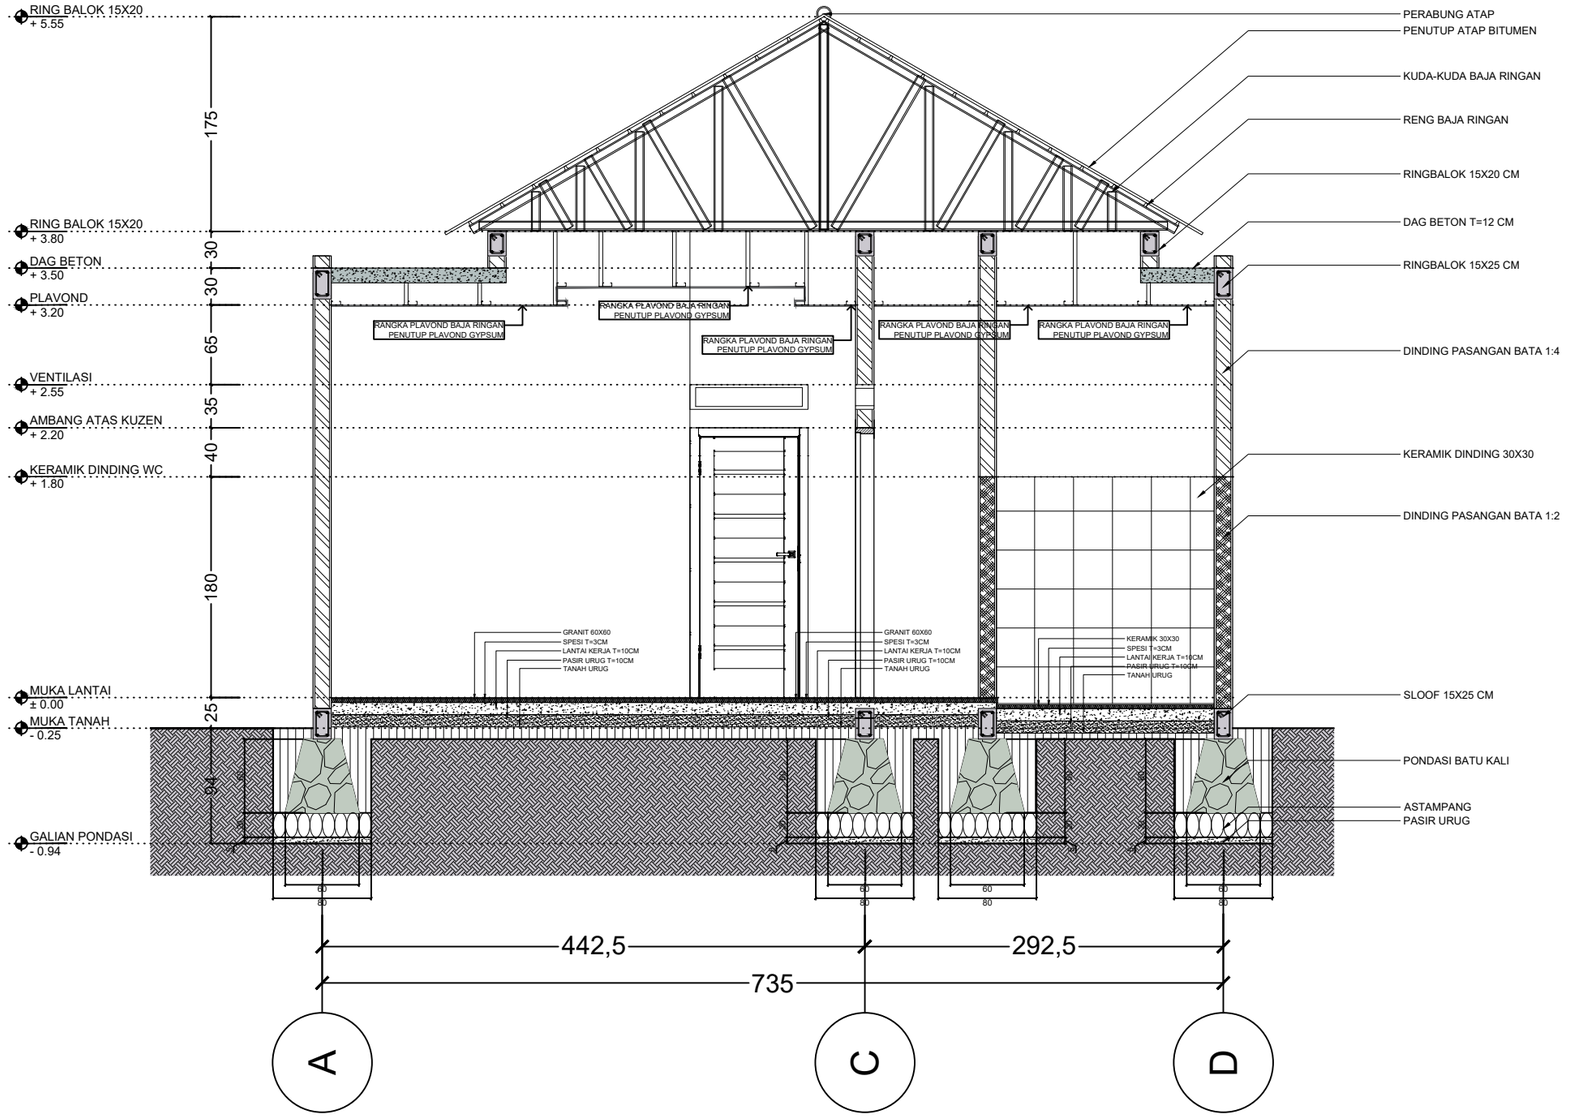

CODE
ARS

POTONGAN A-A

SKALA 1 : 50

ARCHILLES STUDIO

KETERANGAN :

PROJECT :

PERENCANAAN RUMAH HUNIAN
TYPE 65

LOKASI :

BANTARAN NILA, LAMPUNG

OWNER :


.....

PERENCANA :

ARCHILLES TEAM

JUDUL GAMBAR	SKALA

TOTAL HALAMAN	CODE	NO HALAMAN

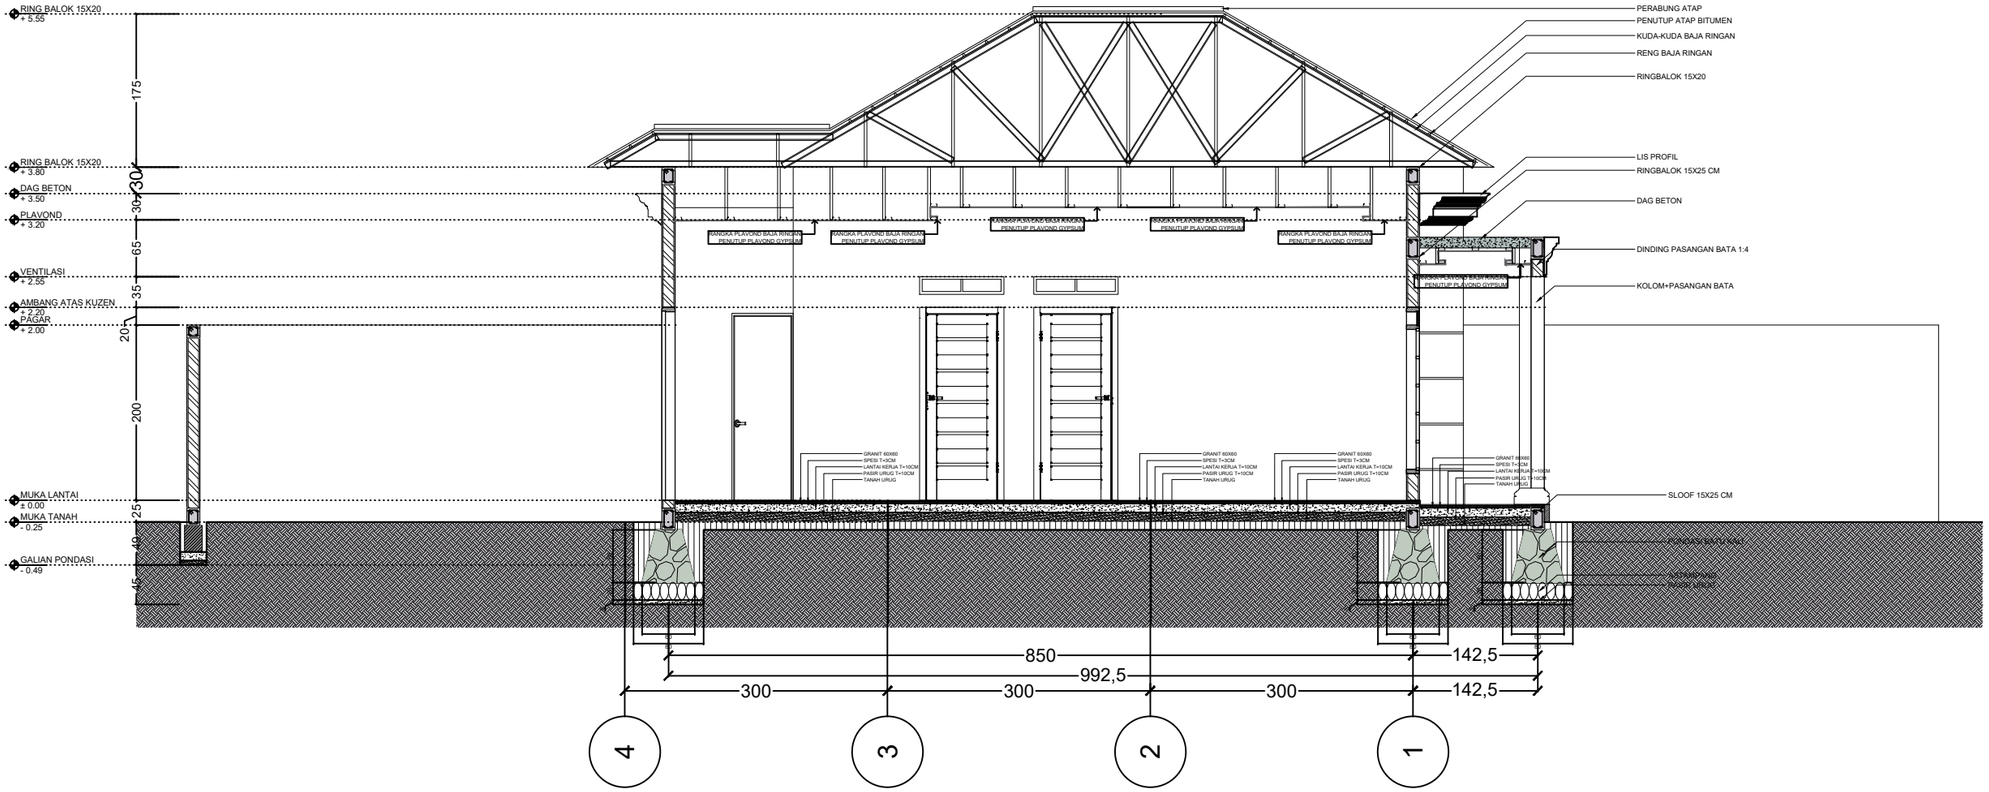

CODE
ARS

POTONGAN B-B

SKALA 1 : 70

ARCHILLES STUDIO

KETERANGAN :

PROJECT :

PERENCANAAN RUMAH HUNIAN
TYPE 65

LOKASI :

BANTARAN NILA, LAMPUNG

OWNER :


.....

PERENCANA :

ARCHILLES TEAM

JUDUL GAMBAR	SKALA

TOTAL HALAMAN	CODE	NO HALAMAN

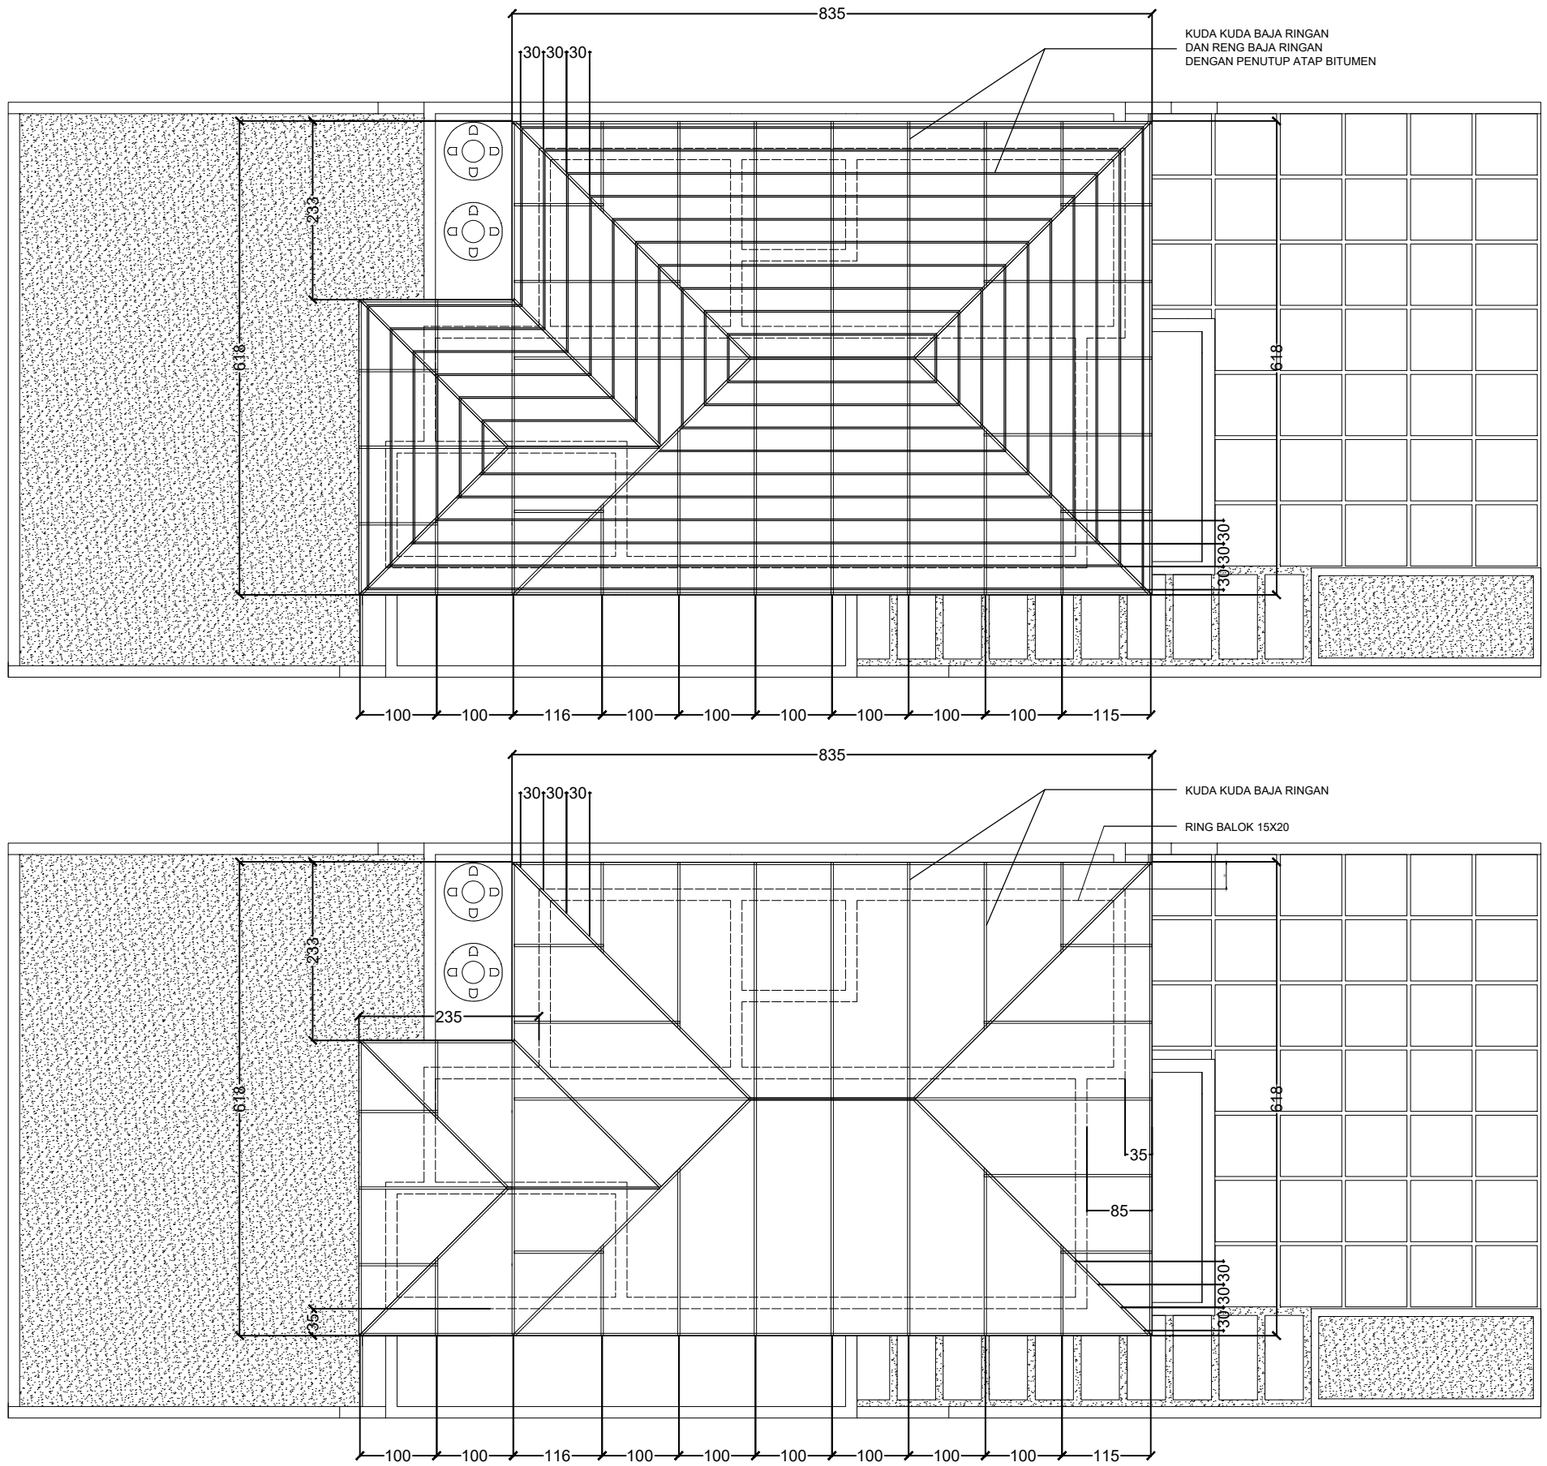

CODE
ARS

DETAIL ATAP

SKALA 1 : 80

ARCHILLES STUDIO

KETERANGAN :

PROJECT :

PERENCANAAN RUMAH HUNIAN
TYPE 65

LOKASI :

BANTARAN NILA, LAMPUNG

OWNER :


.....

PERENCANA :

ARCHILLES TEAM

JUDUL GAMBAR	SKALA

TOTAL HALAMAN	CODE	NO HALAMAN

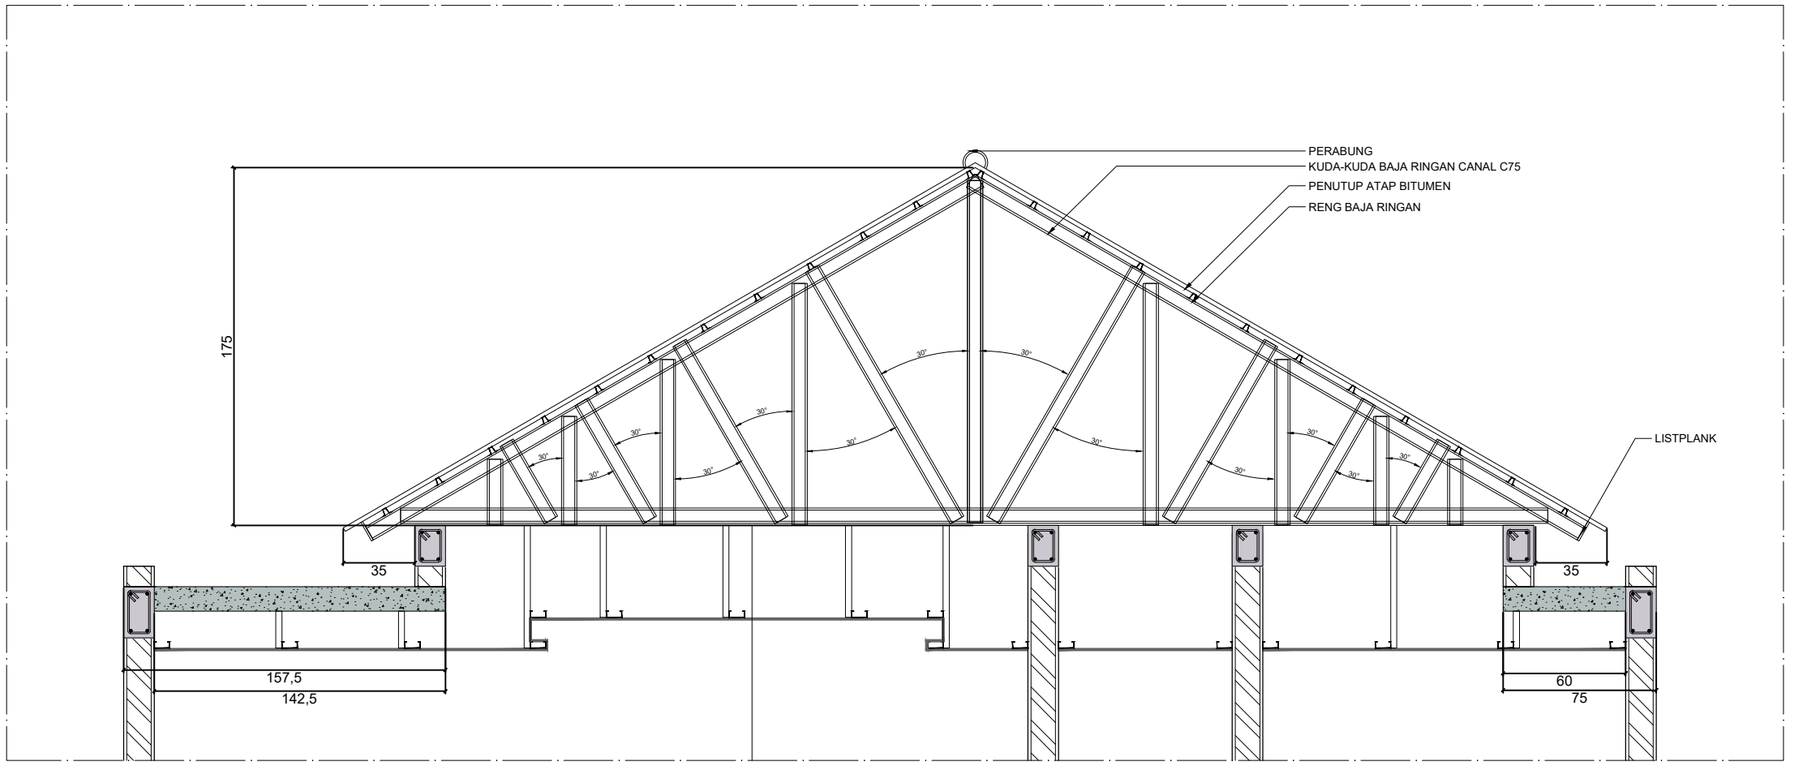

DETAIL POTONGAN ATAP

CODE
ARS

SKALA 1 : 30

ARCHILLES STUDIO

KETERANGAN :

PROJECT :

PERENCANAAN RUMAH HUNIAN
TYPE 65

LOKASI :

BANTARAN NILA, LAMPUNG

OWNER :


.....


PERENCANA :

ARCHILLES TEAM

JUDUL GAMBAR	SKALA

TOTAL HALAMAN	CODE	NO HALAMAN

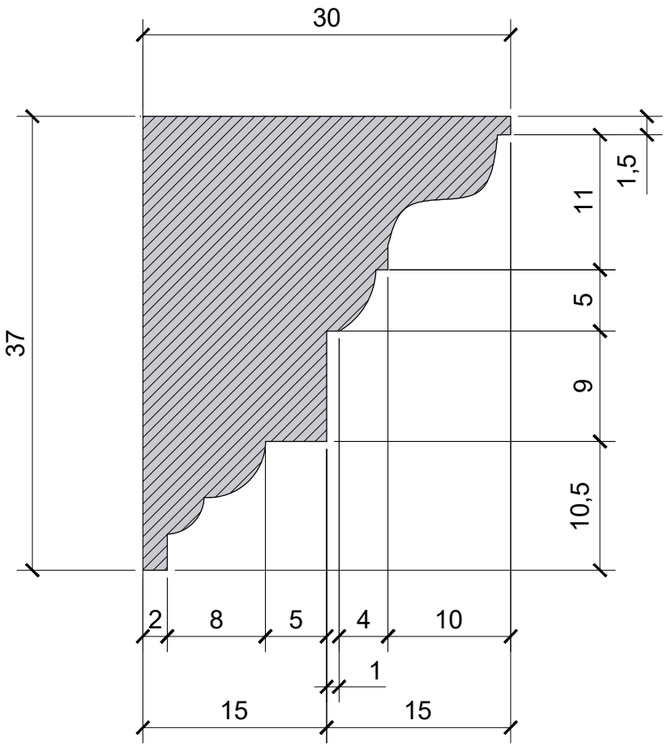

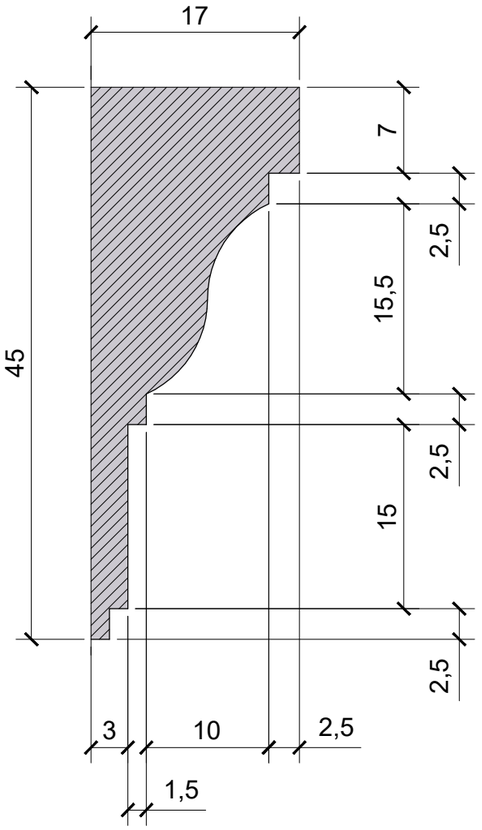

CODE
ARS

DETAIL LIST PROFIL

SKALA 1 : 5

ARCHILLES STUDIO

KETERANGAN :

PROJECT :

PERENCANAAN RUMAH HUNIAN
TYPE 65

LOKASI :

BANTARAN NILA, LAMPUNG

OWNER :


.....

PERENCANA :

ARCHILLES TEAM

JUDUL GAMBAR	SKALA

TOTAL HALAMAN	CODE	NO HALAMAN

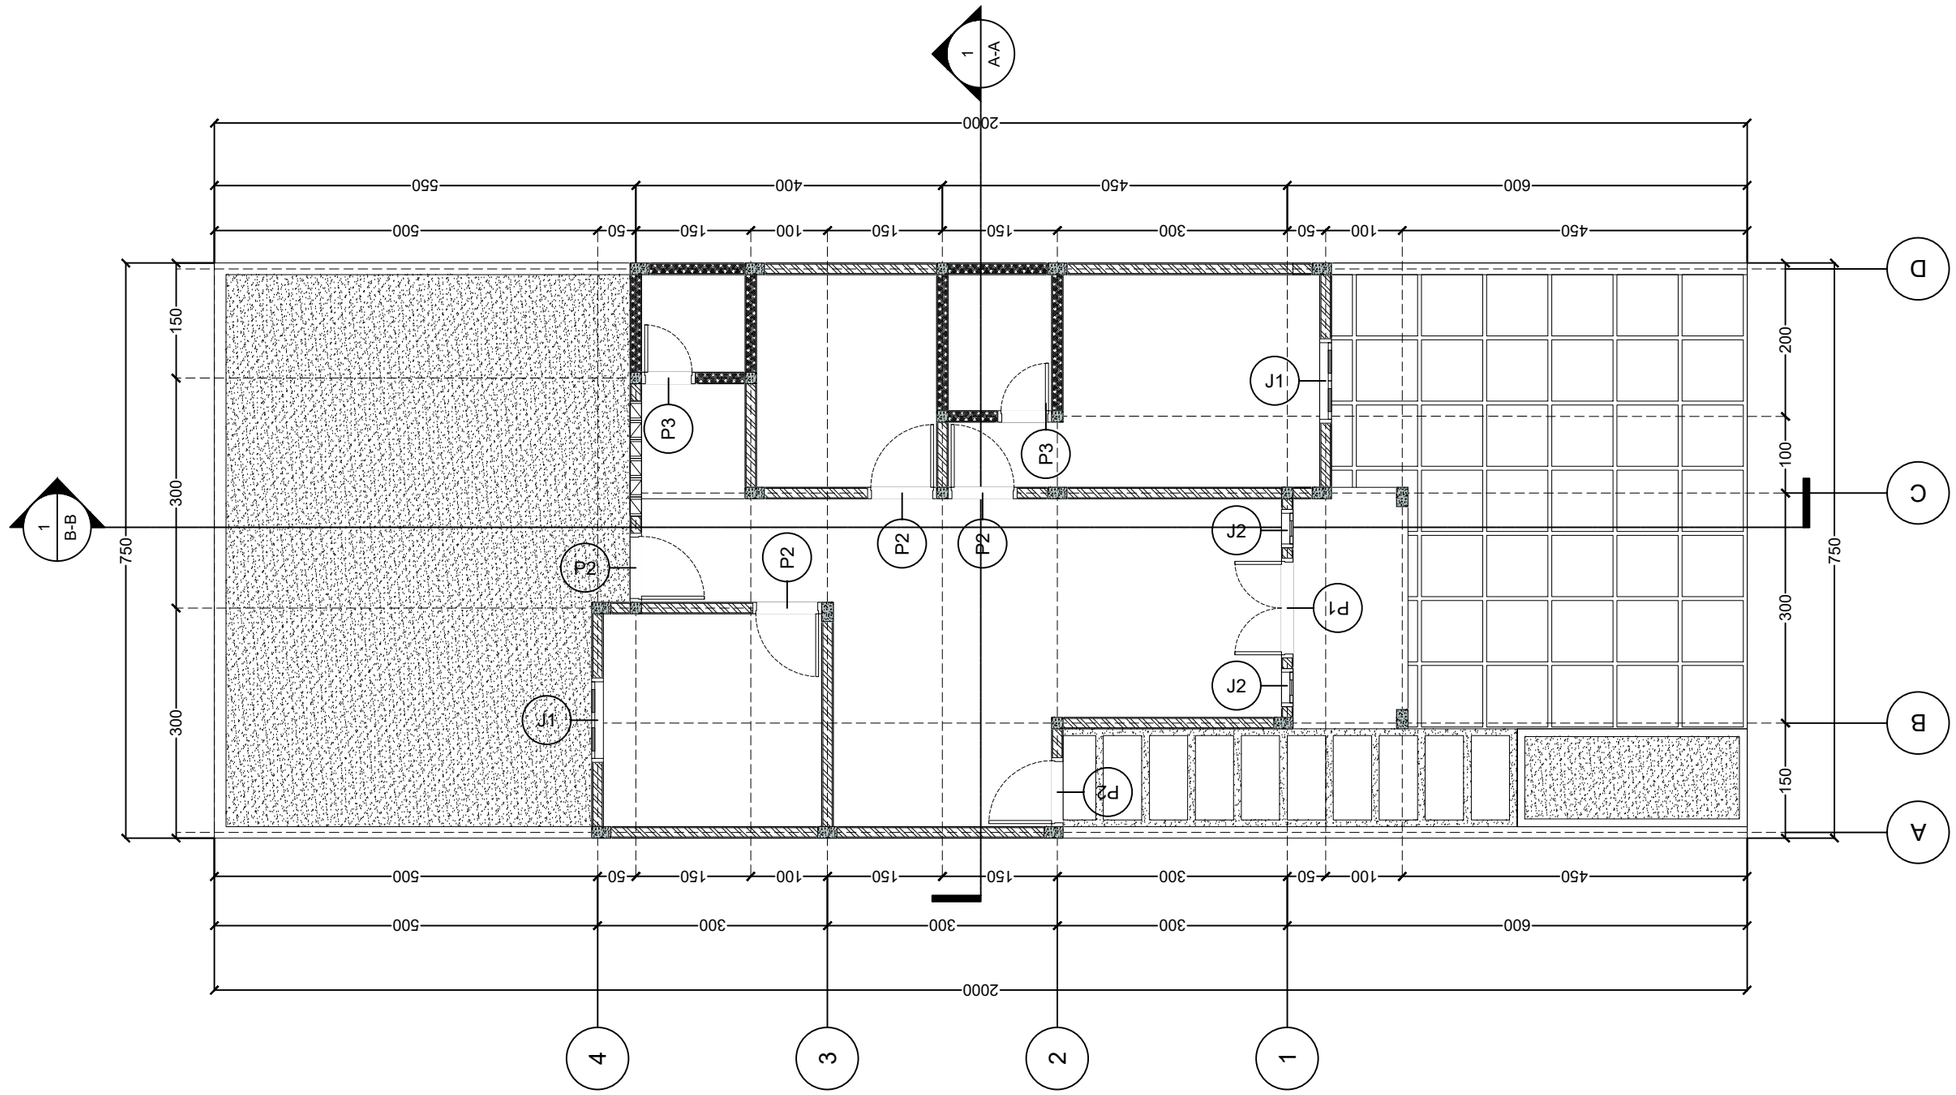

CODE
ARS

DENAH KUZEN

SKALA 1 : 80

ARCHILLES STUDIO

KETERANGAN :

PROJECT :

PERENCANAAN RUMAH HUNIAN
TYPE 65

LOKASI :

BANTARAN NILA, LAMPUNG

OWNER :

.....


PERENCANA :

ARCHILLES TEAM

JUDUL GAMBAR	SKALA


TOTAL HALAMAN	CODE	NO HALAMAN

TIPE : P1	JUMLAH : 1

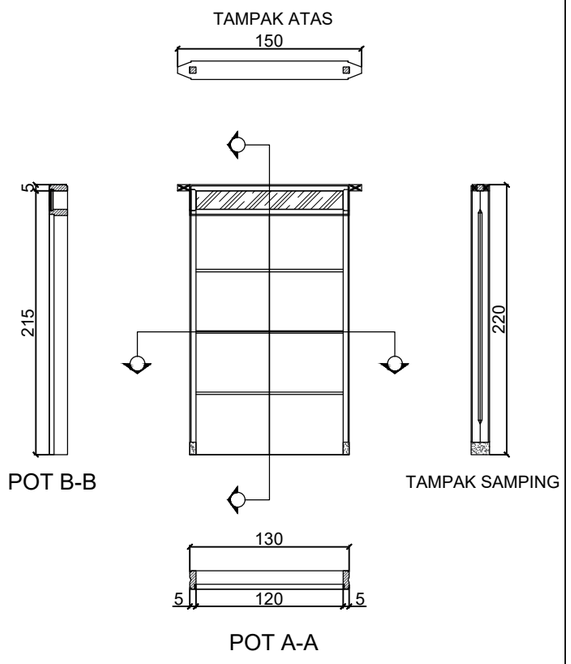


SPESIFIKASI MATERIAL	
KUZEN	KAYU BANIO
PINTU / JENDELA	KAYU SURIAN
KACA	5mm

TIPE : P2	JUMLAH : 5

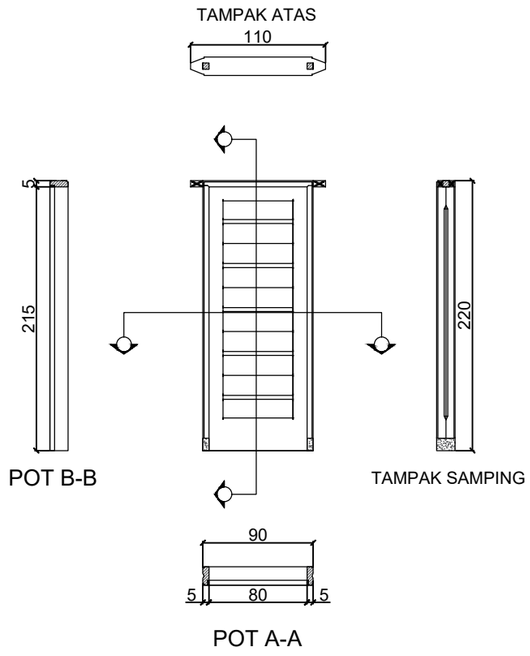

SPESIFIKASI MATERIAL	
KUZEN	KAYU BANIO
PINTU / JENDELA	KAYU SURIAN
KACA	-

TIPE : P3	JUMLAH : 2

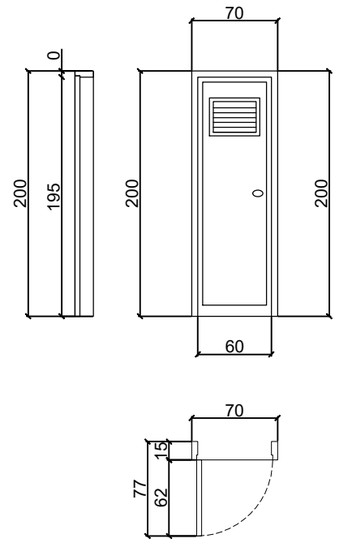

SPESIFIKASI MATERIAL	
KUZEN	PVC
PINTU / JENDELA	PVC
KACA	-

CODE
ARS

DETAIL KUZEN

SKALA 1 : 50

ARCHILLES STUDIO

KETERANGAN :

PROJECT :

PERENCANAAN RUMAH HUNIAN
TYPE 65

LOKASI :

BANTARAN NILA, LAMPUNG

OWNER :

.....


PERENCANA :

ARCHILLES TEAM

JUDUL GAMBAR	SKALA


TOTAL HALAMAN	CODE	NO HALAMAN

TIPE : J1	JUMLAH : 2

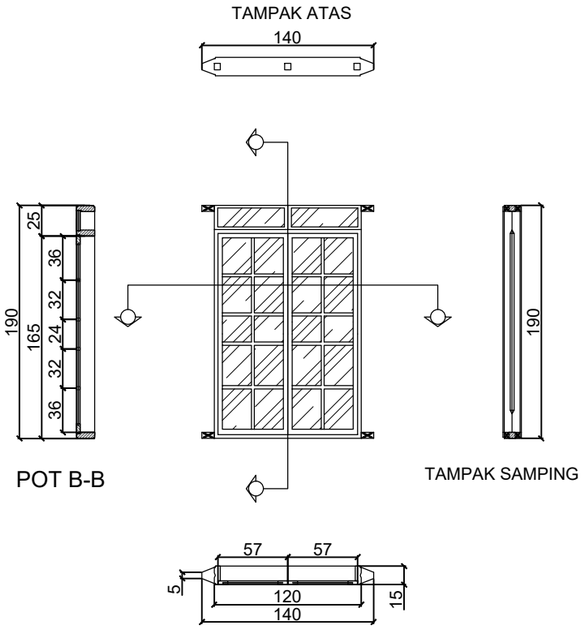

SPESIFIKASI MATERIAL	
KUZEN	KAYU BANIO
PINTU / JENDELA	KAYU SURIAN
KACA	5mm

TIPE : J2	JUMLAH : 2

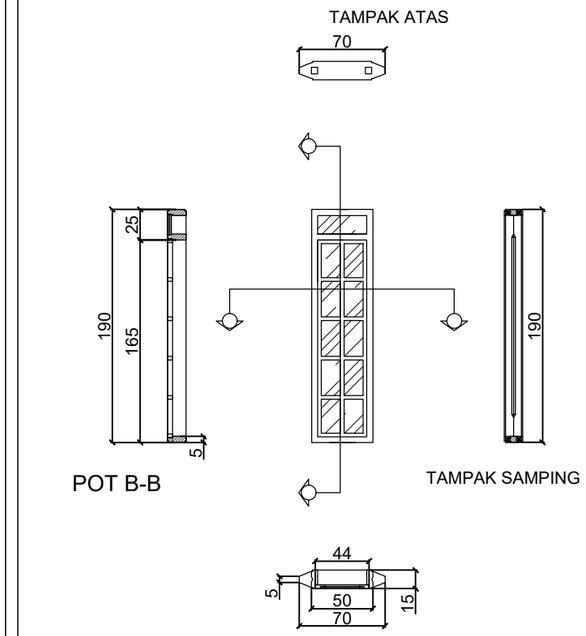

SPESIFIKASI MATERIAL	
KUZEN	KAYU BANIO
PINTU / JENDELA	KAYU SURIAN
KACA	5mm

CODE
ARS

DETAIL KUZEN

SKALA 1 : 50

ARCHILLES STUDIO

KETERANGAN :

PROJECT :

PERENCANAAN RUMAH HUNIAN
TYPE 65

LOKASI :

BANTARAN NILA, LAMPUNG

OWNER :


.....


PERENCANA :


ARCHILLES TEAM

JUDUL GAMBAR	SKALA

TOTAL HALAMAN	CODE	NO HALAMAN

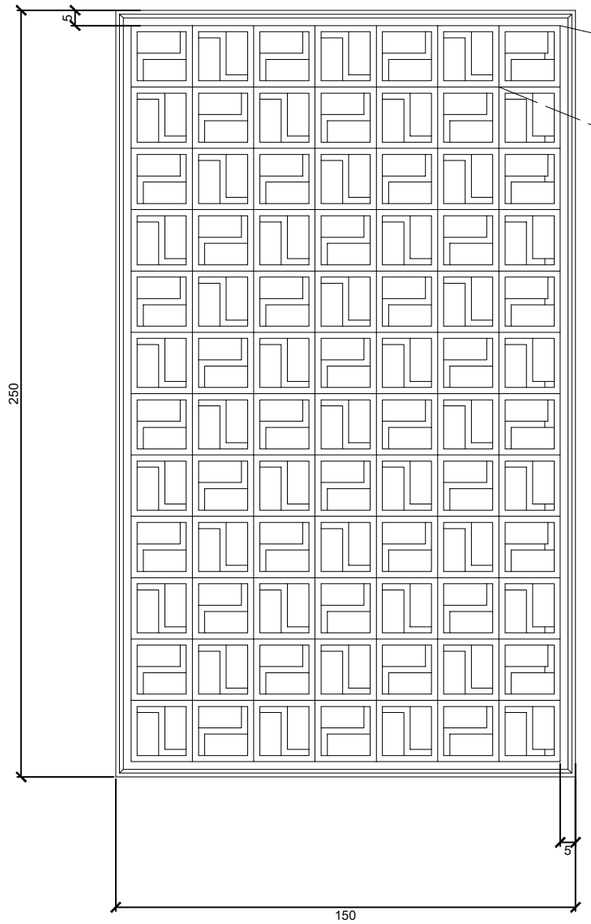

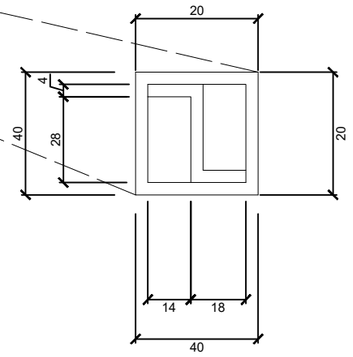

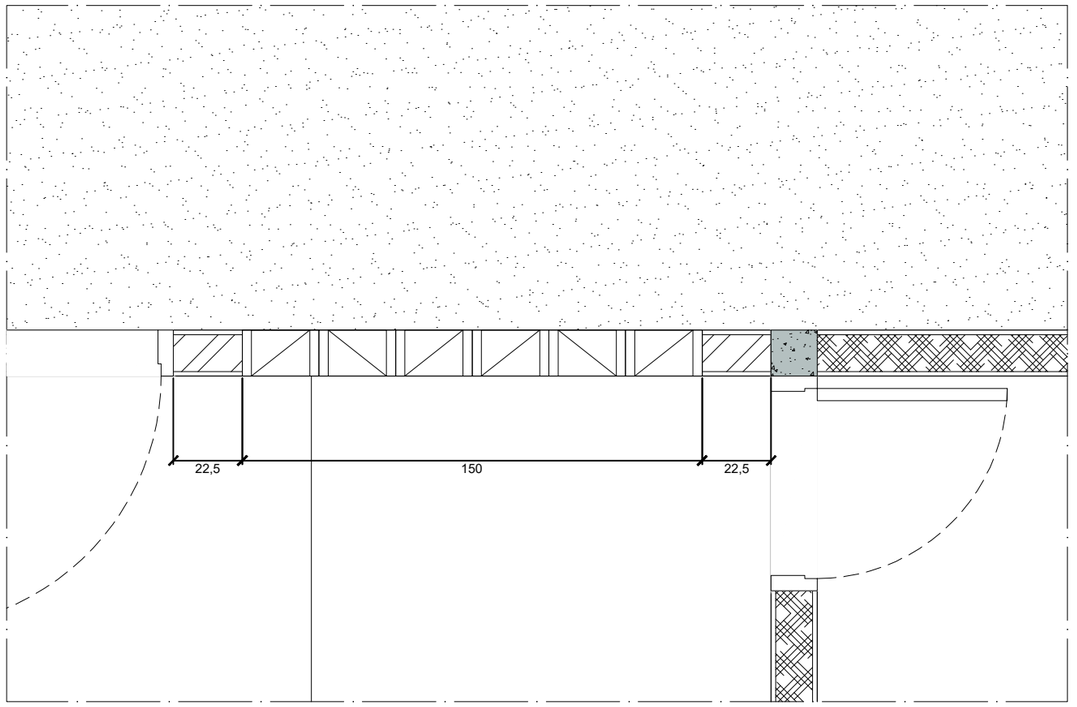

CODE
ARS

DETAIL PEMASANGAN ROSTER

SKALA 1 : 20

ARCHILLES STUDIO

KETERANGAN :

PROJECT :

PERENCANAAN RUMAH HUNIAN
TYPE 65

LOKASI :

BANTARAN NILA, LAMPUNG

OWNER :


.....

PERENCANA :

ARCHILLES TEAM

JUDUL GAMBAR	SKALA

TOTAL HALAMAN	CODE	NO HALAMAN

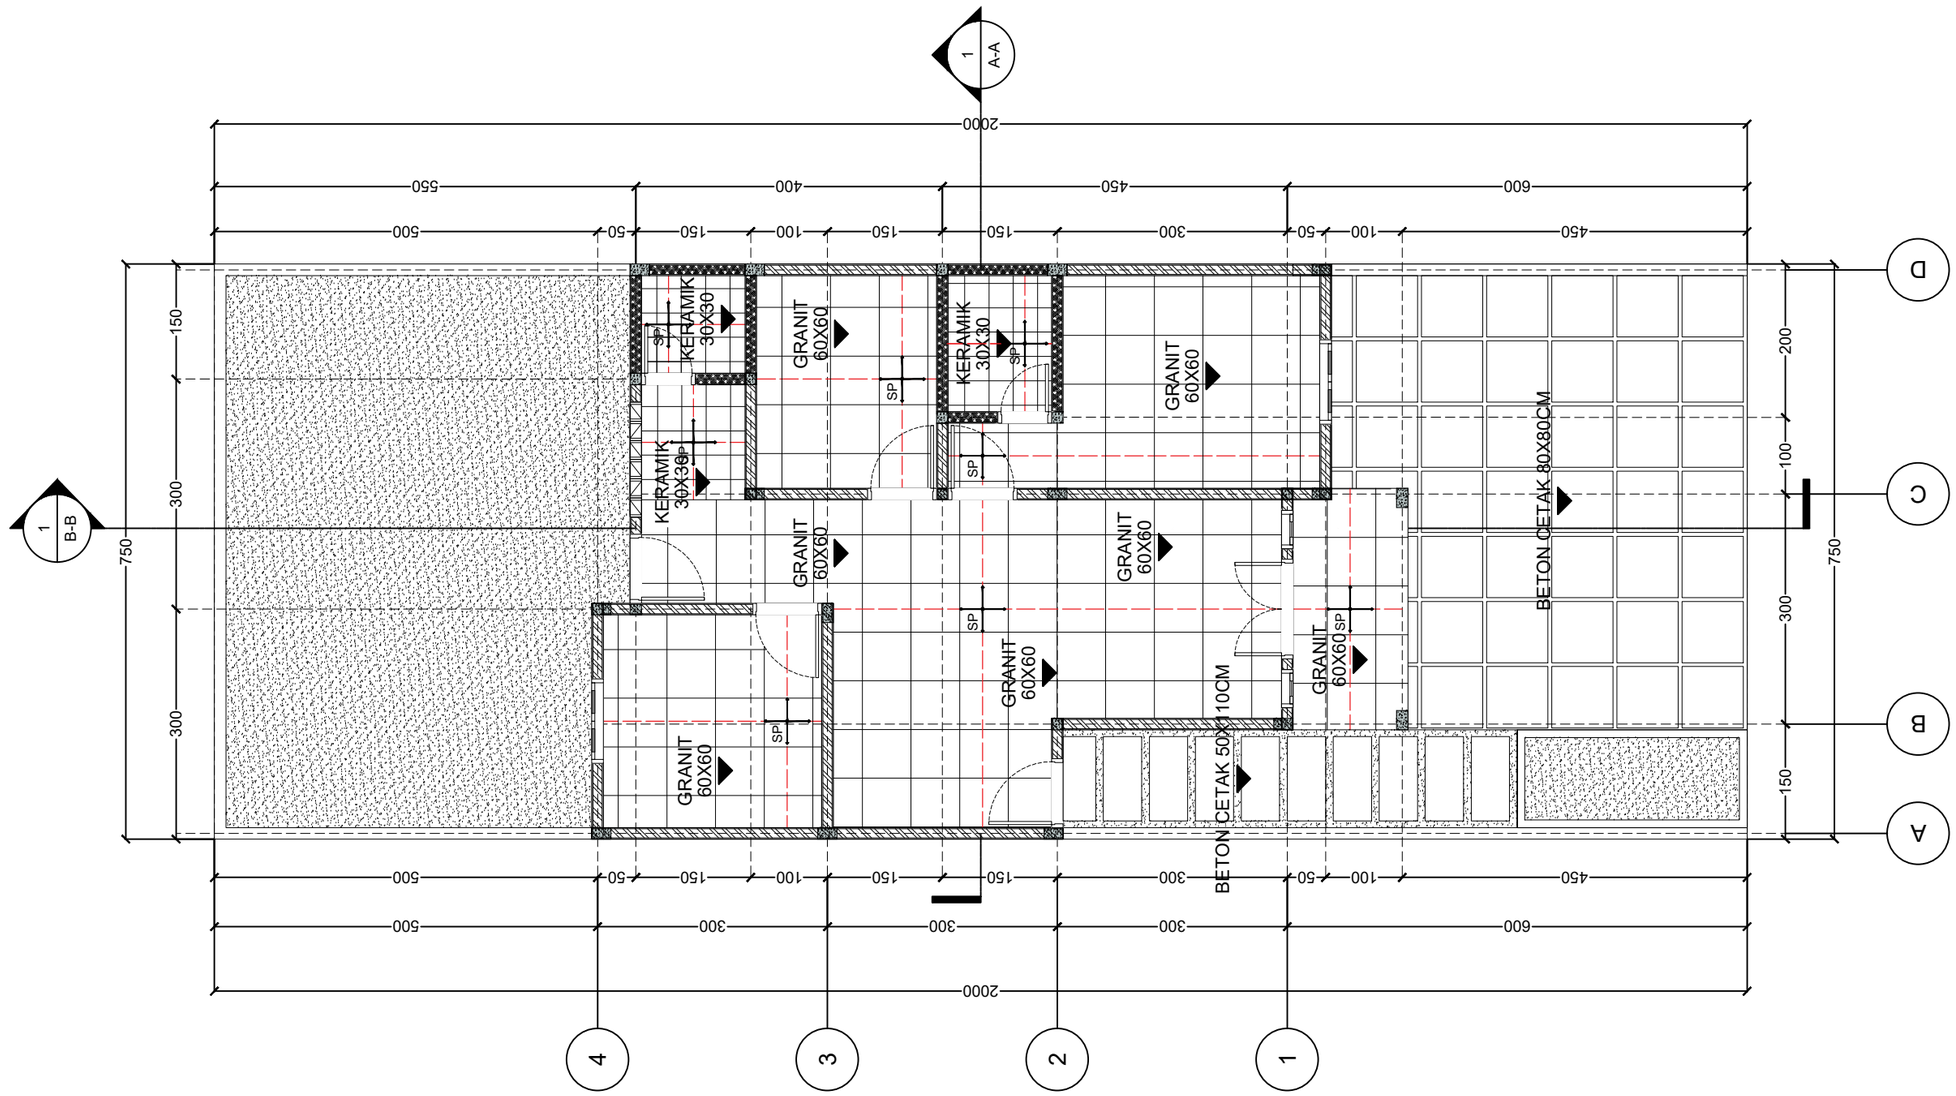

DENAH PEMASANGAN PENUTUP LANTAI

CODE
ARS

SKALA 1 : 80

ARCHILLES STUDIO

KETERANGAN :

PROJECT :

PERENCANAAN RUMAH HUNIAN
TYPE 65

LOKASI :

BANTARAN NILA, LAMPUNG

OWNER :


.....

PERENCANA :

ARCHILLES TEAM

JUDUL GAMBAR	SKALA

TOTAL HALAMAN	CODE	NO HALAMAN

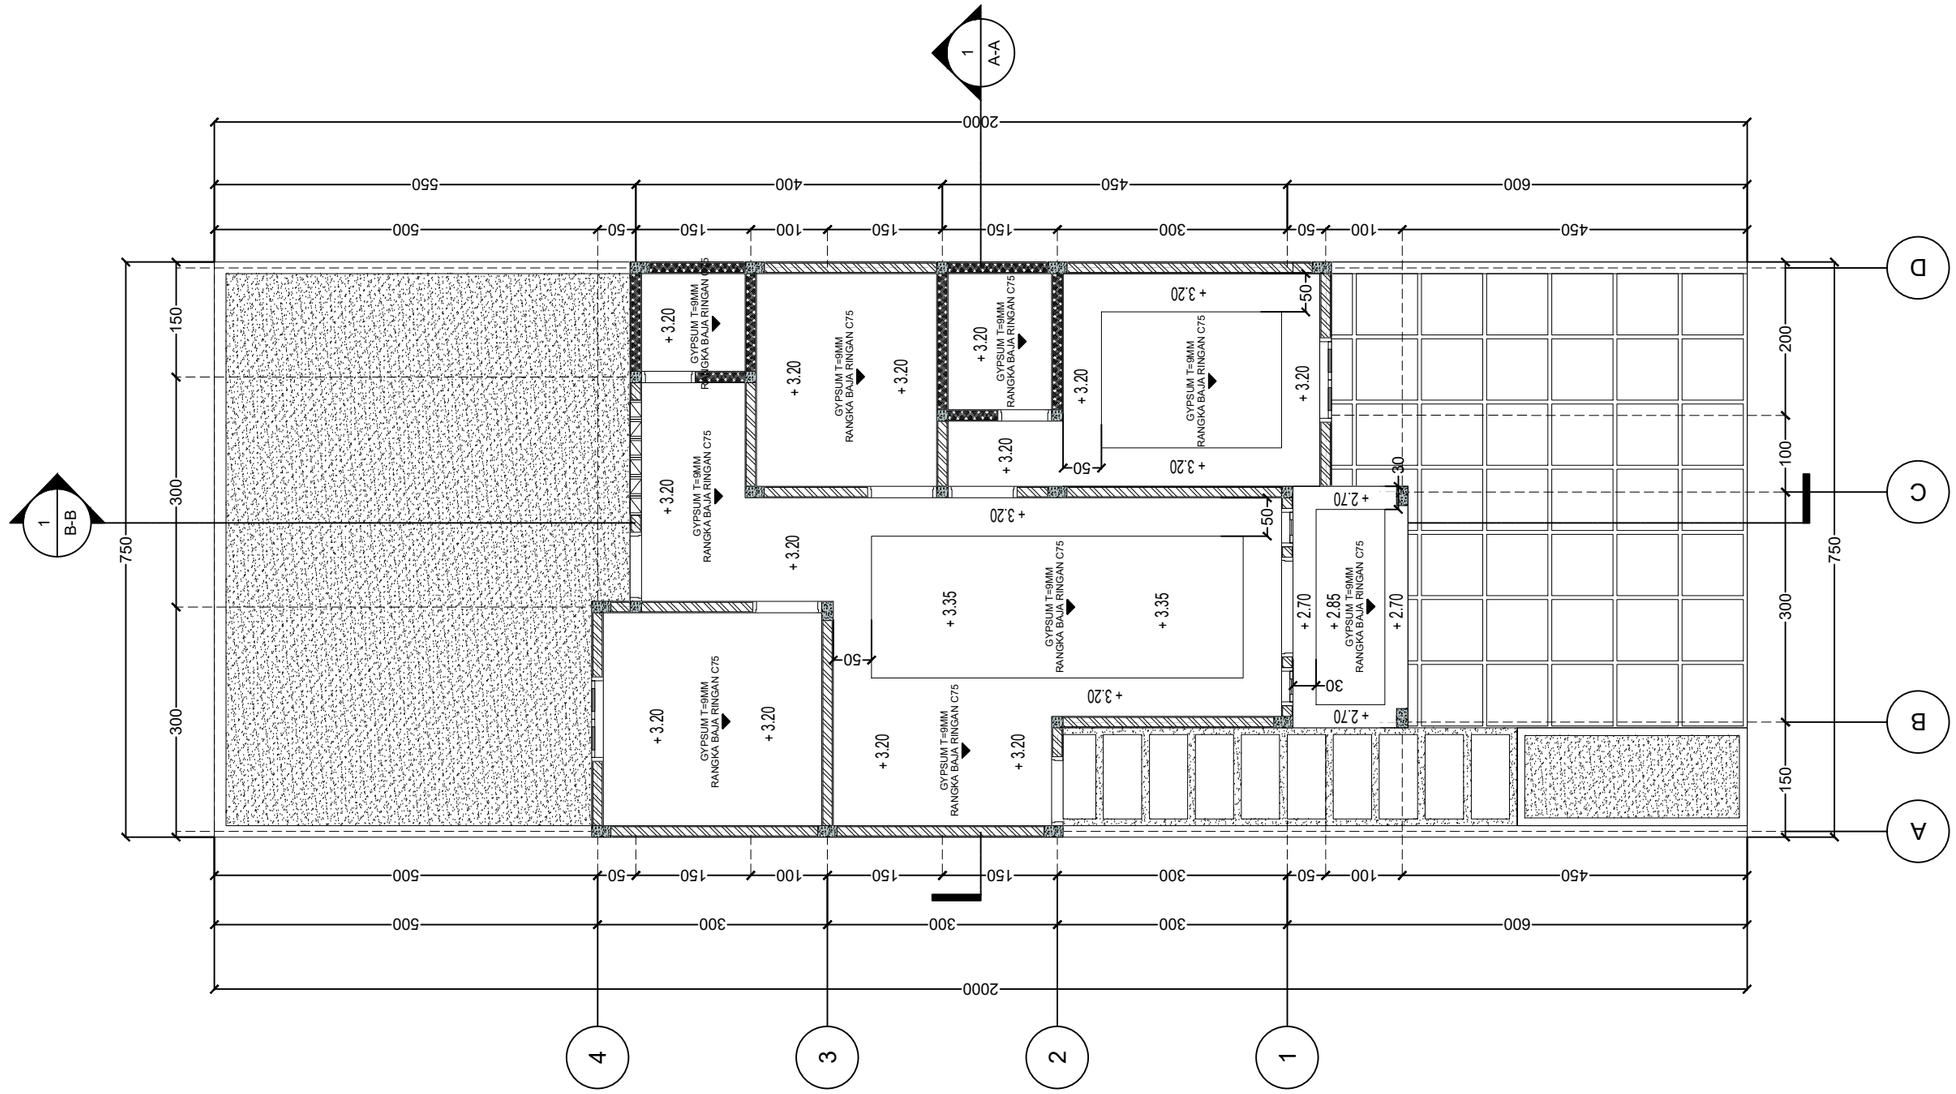

CODE
ARS

DENAH PEMASANGAN PLAVOND

SKALA 1 : 80

ARCHILLES STUDIO

KETERANGAN :

PROJECT :

PERENCANAAN RUMAH HUNIAN
TYPE 65

LOKASI :

BANTARAN NILA, LAMPUNG

OWNER :


.....

PERENCANA :

ARCHILLES TEAM

JUDUL GAMBAR	SKALA

TOTAL HALAMAN	CODE	NO HALAMAN

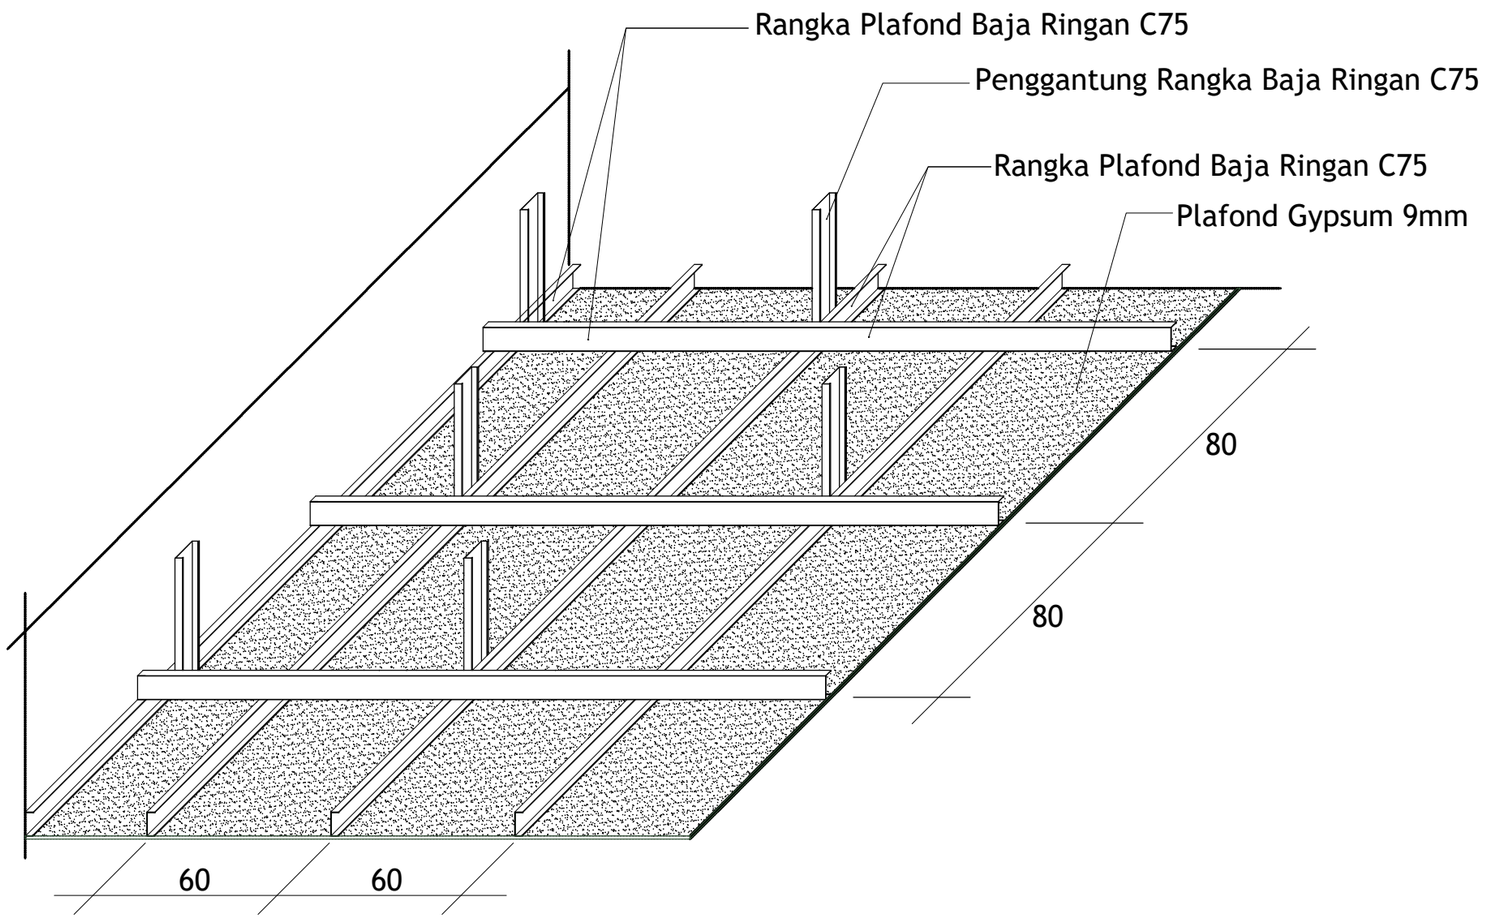

CODE
ARS

PERSPEKTIF RANGKA PLAVOND

SKALA 1 : 20

ARCHILLES STUDIO

KETERANGAN :

PROJECT :

PERENCANAAN RUMAH HUNIAN
TYPE 65

LOKASI :

BANTARAN NILA, LAMPUNG

OWNER :

.....

PERENCANA :

ARCHILLES TEAM

JUDUL GAMBAR	SKALA


TOTAL HALAMAN	CODE	NO HALAMAN

ARCHILLES
STUDIO

STRUKTUR

CODE :

STR

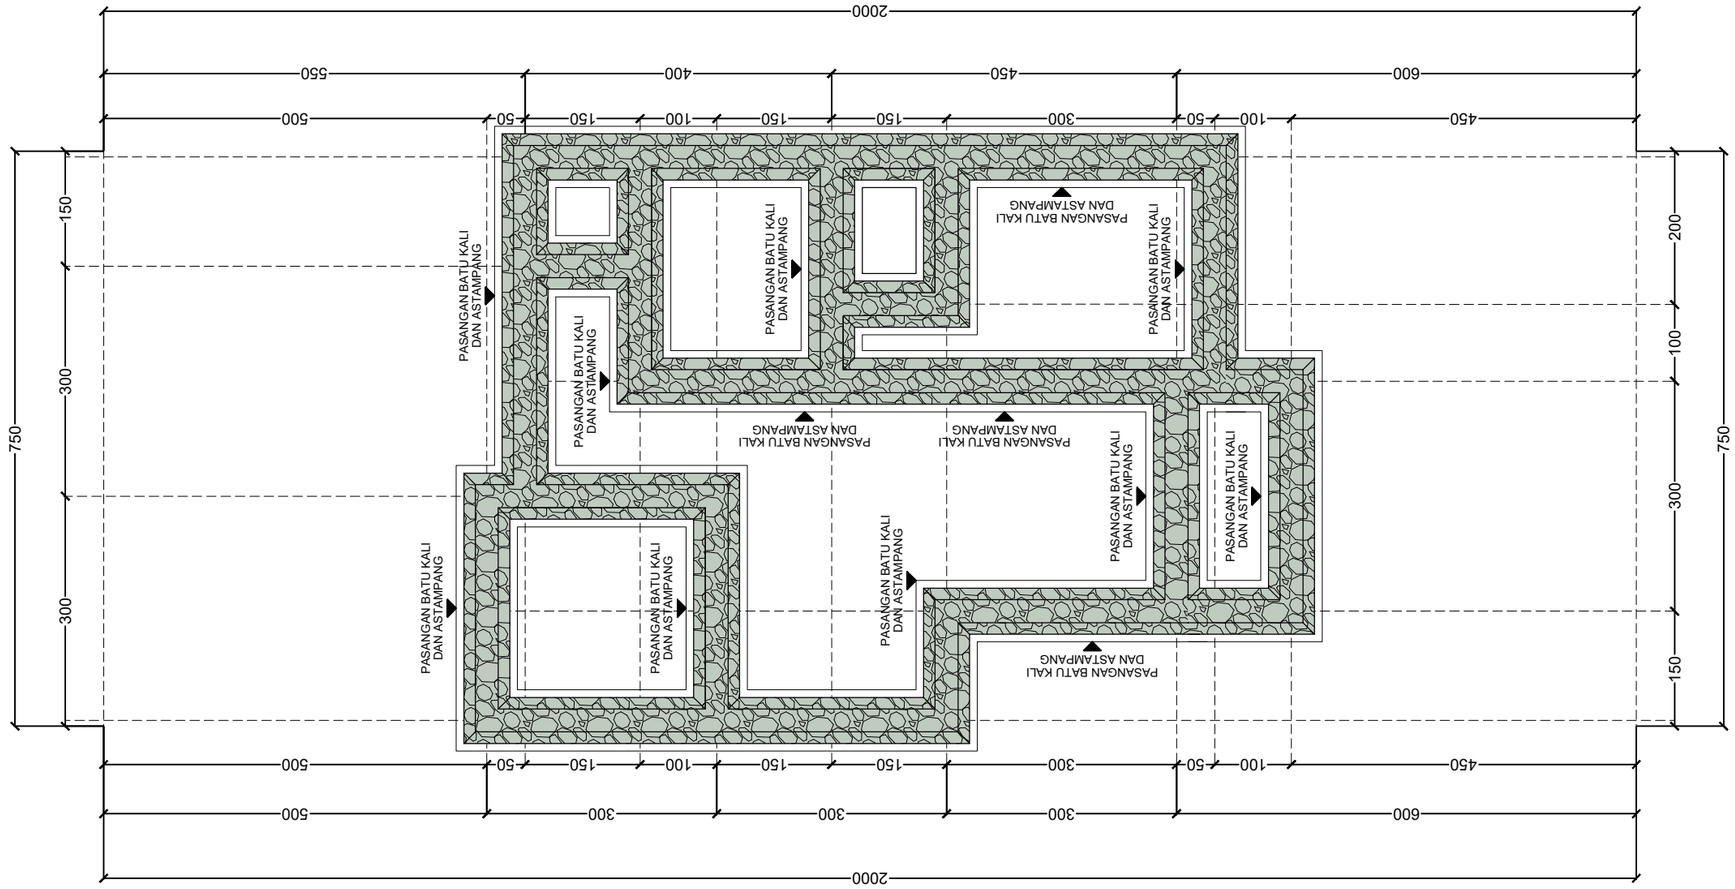

CODE
STR

DENAH PONDASI BATU KALI

SKALA 1 : 80

ARCHILLES STUDIO

KETERANGAN :

PROJECT :

PERENCANAAN RUMAH HUNIAN
TYPE 65

LOKASI :

BANTARAN NILA, LAMPUNG

OWNER :


.....

PERENCANA :

ARCHILLES TEAM

JUDUL GAMBAR	SKALA

TOTAL HALAMAN	CODE	NO HALAMAN

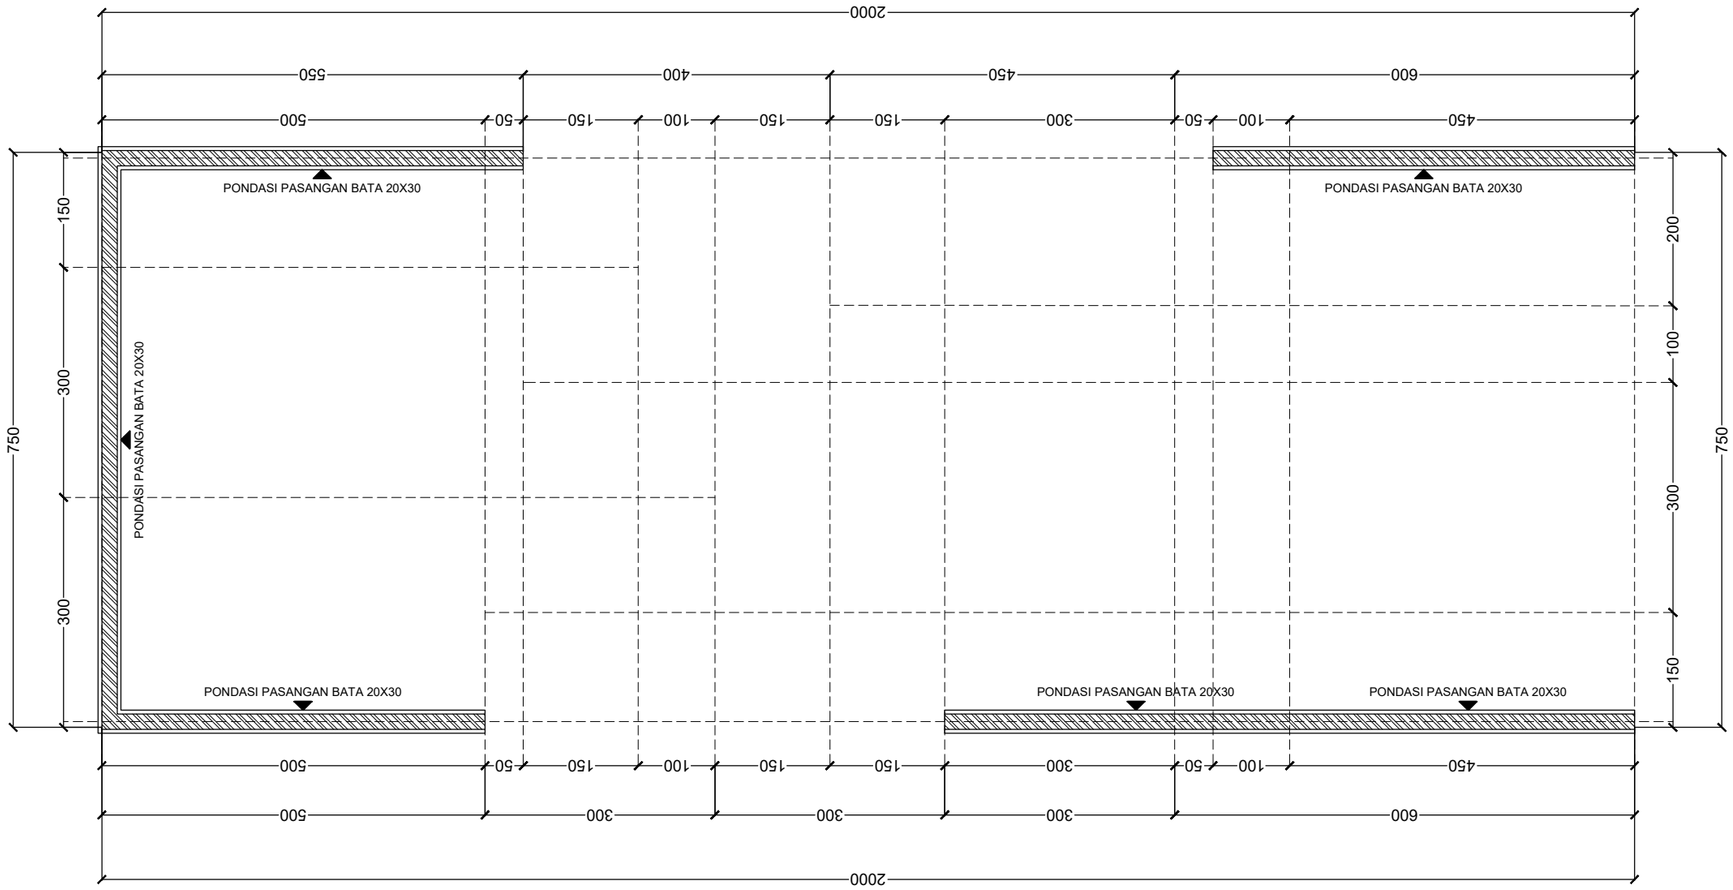

CODE
STR

DENAH PONDASI PASANGAN BATA

SKALA 1 : 80

ARCHILLES STUDIO

KETERANGAN :

PROJECT :

PERENCANAAN RUMAH HUNIAN
TYPE 65

LOKASI :

BANTARAN NILA, LAMPUNG

OWNER :


.....

PERENCANA :

ARCHILLES TEAM

JUDUL GAMBAR	SKALA


TOTAL HALAMAN	CODE	NO HALAMAN

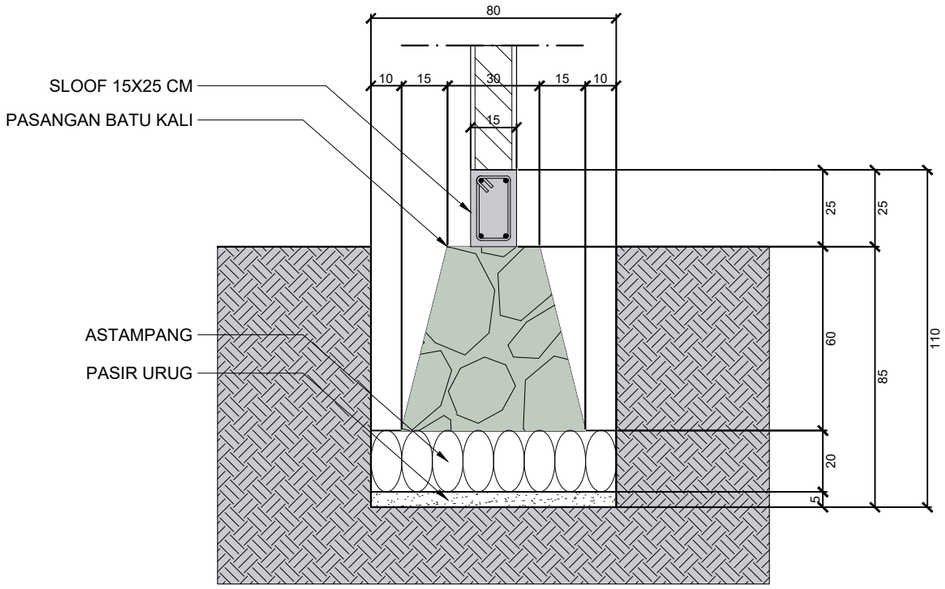

DETAIL PONDASI PASANGAN BATU KALI

CODE STR

SKALA 1 : 20

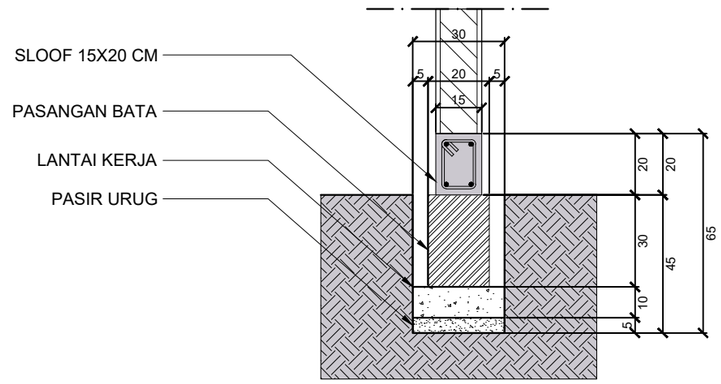

DETAIL PONDASI PASANGAN BATU BATA

CODE STR

SKALA 1 : 20

ARCHILLES STUDIO

KETERANGAN :

PROJECT :

PERENCANAAN RUMAH HUNIAN
TYPE 65

LOKASI :

BANTARAN NILA, LAMPUNG

OWNER :


.....

PERENCANA :

ARCHILLES TEAM

JUDUL GAMBAR	SKALA

TOTAL HALAMAN	CODE	NO HALAMAN

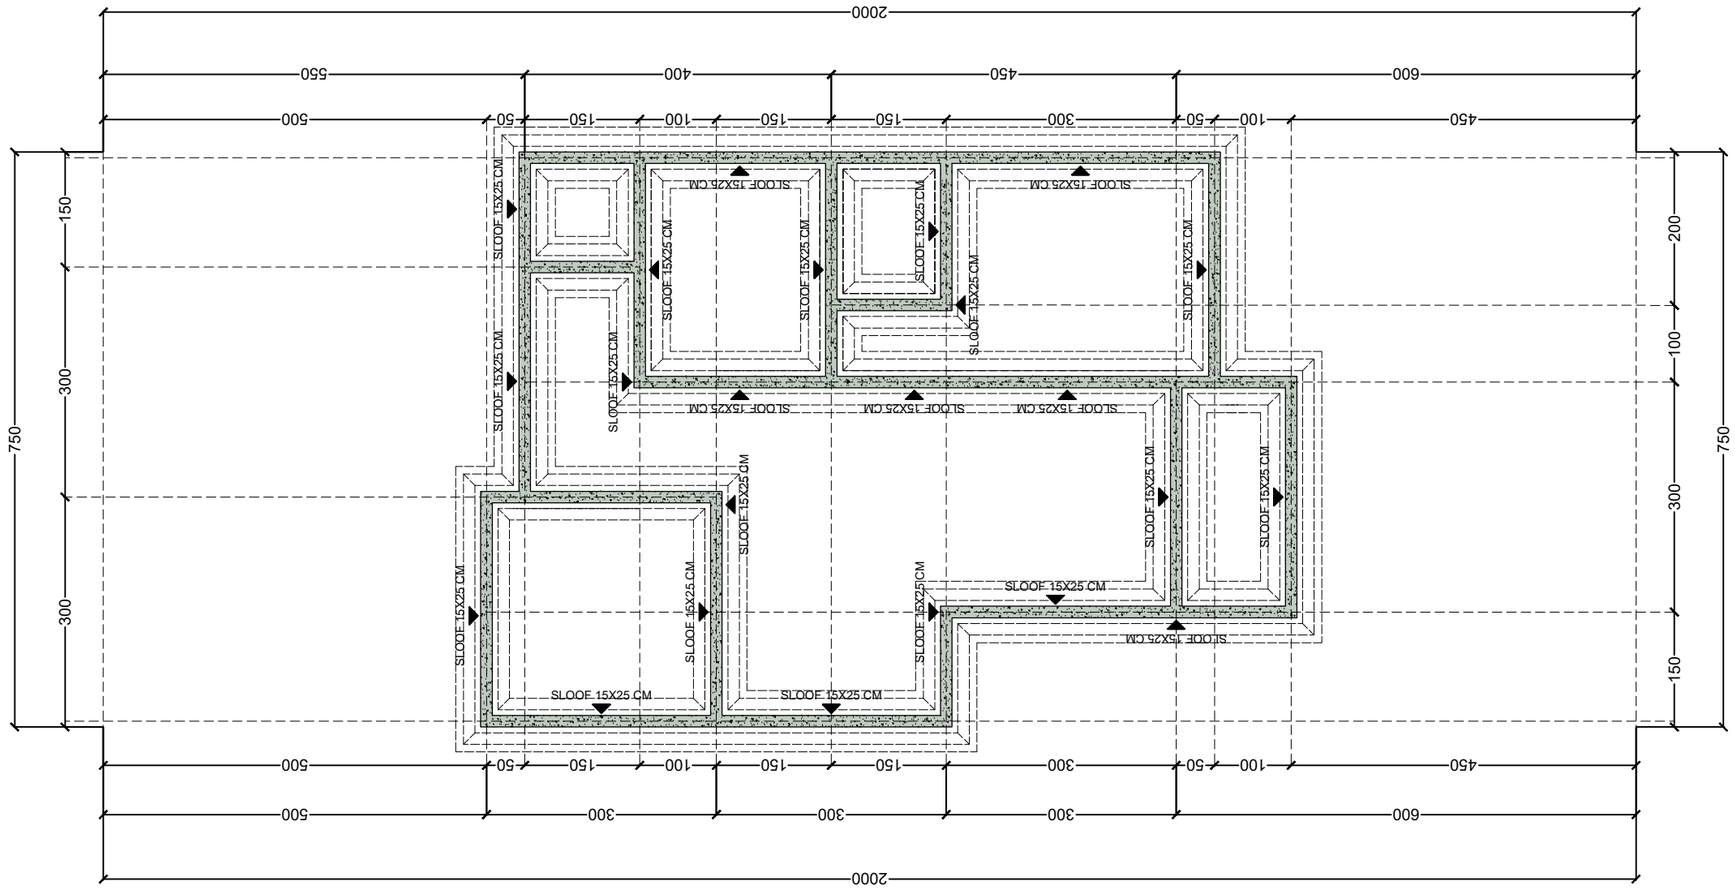

GEOMETRI SLOOF SLF1		
DIMENSI	15 x 25	
TUL. ATAS	2 Ø 12	2 Ø 12
TUL.TENGAH	-	-
TUL. BAWAH	2 Ø 12	2 Ø 12
JARAK BEUGEL	¼ H	½ H
	Ø8 - 10	Ø8 - 20

CODE
STR

DENAH SLOOF 15X25

SKALA 1 : 80

ARCHILLES STUDIO

KETERANGAN :

PROJECT :

PERENCANAAN RUMAH HUNIAN
TYPE 65

LOKASI :

BANTARAN NILA, LAMPUNG

OWNER :


.....

PERENCANA :

ARCHILLES TEAM

JUDUL GAMBAR	SKALA

TOTAL HALAMAN	CODE	NO HALAMAN

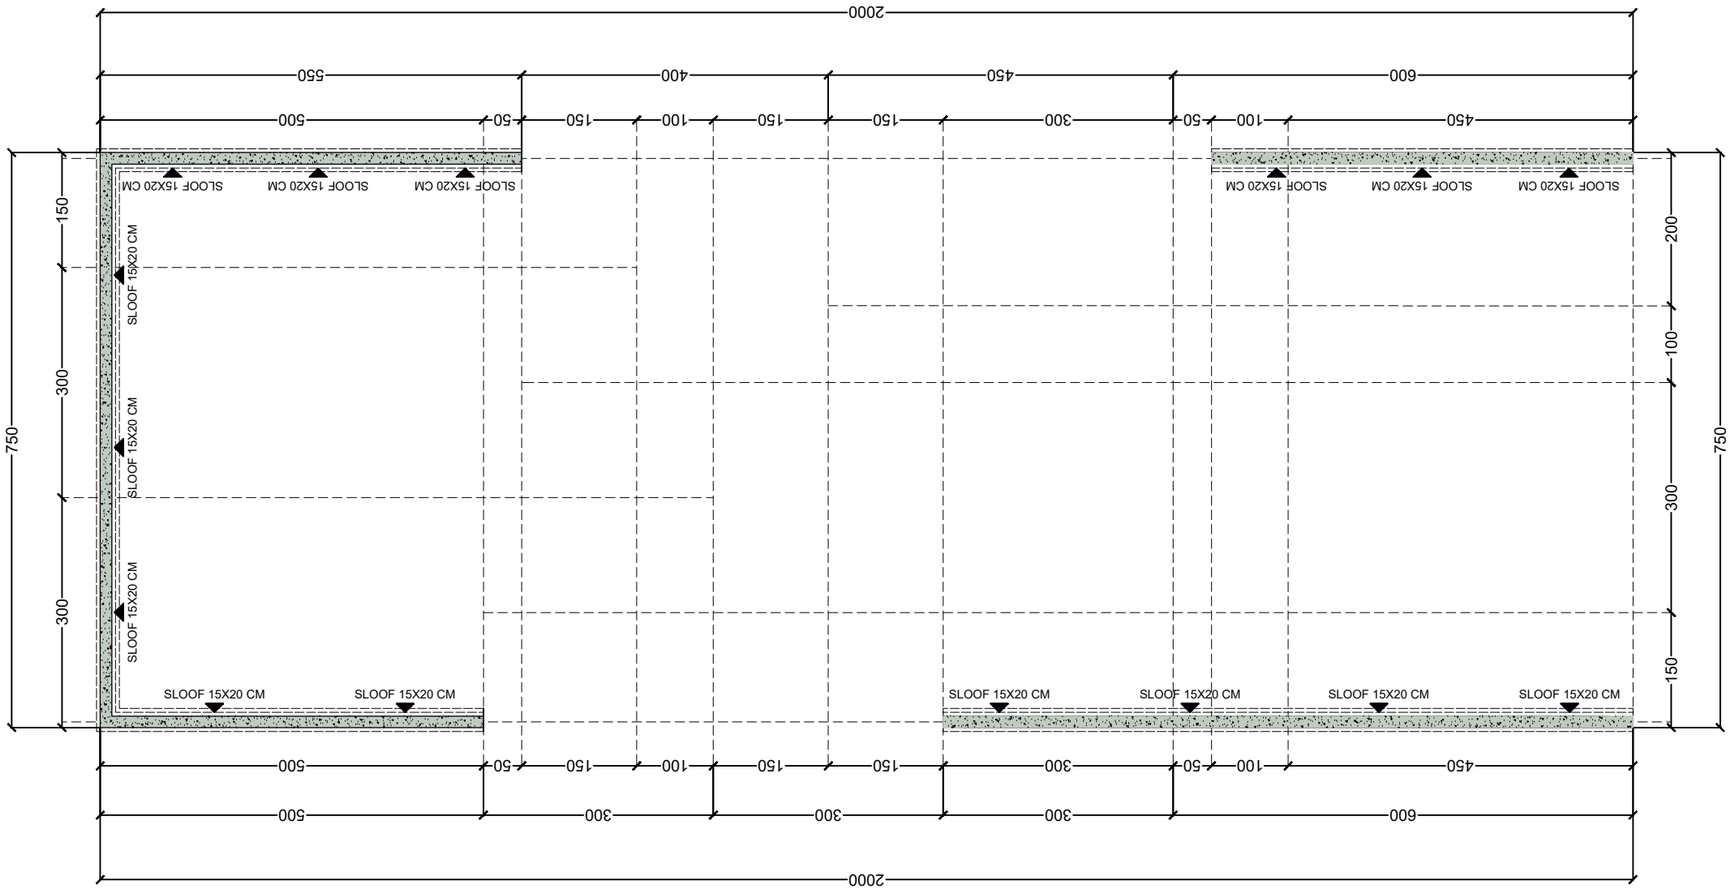

CODE
STR

DENAH SLOOF 15X20

SKALA 1 : 80

GEOMETRI SLOOF SLF 2		
DIMENSI	15 x 20	
TUL. ATAS	2 Ø 12	2 Ø 12
TUL.TENGAH	-	-
TUL. BAWAH	2 Ø 12	2 Ø 12
JARAK BEUGEL	¼ H	½ H
	Ø8 - 10	Ø8 - 20

ARCHILLES STUDIO

KETERANGAN :

PROJECT :

PERENCANAAN RUMAH HUNIAN
TYPE 65

LOKASI :

BANTARAN NILA, LAMPUNG

OWNER :


.....

PERENCANA :

ARCHILLES TEAM

JUDUL GAMBAR	SKALA

TOTAL HALAMAN	CODE	NO HALAMAN

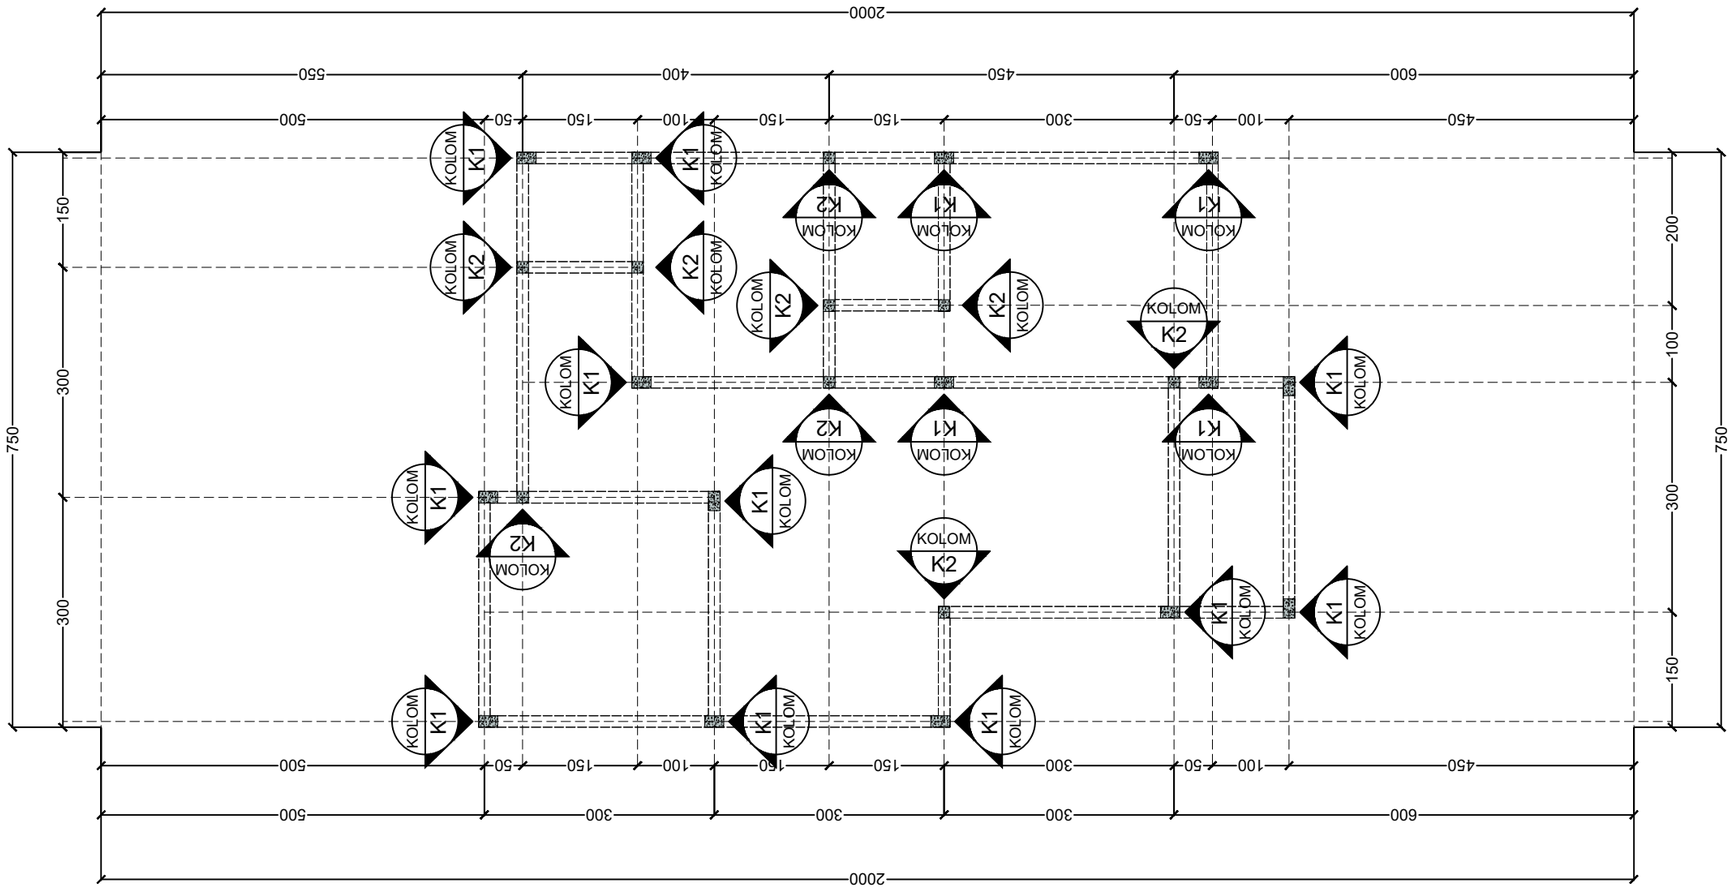

GEOMETRI KOLOM K1		
DIMENSI	15 x 25	
TUL. ATAS	2 Ø 12	2 Ø 12
TUL.TENGAH	-	-
TUL. BAWAH	2 Ø 12	2 Ø 12
JARAK BEUGEL	¼ H	½ H
	Ø8 - 10	Ø8 - 15

GEOMETRI KOLOM K2		
DIMENSI	15 x 15	
TUL. ATAS	2 Ø 12	2 Ø 12
TUL.TENGAH	-	-
TUL. BAWAH	2 Ø 12	2 Ø 12
JARAK BEUGEL	¼ H	½ H
	Ø8 - 10	Ø8 - 15

CODE
STR

DENAH KOLOM BANGUNAN

SKALA 1 : 80

ARCHILLES STUDIO

KETERANGAN :

PROJECT :

PERENCANAAN RUMAH HUNIAN
TYPE 65

LOKASI :

BANTARAN NILA, LAMPUNG

OWNER :


.....

PERENCANA :

ARCHILLES TEAM

JUDUL GAMBAR	SKALA

TOTAL HALAMAN	CODE	NO HALAMAN

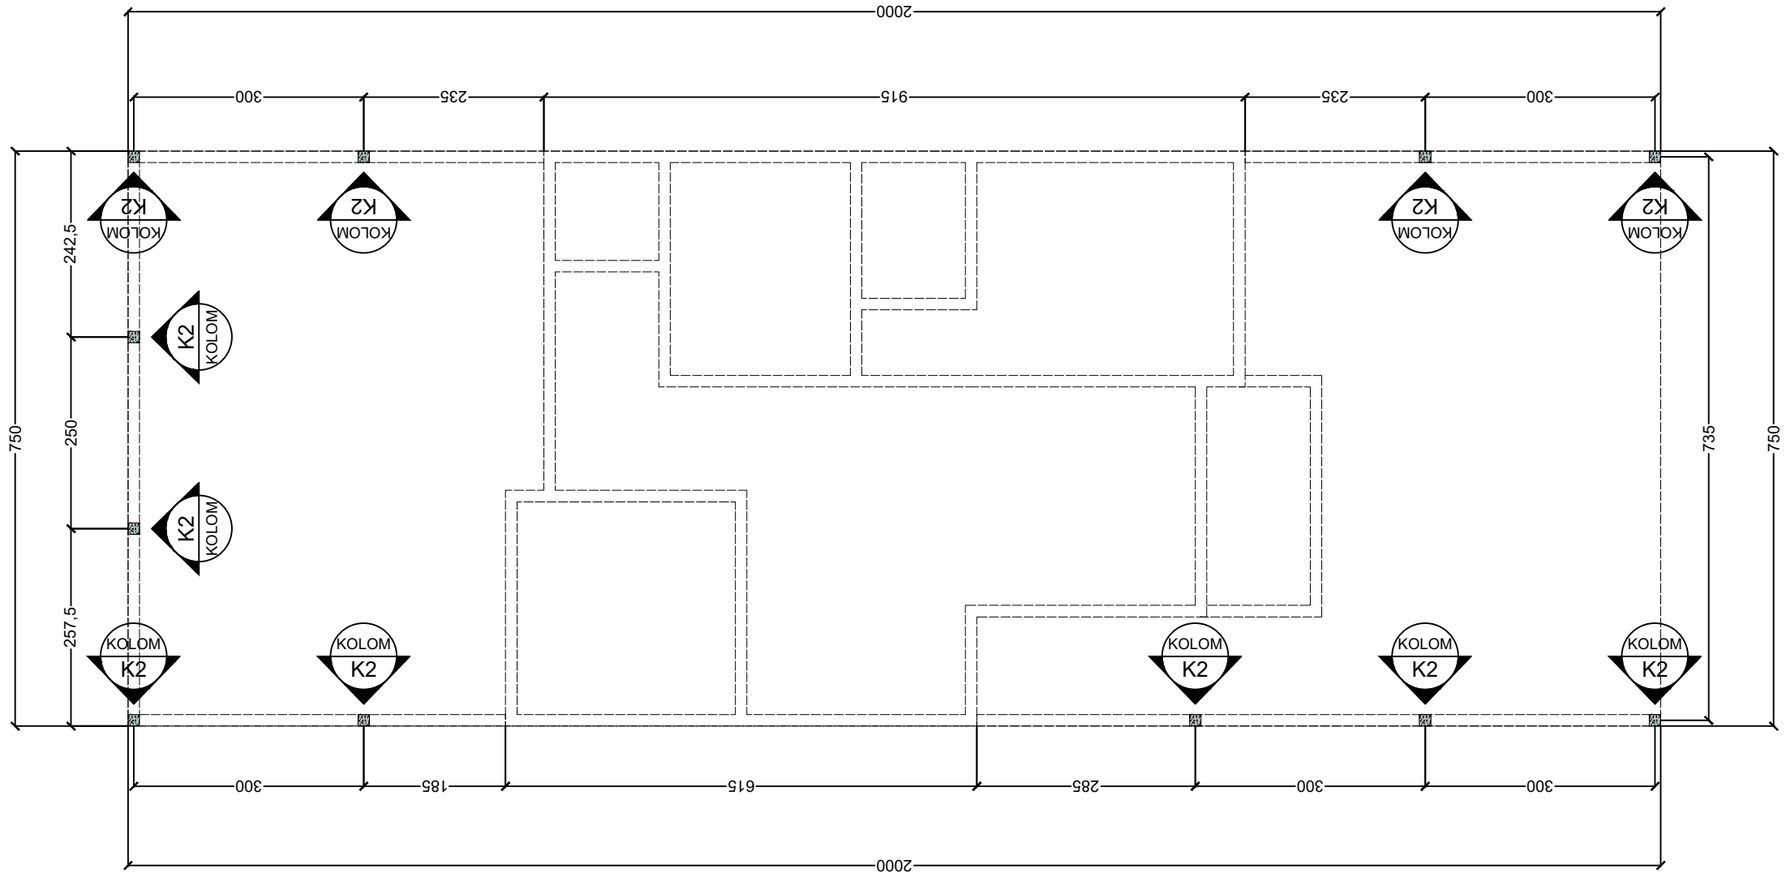

DENAH KOLOM PAGAR TINGGI 2M

CODE
STR

SKALA 1 : 80

GEOMETRI KOLOM K2		
DIMENSI	15 x 15	
TUL. ATAS	2 Ø 12	2 Ø 12
TUL.TENGAH	-	-
TUL. BAWAH	2 Ø 12	2 Ø 12
JARAK BEUGEL	¼ H	½ H
	Ø8 - 10	Ø8 - 15

ARCHILLES STUDIO

KETERANGAN :

PROJECT :

PERENCANAAN RUMAH HUNIAN
TYPE 65

LOKASI :

BANTARAN NILA, LAMPUNG

OWNER :


.....

PERENCANA :

ARCHILLES TEAM

JUDUL GAMBAR	SKALA

TOTAL HALAMAN	CODE	NO HALAMAN

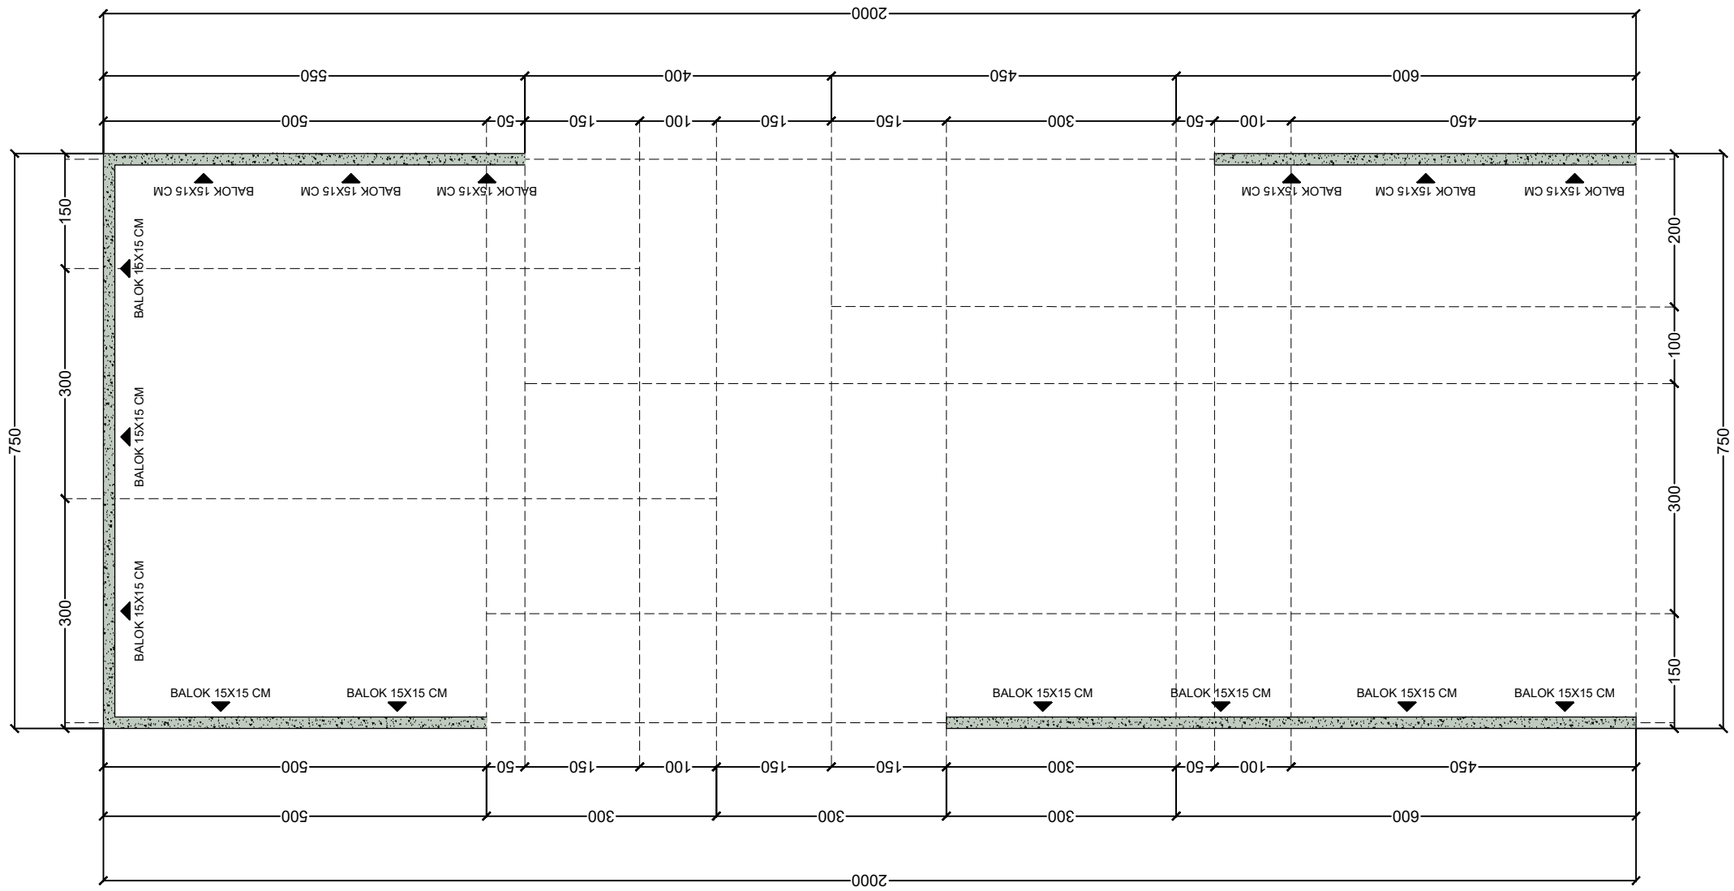

CODE
STR

DENAH BALOK ELEVASI + 2.00

SKALA 1 : 80

GEOMETRI BALOK B2		
DIMENSI	15 x 15	
TUL. ATAS	2 Ø 12	2 Ø 12
TUL.TENGAH	-	-
TUL. BAWAH	2 Ø 12	2 Ø 12
JARAK BEUGEL	¼ H	½ H
	Ø8 - 10	Ø8 - 15

ARCHILLES STUDIO

KETERANGAN :

PROJECT :

PERENCANAAN RUMAH HUNIAN
TYPE 65

LOKASI :

BANTARAN NILA, LAMPUNG

OWNER :


.....

PERENCANA :

ARCHILLES TEAM

JUDUL GAMBAR	SKALA

TOTAL HALAMAN	CODE	NO HALAMAN

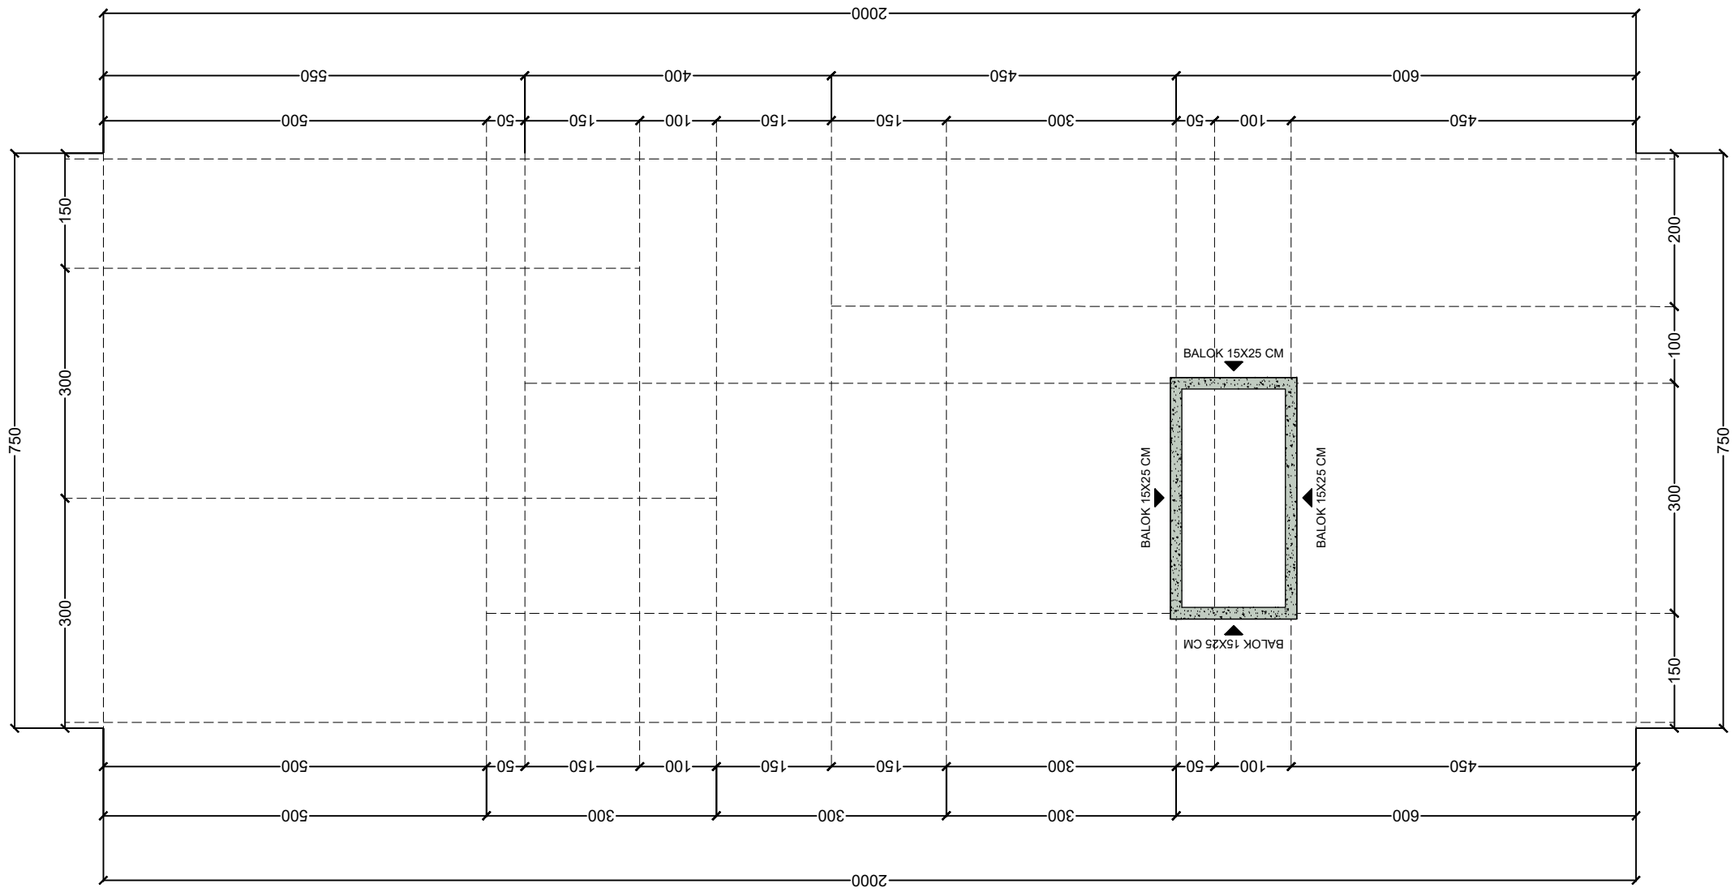

CODE
STR

DENAH BALOK ELEVASI + 3.00

SKALA 1 : 80

GEOMETRI BALOK B1		
DIMENSI	15 x 25	
TUL. ATAS	2 Ø 12	2 Ø 12
TUL.TENGAH	-	-
TUL. BAWAH	2 Ø 12	2 Ø 12
JARAK BEUGEL	¼ H	½ H
	Ø8 - 10	Ø8 - 15

ARCHILLES STUDIO

KETERANGAN :

PROJECT :

PERENCANAAN RUMAH HUNIAN
TYPE 65

LOKASI :

BANTARAN NILA, LAMPUNG

OWNER :


.....

PERENCANA :

ARCHILLES TEAM

JUDUL GAMBAR	SKALA

TOTAL HALAMAN	CODE	NO HALAMAN

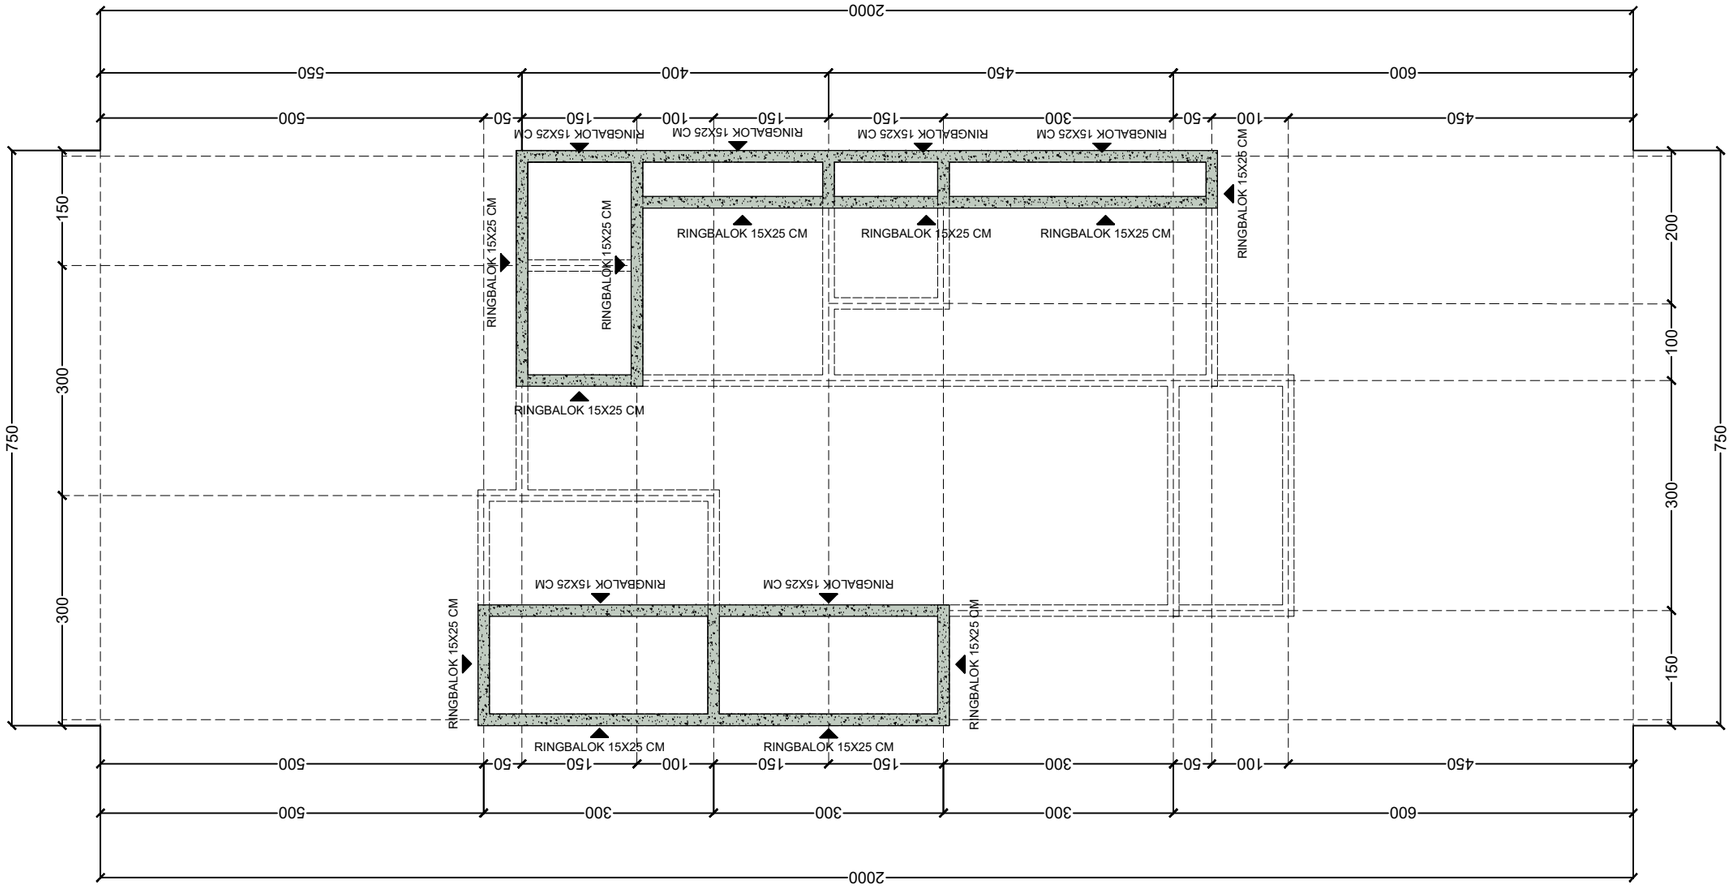

CODE
STR

DENAH RING BALOK ELEVASI + 3.50

SKALA 1 : 80

GEOMETRI RING BALOK RB1		
DIMENSI	15 x 25	
TUL. ATAS	2 Ø 12	2 Ø 12
TUL.TENGAH	-	-
TUL. BAWAH	2 Ø 12	2 Ø 12
JARAK BEUGEL	¼ H	½ H
	Ø8 - 10	Ø8 - 20

ARCHILLES STUDIO

KETERANGAN :

PROJECT :

PERENCANAAN RUMAH HUNIAN
TYPE 65

LOKASI :

BANTARAN NILA, LAMPUNG

OWNER :


.....


PERENCANA :

ARCHILLES TEAM

JUDUL GAMBAR	SKALA

TOTAL HALAMAN	CODE	NO HALAMAN

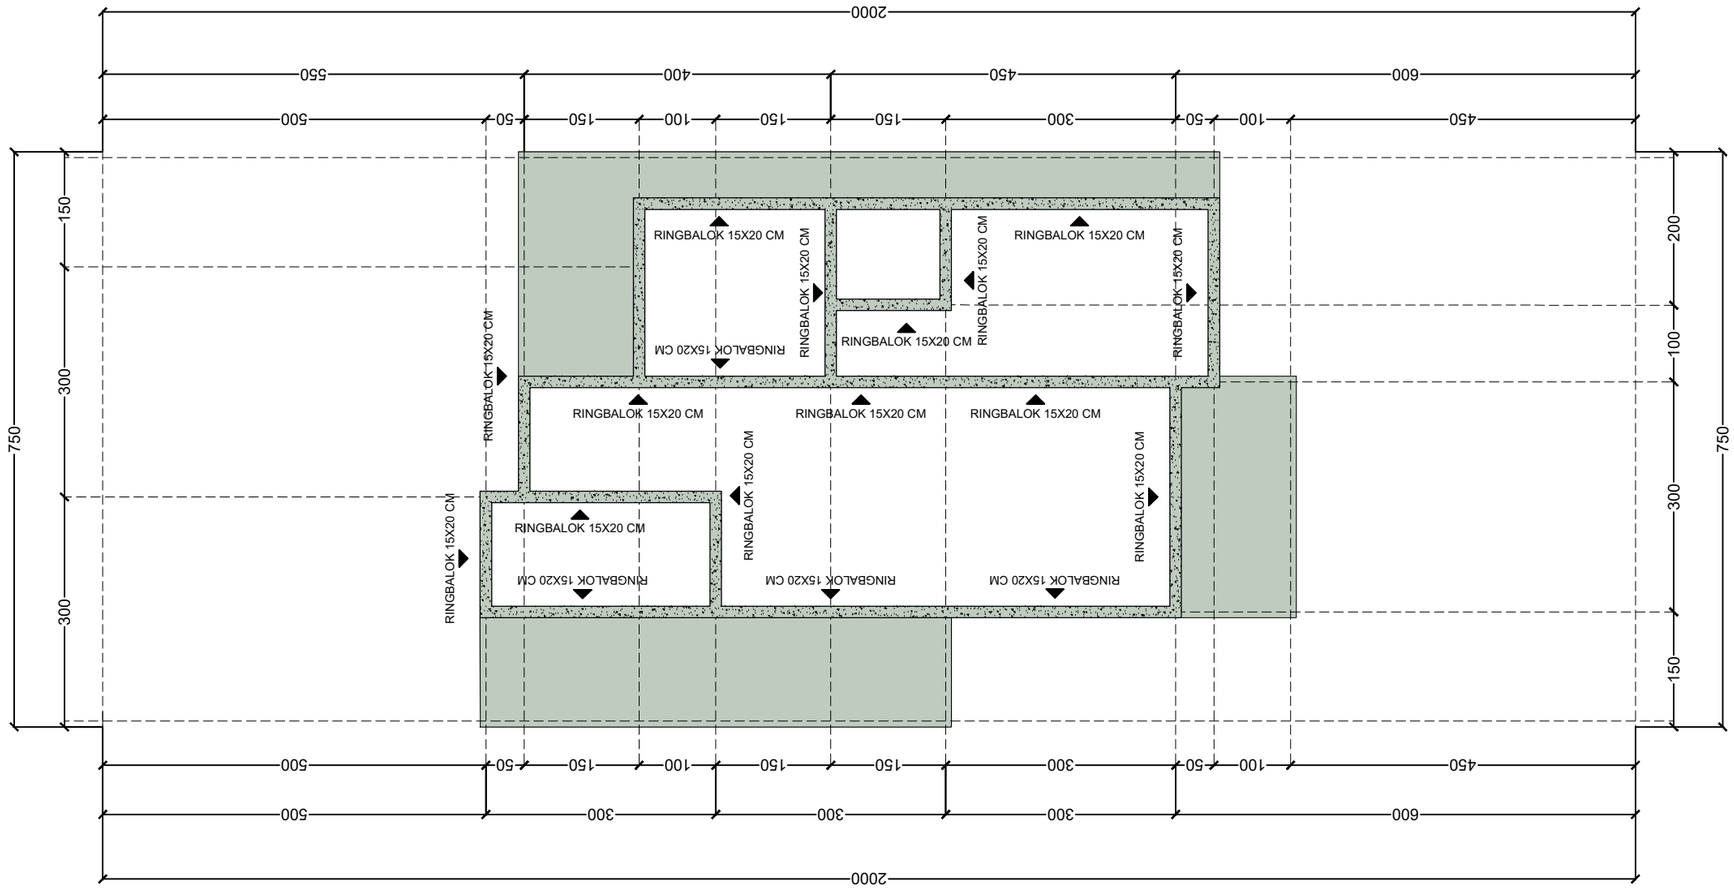
2000
550
400
450
600
500
50
150
100
150
150
300
50
100
450
750
150
300
300
150
RINGBALOK 15X20 CM
RINGBALOK 15X20 CM
RINGBALOK 15X20 CM

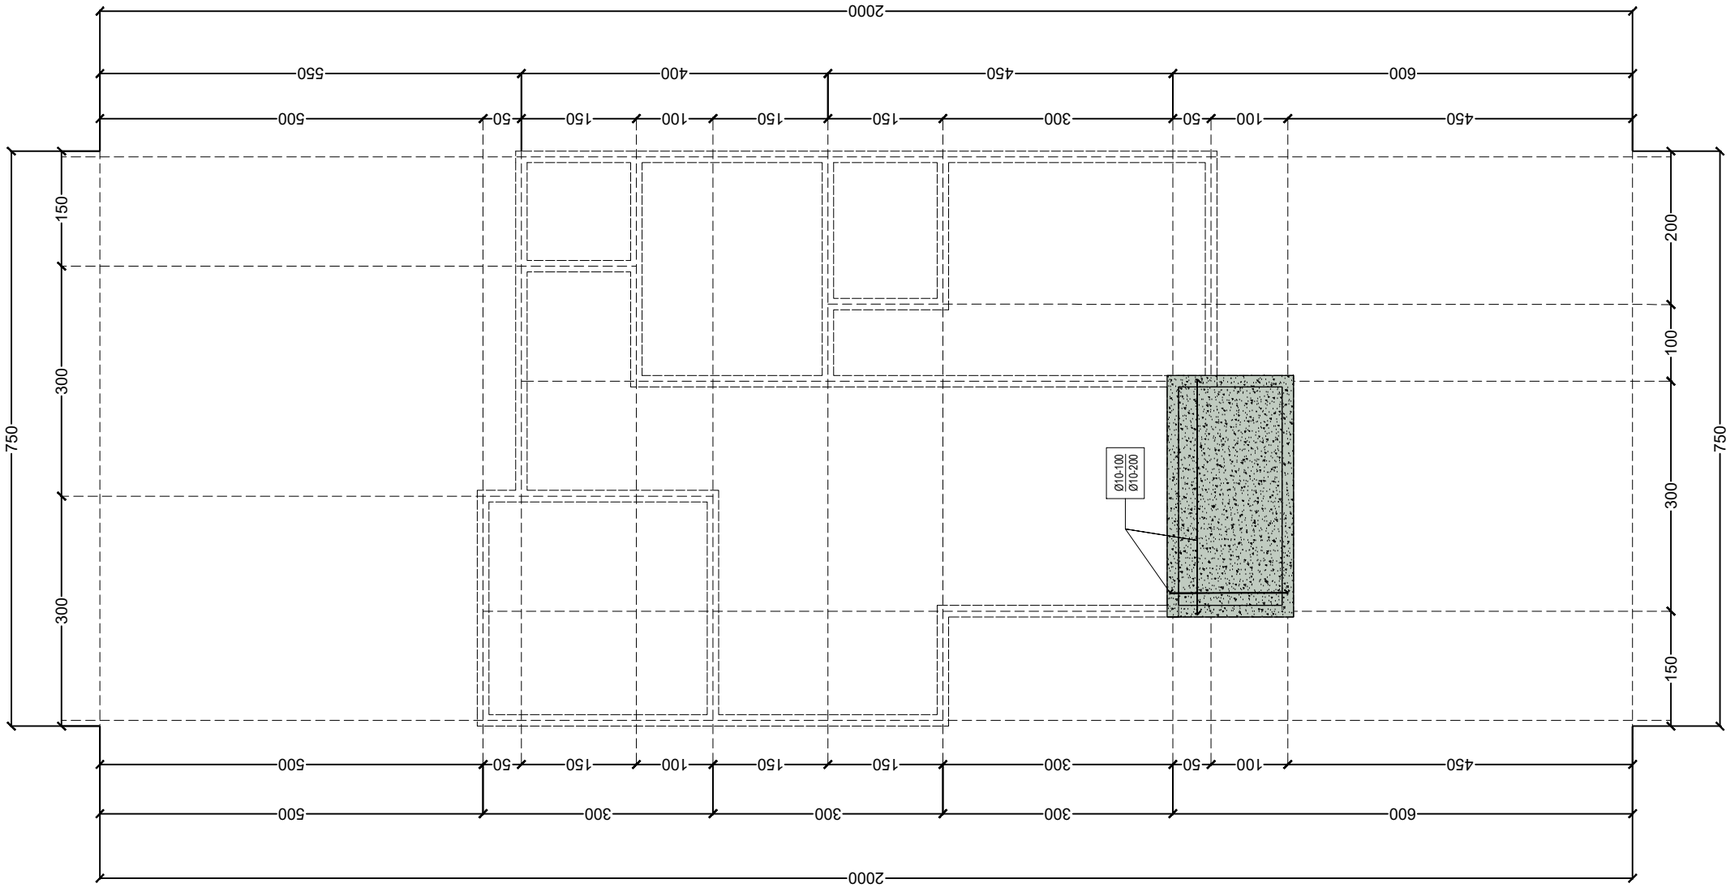

CODE
STR

DENAH DAK BETON ELEVASI +3.00

SKALA 1 : 80

ARCHILLES STUDIO

KETERANGAN :

PROJECT :

PERENCANAAN RUMAH HUNIAN
TYPE 65

LOKASI :

BANTARAN NILA, LAMPUNG

OWNER :


.....

PERENCANA :

ARCHILLES TEAM

JUDUL GAMBAR	SKALA

TOTAL HALAMAN	CODE	NO HALAMAN

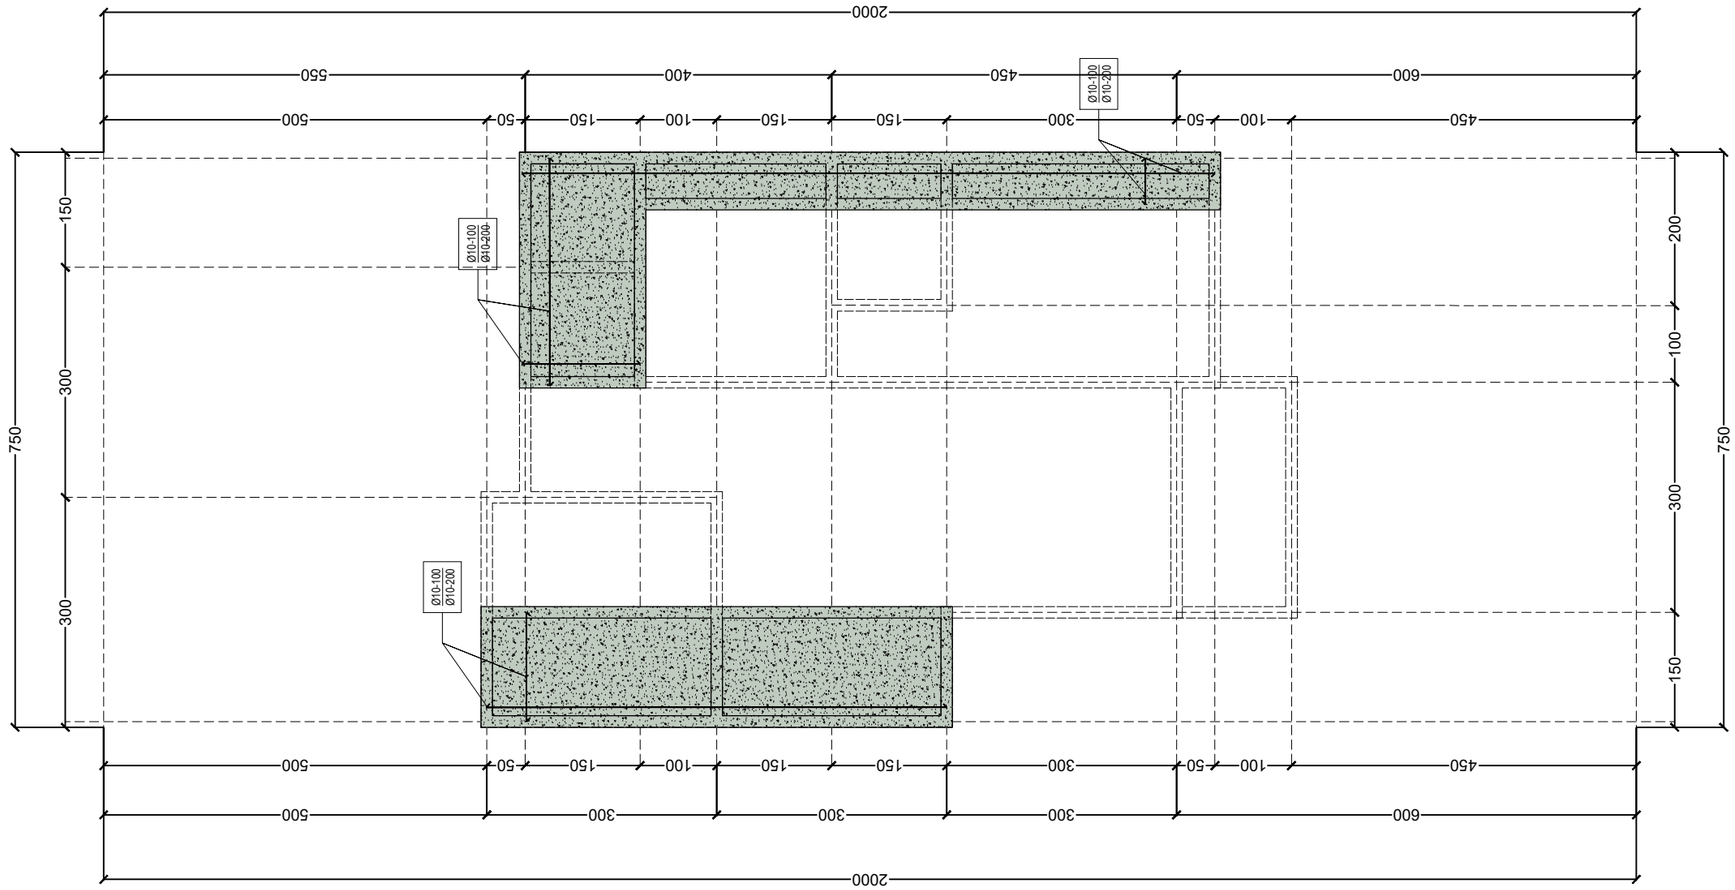

CODE
STR

DENAH DAK BETON ELEVASI +3.50

SKALA 1 : 80

ARCHILLES STUDIO

KETERANGAN :

PROJECT :

PERENCANAAN RUMAH HUNIAN
TYPE 65

LOKASI :

BANTARAN NILA, LAMPUNG

OWNER :


.....

PERENCANA :

ARCHILLES TEAM

JUDUL GAMBAR	SKALA

TOTAL HALAMAN	CODE	NO HALAMAN

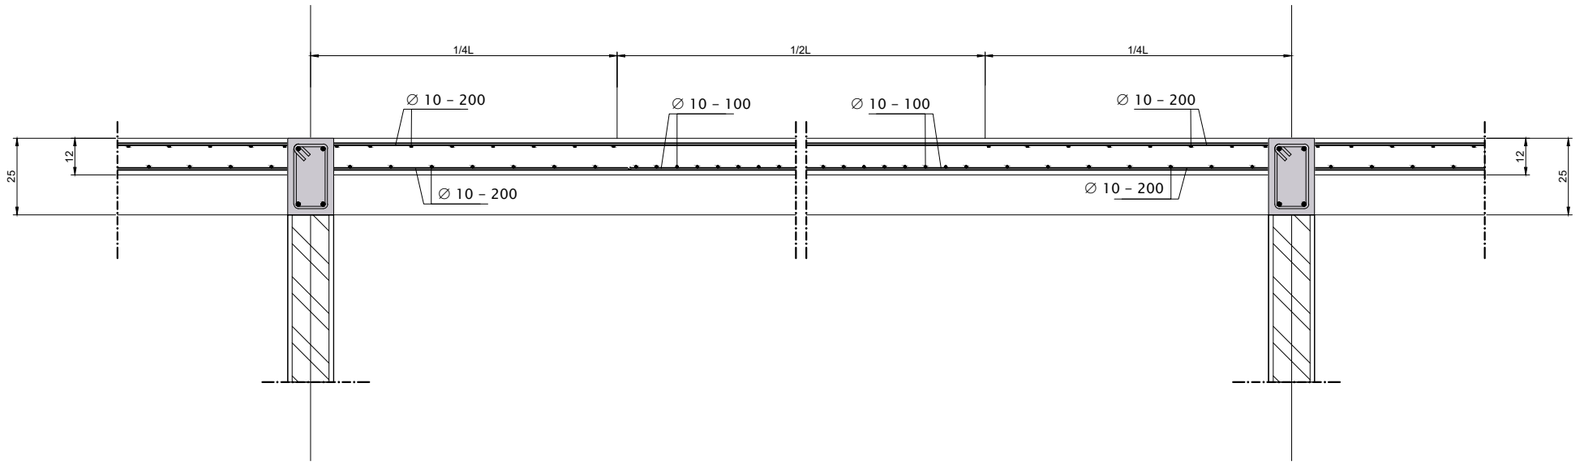

CODE
STR

DETAIL POTONGAN DAK

SKALA 1 : 20

ARCHILLES STUDIO

KETERANGAN :

PROJECT :

PERENCANAAN RUMAH HUNIAN
TYPE 65

LOKASI :

BANTARAN NILA, LAMPUNG

OWNER :

.....

PERENCANA :

ARCHILLES TEAM


JUDUL GAMBAR	SKALA

TOTAL HALAMAN	CODE	NO HALAMAN

ARCHILLES
STUDIO

MECHANICAL, ELECTRICAL, AND PLUMBING

CODE :
MEP

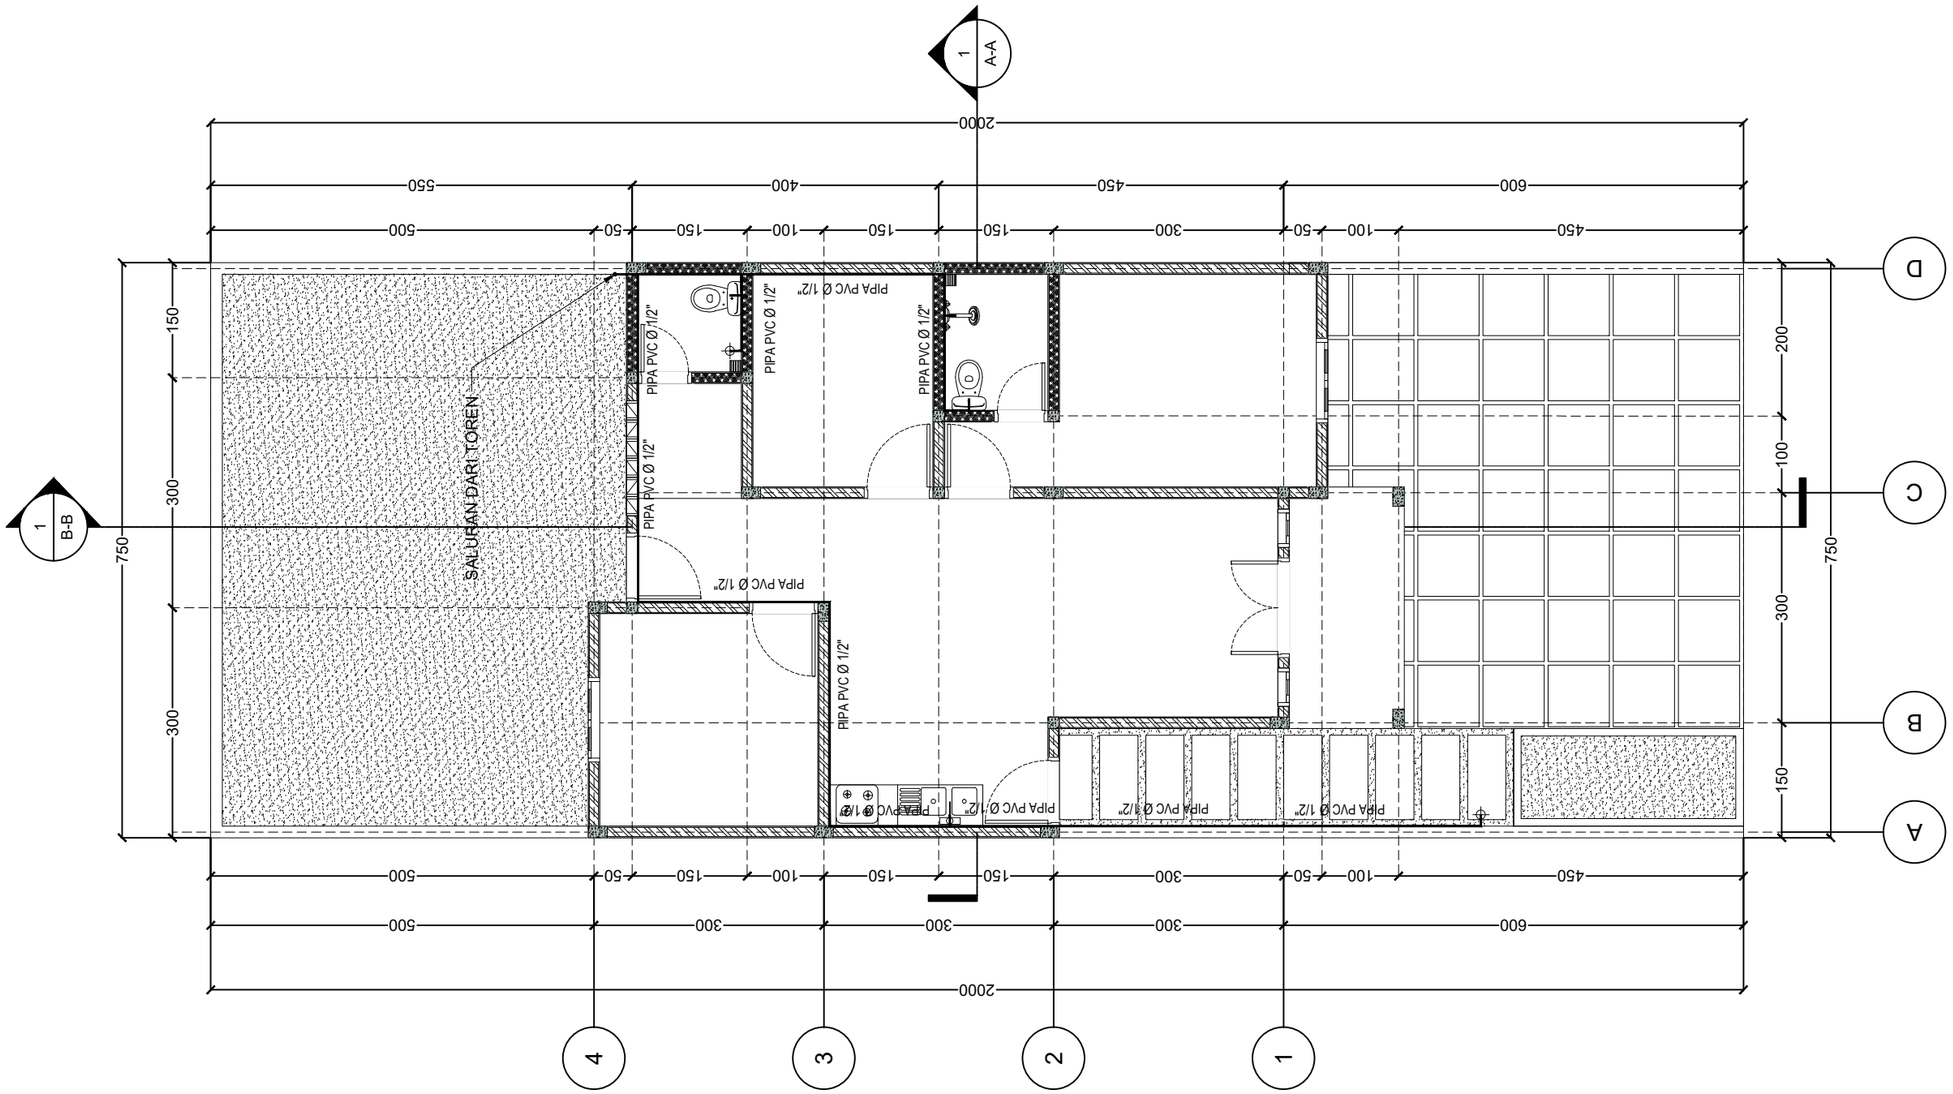

CODE
MEP

DENAH SANITASI AIR BERSIH

SKALA 1 : 80

ARCHILLES STUDIO

KETERANGAN :

PROJECT :

PERENCANAAN RUMAH HUNIAN
TYPE 65

LOKASI :

BANTARAN NILA, LAMPUNG

OWNER :


.....

PERENCANA :

ARCHILLES TEAM

JUDUL GAMBAR	SKALA

TOTAL HALAMAN	CODE	NO HALAMAN

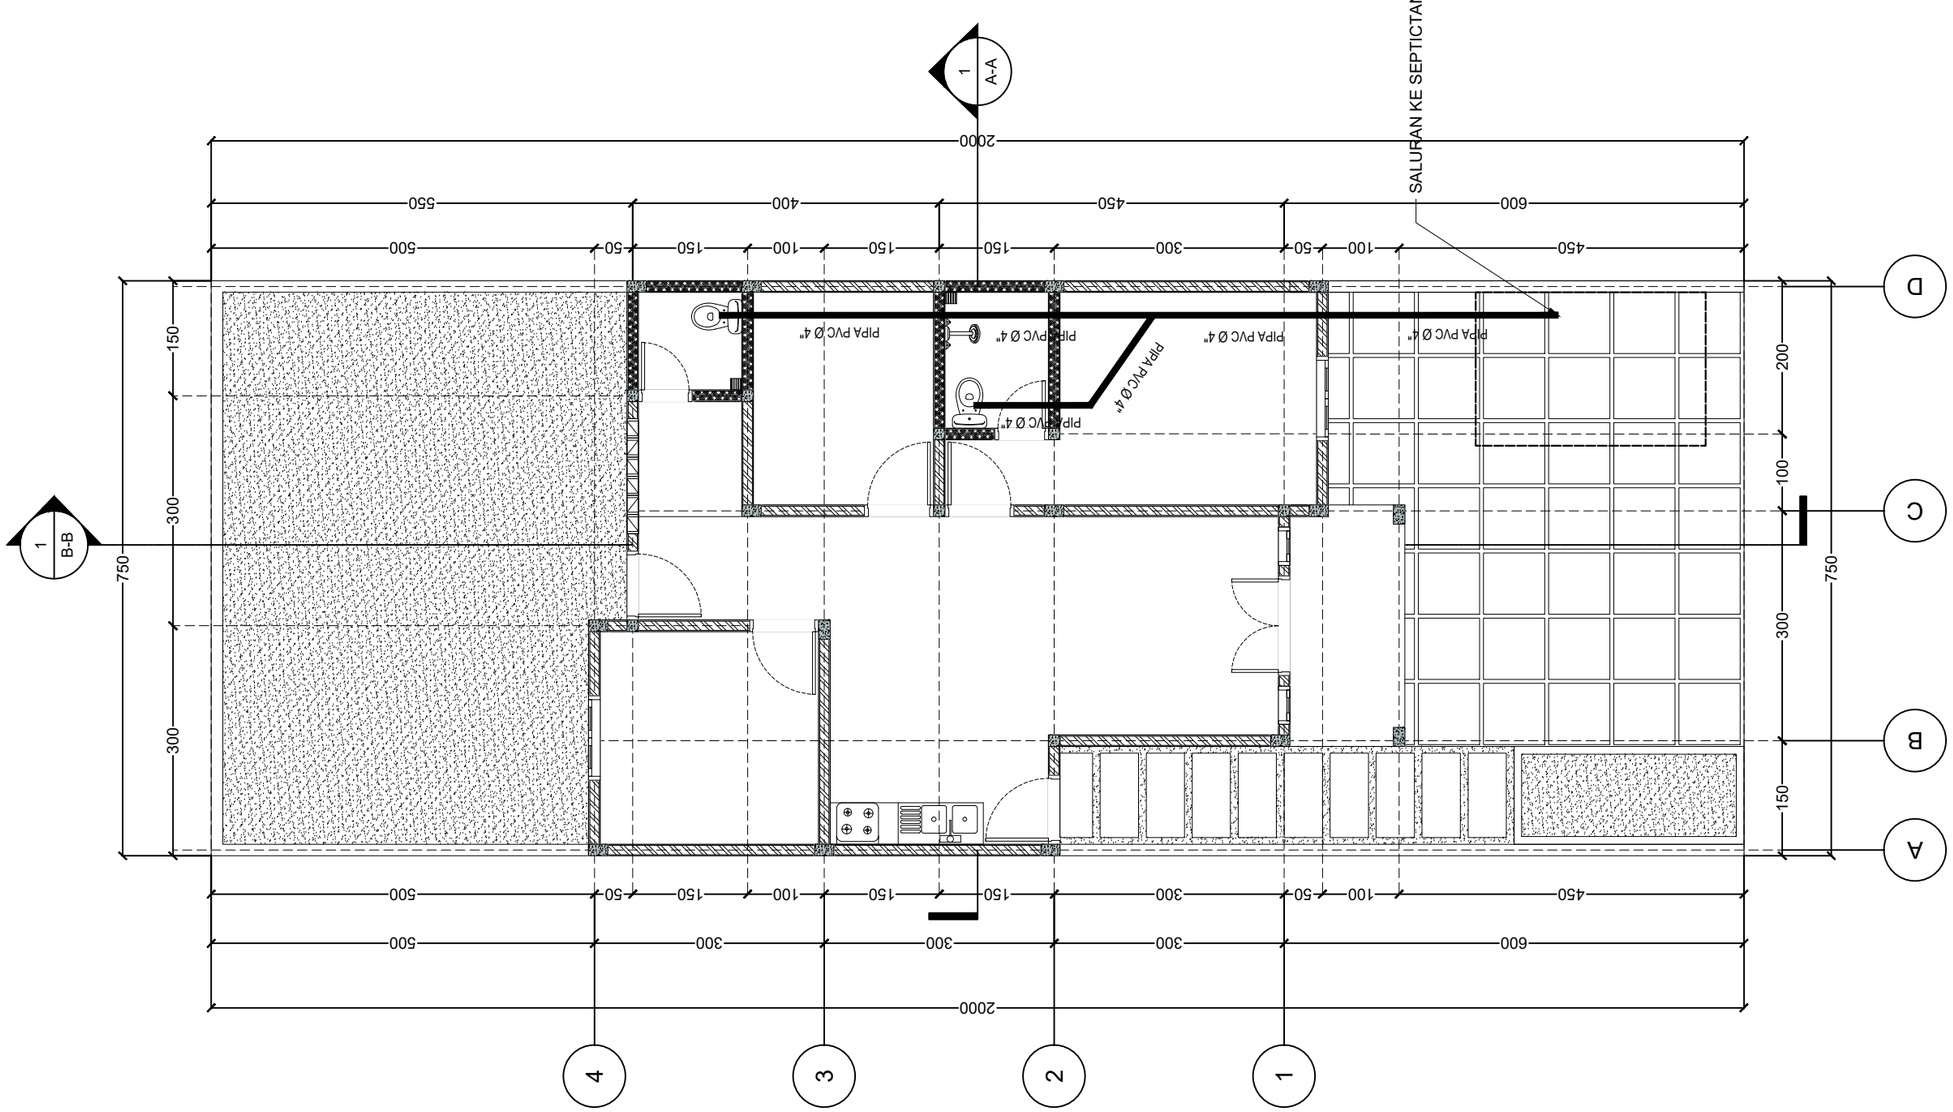

CODE
MEP

DENAH SANITASI PEMBUANGAN TINJA

SKALA 1 : 80

ARCHILLES STUDIO

KETERANGAN :

PROJECT :

PERENCANAAN RUMAH HUNIAN
TYPE 65

LOKASI :

BANTARAN NILA, LAMPUNG

OWNER :


.....

PERENCANA :

ARCHILLES TEAM

JUDUL GAMBAR	SKALA

TOTAL HALAMAN	CODE	NO HALAMAN

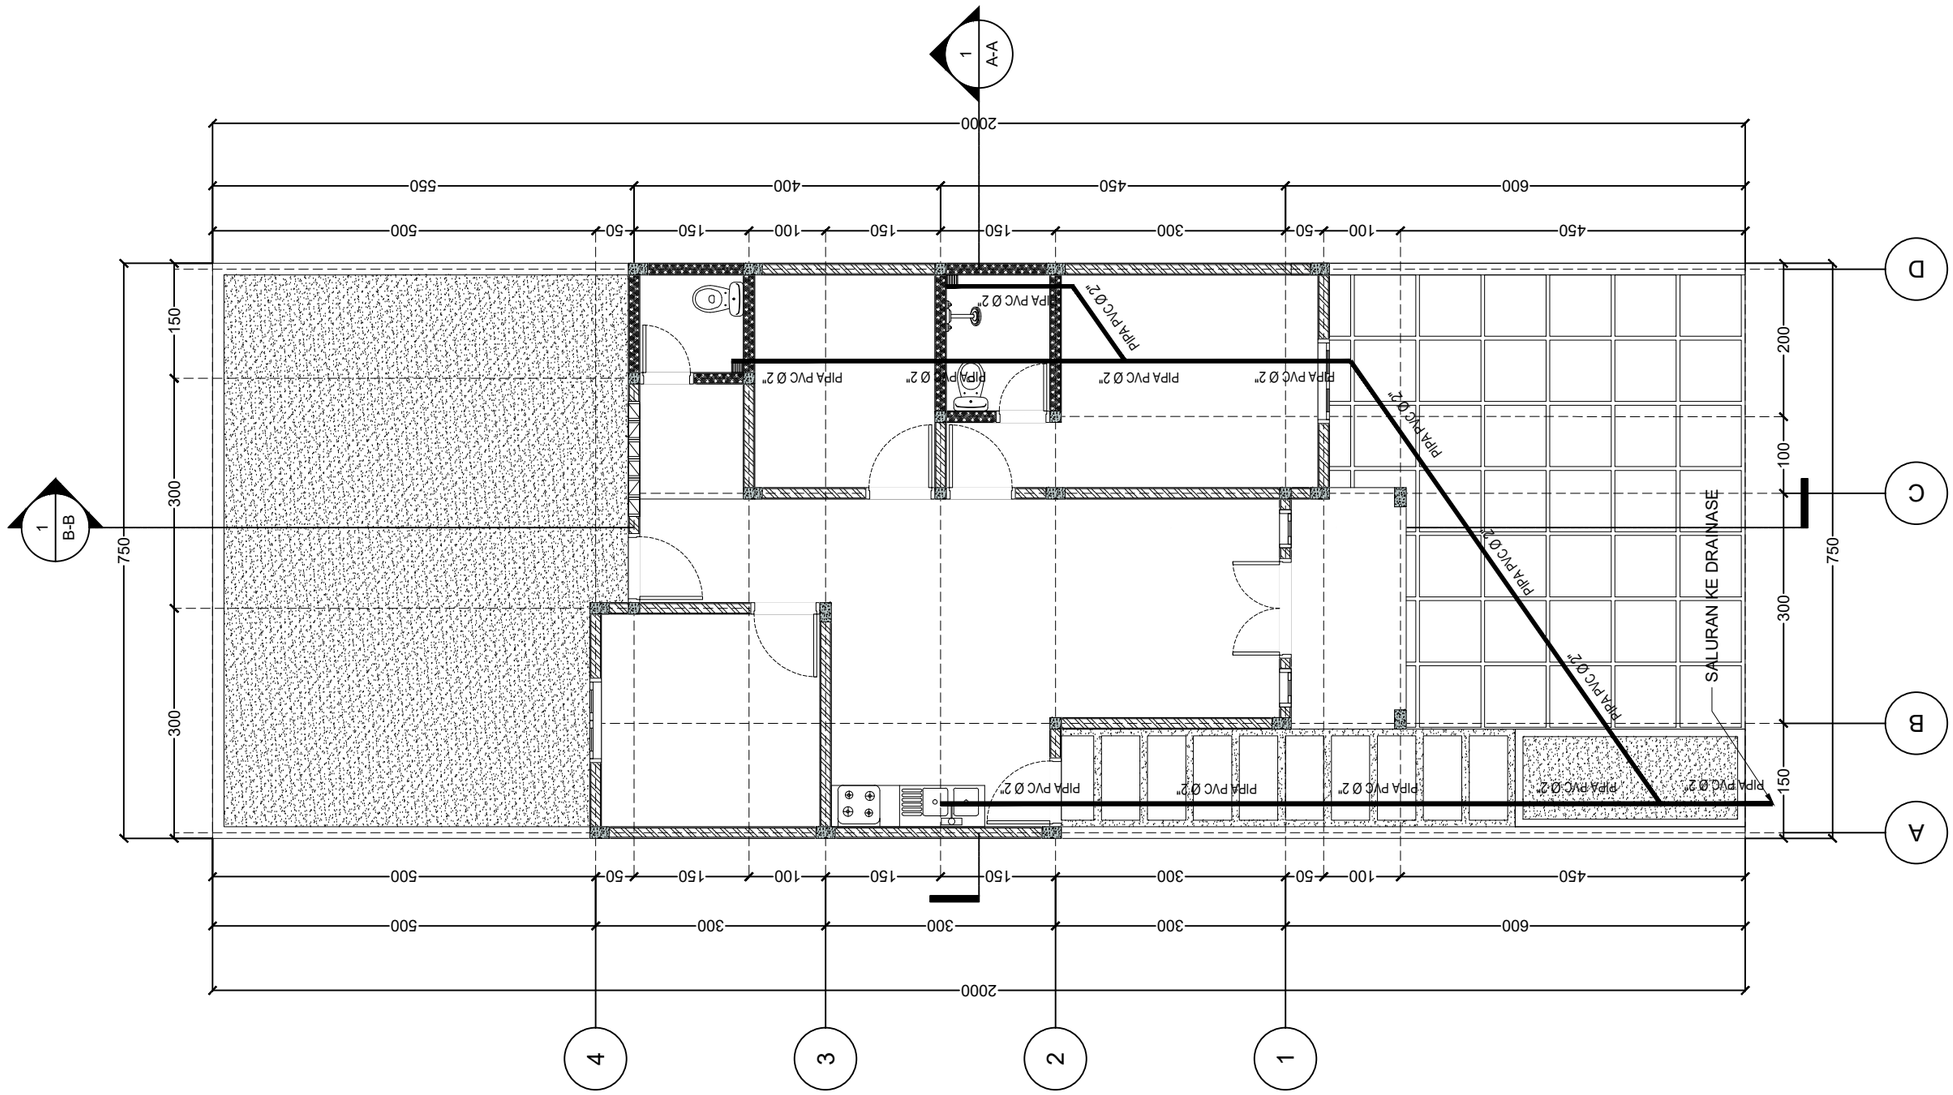

CODE
MEP

DENAH SANITASI AIR KOTOR

SKALA 1 : 80

ARCHILLES STUDIO

KETERANGAN :

PROJECT :

PERENCANAAN RUMAH HUNIAN
TYPE 65

LOKASI :

BANTARAN NILA, LAMPUNG

OWNER :


.....

PERENCANA :

ARCHILLES TEAM


JUDUL GAMBAR	SKALA

TOTAL HALAMAN	CODE	NO HALAMAN

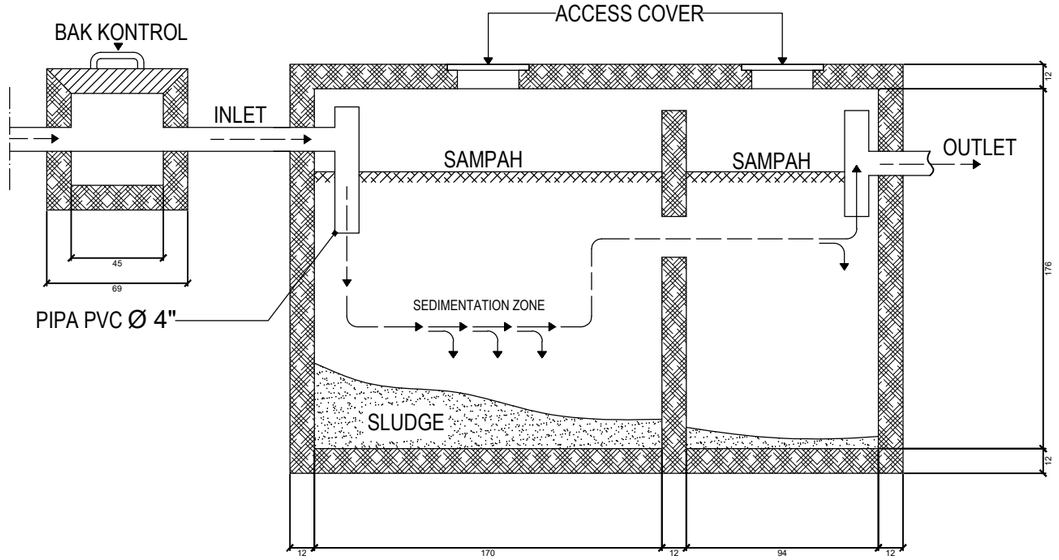


CODE MEP — POTONGAN A-A SEPTICTANK

SKALA 1 : 30

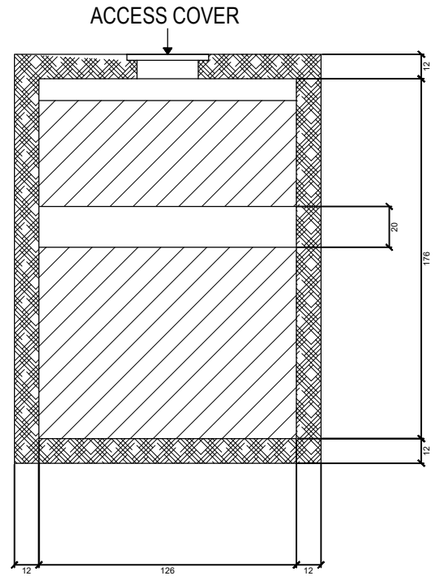

CODE MEP — POTONGAN B-B SEPTICTANK

SKALA 1 : 30

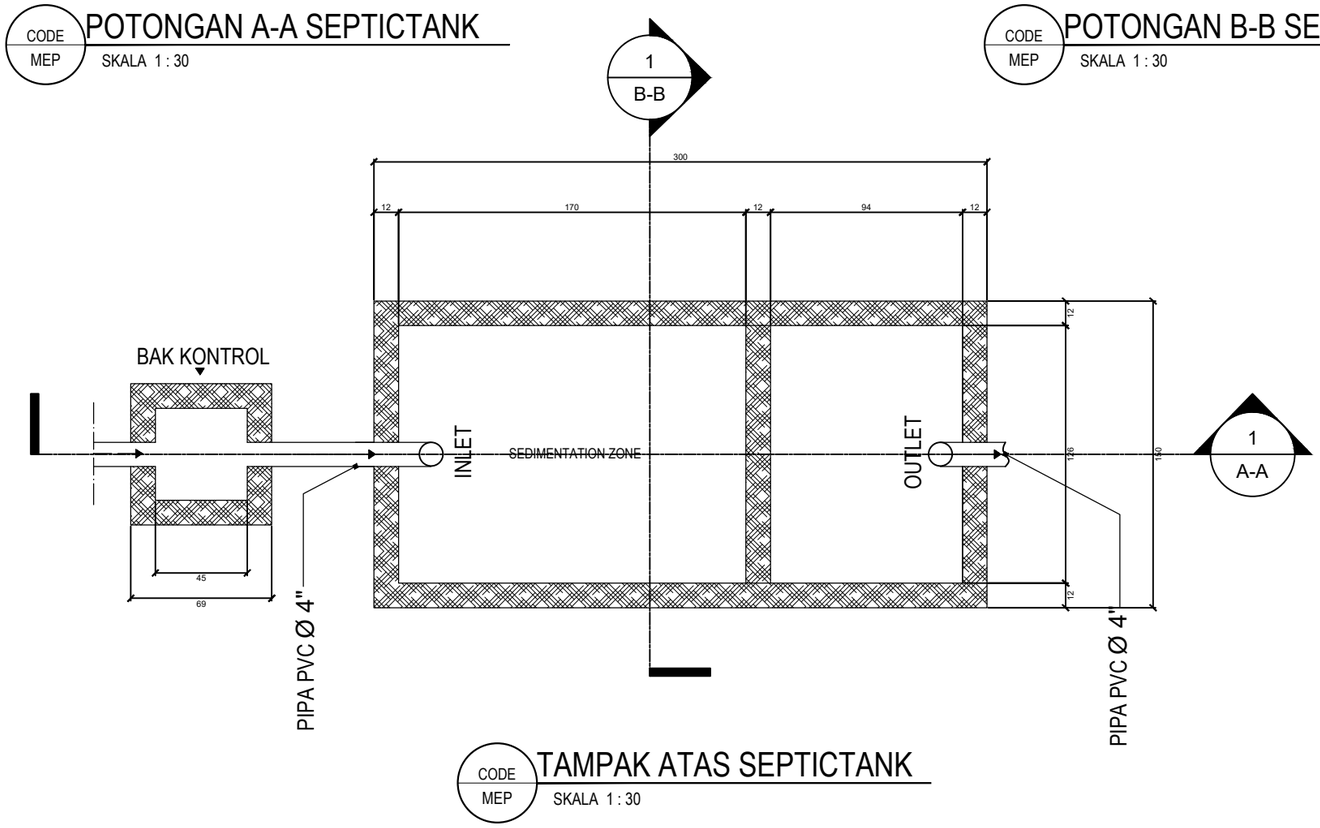

CODE MEP — TAMPAK ATAS SEPTICTANK

SKALA 1 : 30

ARCHILLES STUDIO

KETERANGAN :

PROJECT :

PERENCANAAN RUMAH HUNIAN
TYPE 65

LOKASI :

BANTARAN NILA, LAMPUNG

OWNER :


.....

PERENCANA :

ARCHILLES TEAM

JUDUL GAMBAR	SKALA

TOTAL HALAMAN	CODE	NO HALAMAN

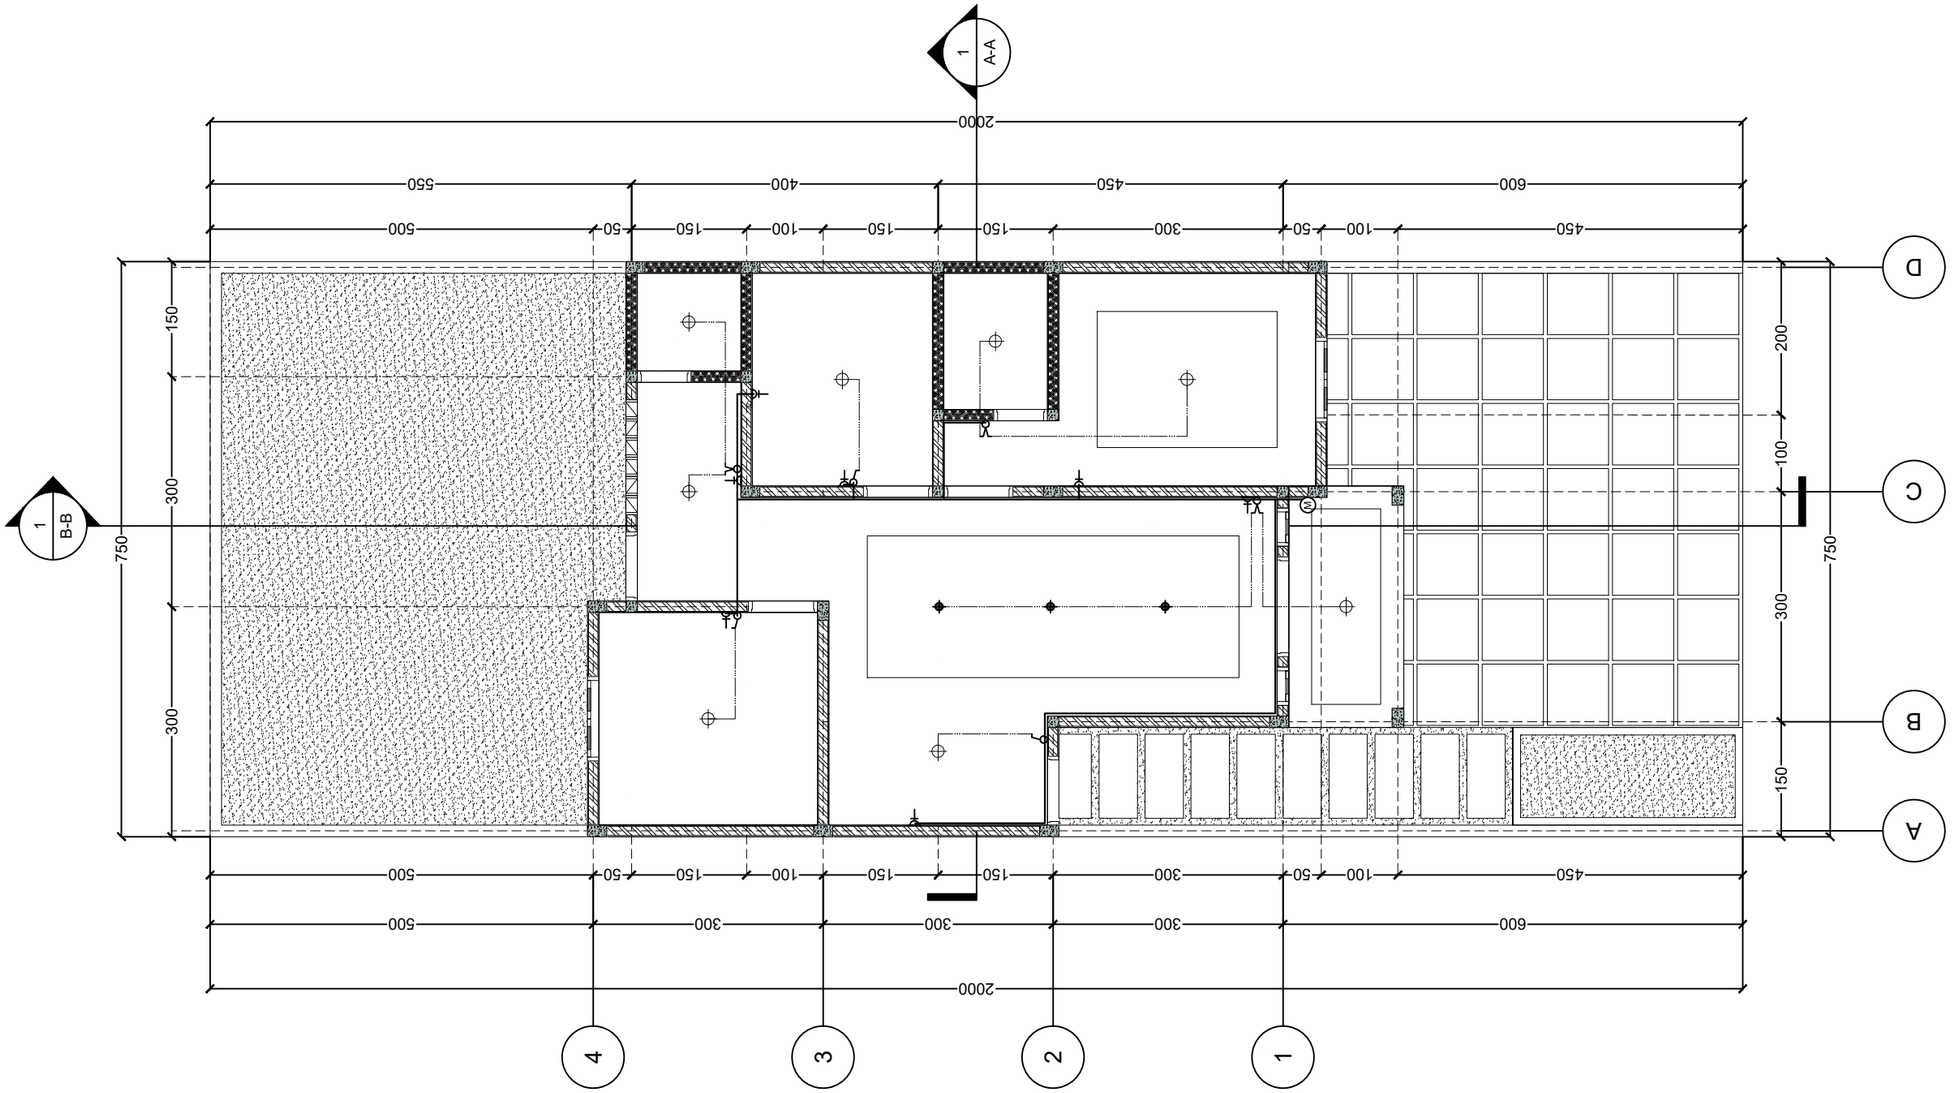

NO	SIMBOL	JML	KETERANGAN
1		8	LAMPU 40 WATT
2		3	SAKLAR TUNGGAL ELEV + 1.50
3		3	SAKLAR DOUBLE ELEV + 1.50
4		6	STOP KONTAK ELEV + 1.50
5		1	STOP KONTAK AC ELEV + 2.80
5	M	1	METERAN LISTRIK DAN MCB
6		3	LAMPU DOWN LIGHT

CODE
MEP

DENAH INSTALASI LISTRIK

SKALA 1 : 80

ARCHILLES STUDIO

KETERANGAN :

PROJECT :

PERENCANAAN RUMAH HUNIAN
TYPE 65

LOKASI :

BANTARAN NILA, LAMPUNG

OWNER :

.....

PERENCANA :

ARCHILLES TEAM

JUDUL GAMBAR	SKALA

TOTAL HALAMAN	CODE	NO HALAMAN

ARCHILLES
STUDIO

Instagram : archilles_studio