September 2026

Project

Perencanaan Rumah Hunian
satu lantai
Alamat : Pramuka.

ARCHILLES
STUDIO

DED


(Detail Engineering Design)

ARCHILLES
STUDIO

ARSITEKTUR

CODE :

ARS

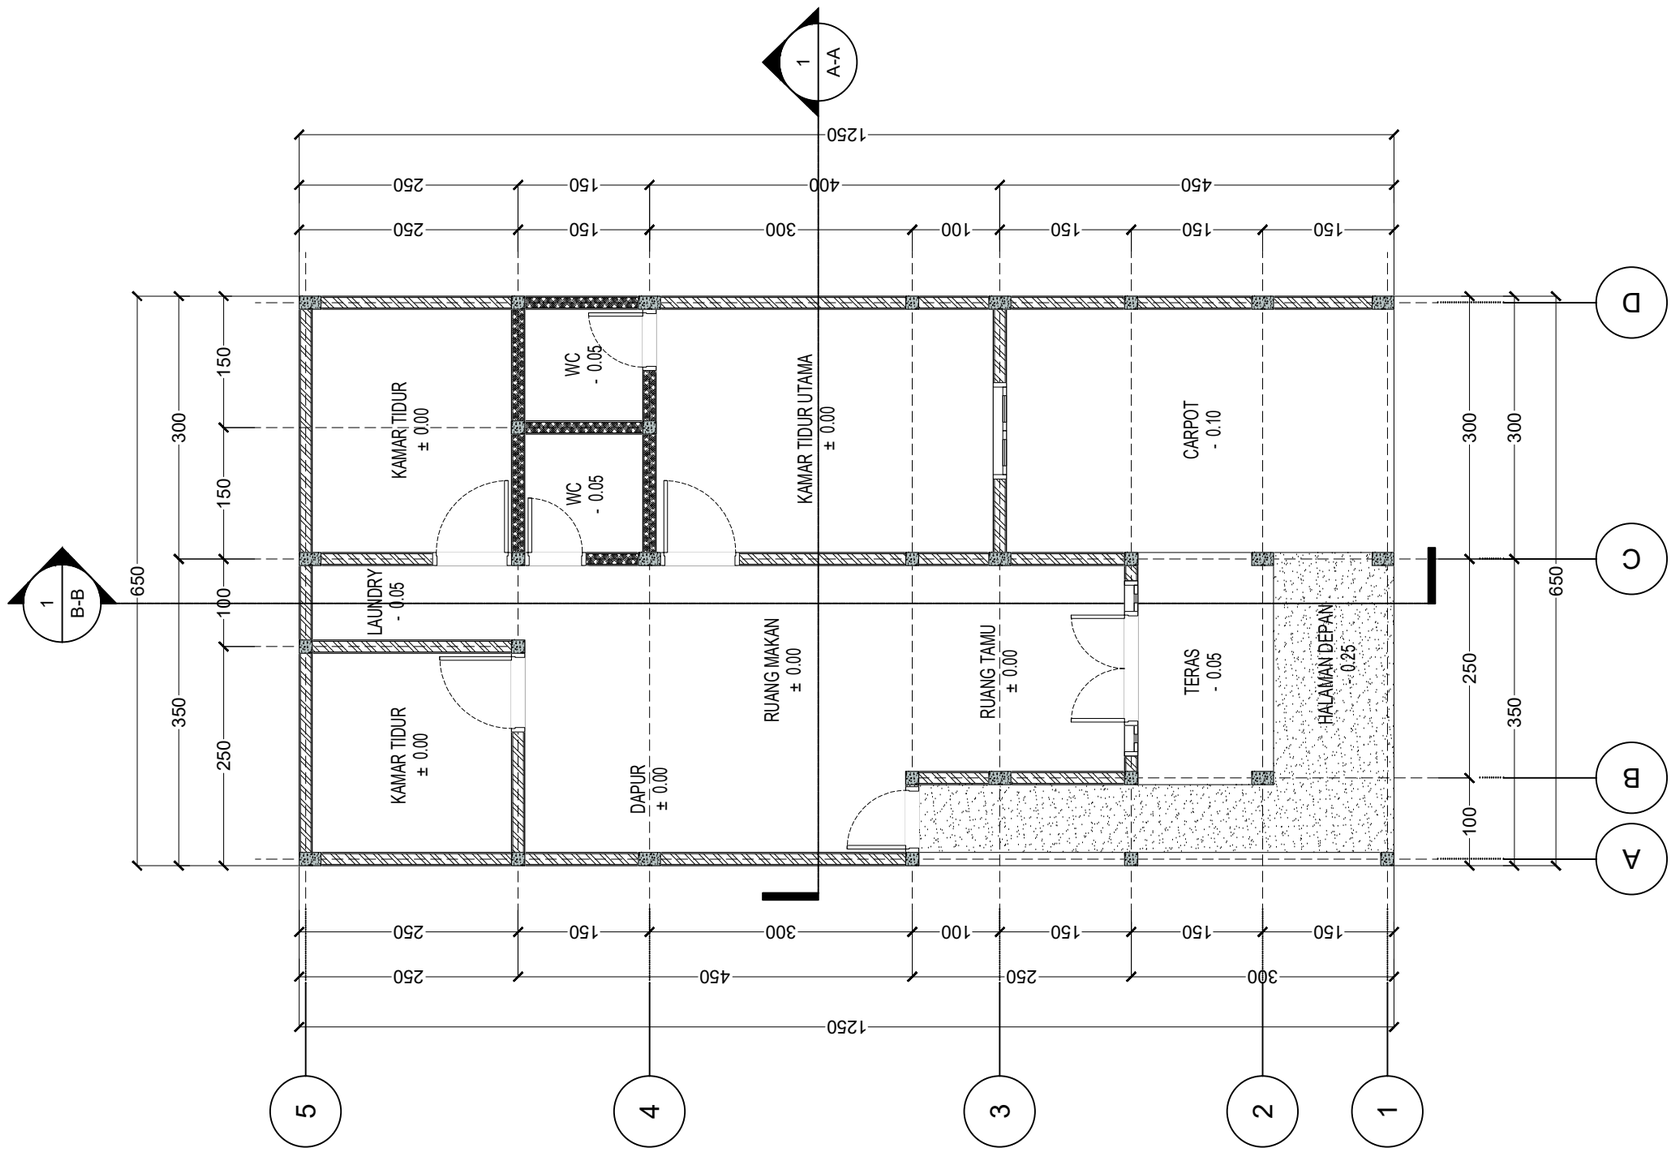

CODE
ARS

DENAH

SKALA 1 : 70

ARCHILLES STUDIO

KETERANGAN :

PROJECT :

PERENCANAAN RUMAH HUNIAN

LOKASI :

PRAMUKA

OWNER :


.....

PERENCANA :

ARCHILLES TEAM

JUDUL GAMBAR	SKALA

TOTAL HALAMAN	CODE	NO HALAMAN

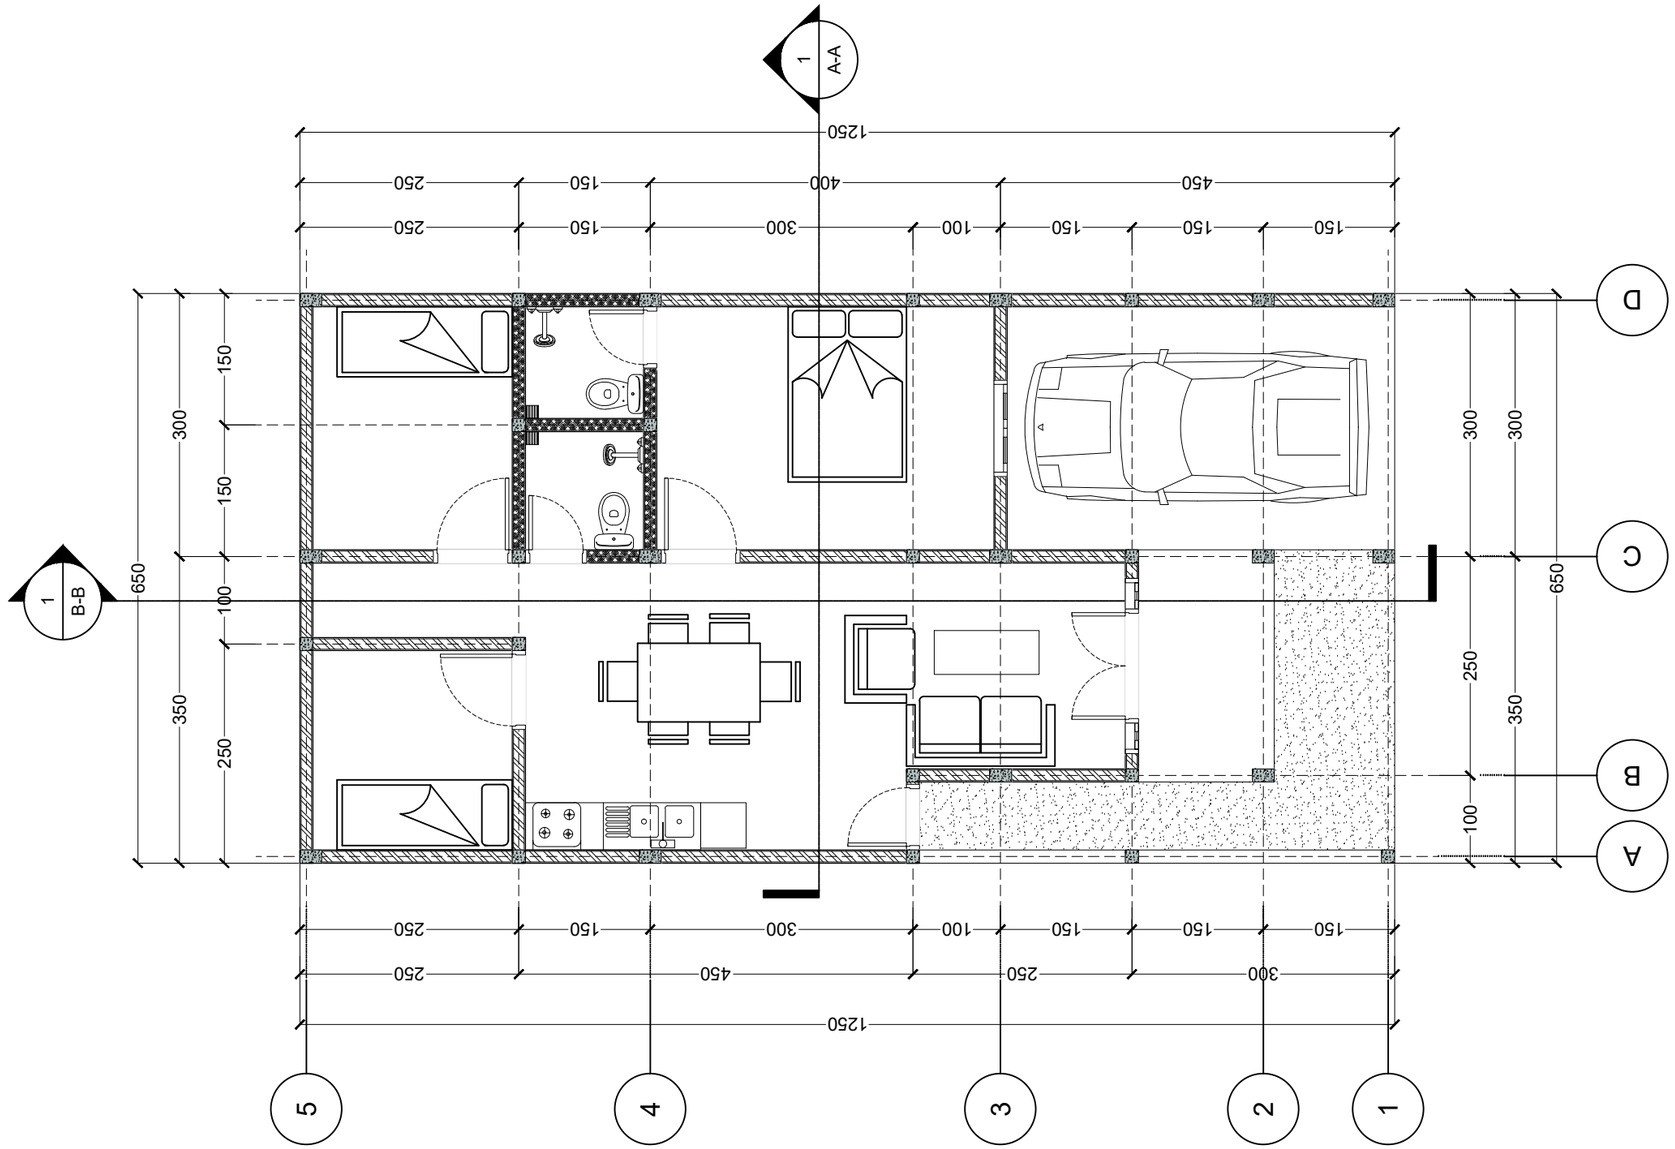

CODE
ARS

DENAH LAYOUT

SKALA 1 : 70

ARCHILLES STUDIO

KETERANGAN :

PROJECT :

PERENCANAAN RUMAH HUNIAN

LOKASI :

PRAMUKA

OWNER :

.....

PERENCANA :

ARCHILLES TEAM

JUDUL GAMBAR	SKALA


TOTAL HALAMAN	CODE	NO HALAMAN



CODE
ARS

TAMPAK DEPAN

SKALA 1 : 70

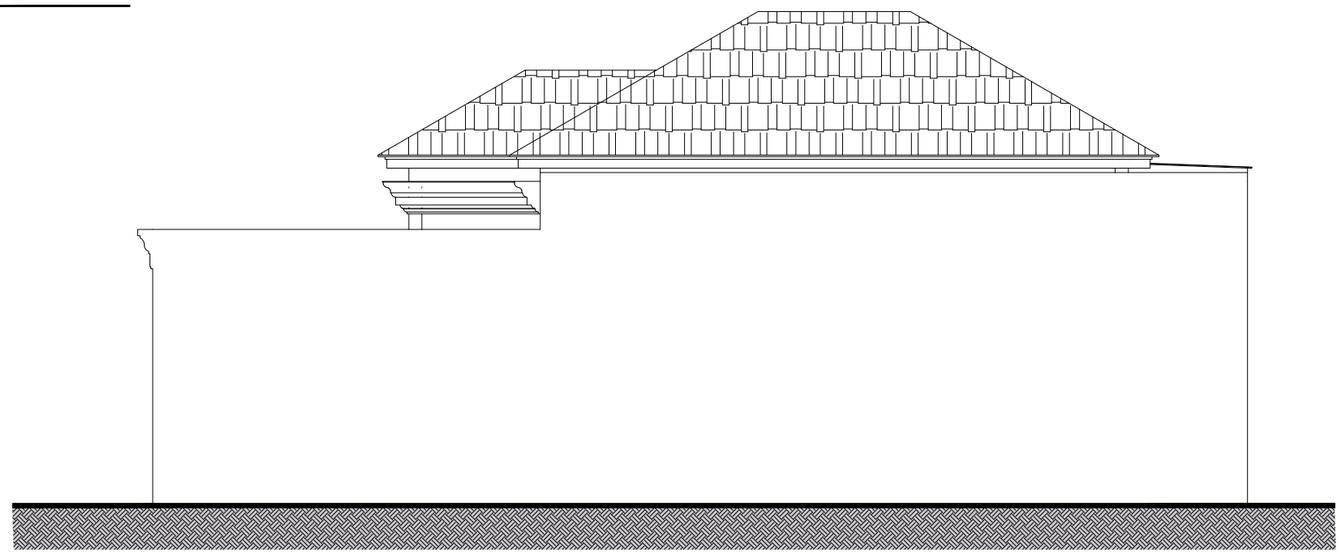

CODE
ARS

TAMPAK SAMPING KANAN

SKALA 1 : 70

ARCHILLES STUDIO

KETERANGAN :

PROJECT :

PERENCANAAN RUMAH HUNIAN

LOKASI :

PRAMUKA

OWNER :


.....

PERENCANA :

ARCHILLES TEAM

JUDUL GAMBAR	SKALA


TOTAL HALAMAN	CODE	NO HALAMAN

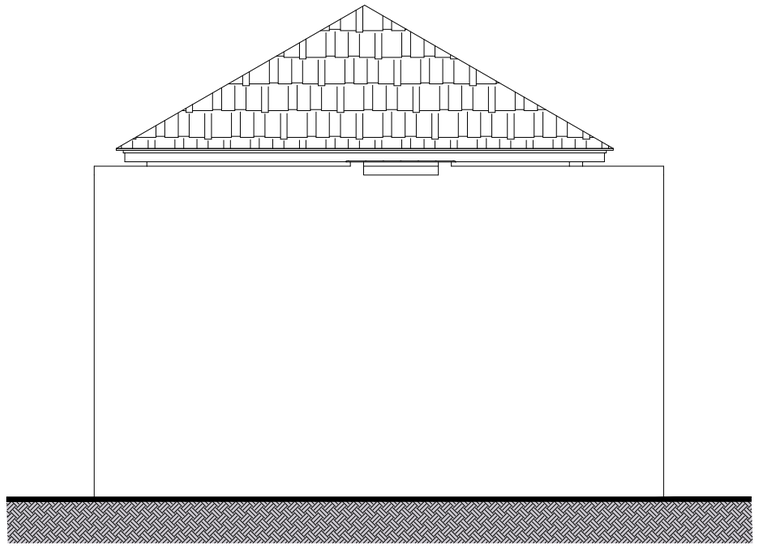

CODE
ARS

TAMPAK BELAKANG

SKALA 1 : 70

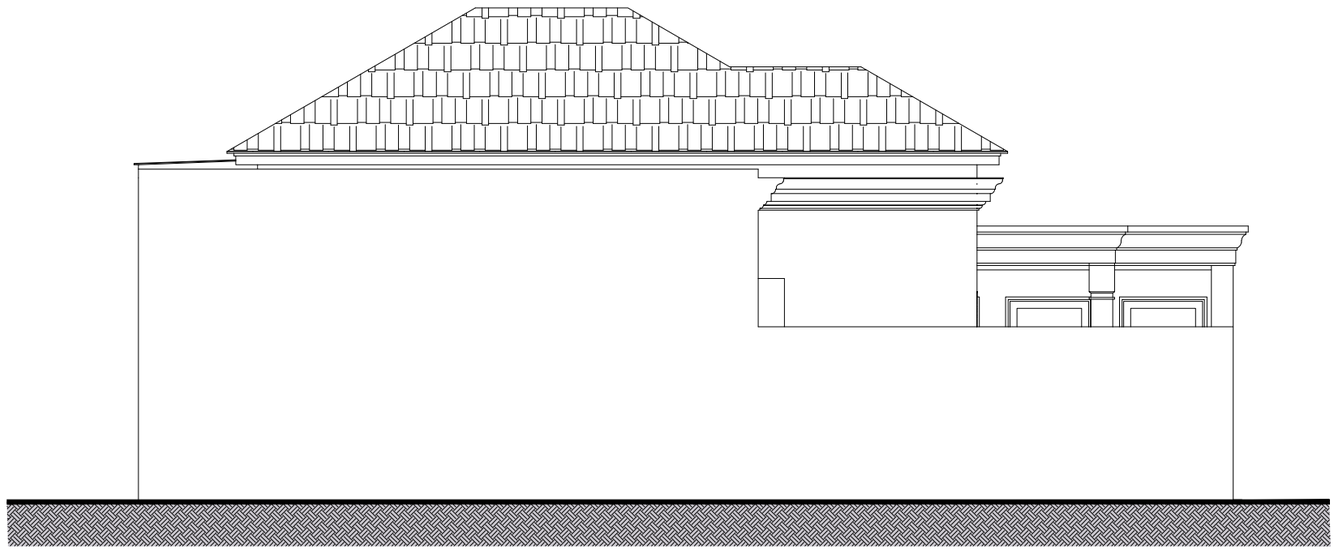

CODE
ARS

TAMPAK SAMPING KIRI

SKALA 1 : 70

ARCHILLES STUDIO

KETERANGAN :

PROJECT :

PERENCANAAN RUMAH HUNIAN

LOKASI :

PRAMUKA

OWNER :


.....

PERENCANA :

ARCHILLES TEAM

JUDUL GAMBAR	SKALA

TOTAL HALAMAN	CODE	NO HALAMAN

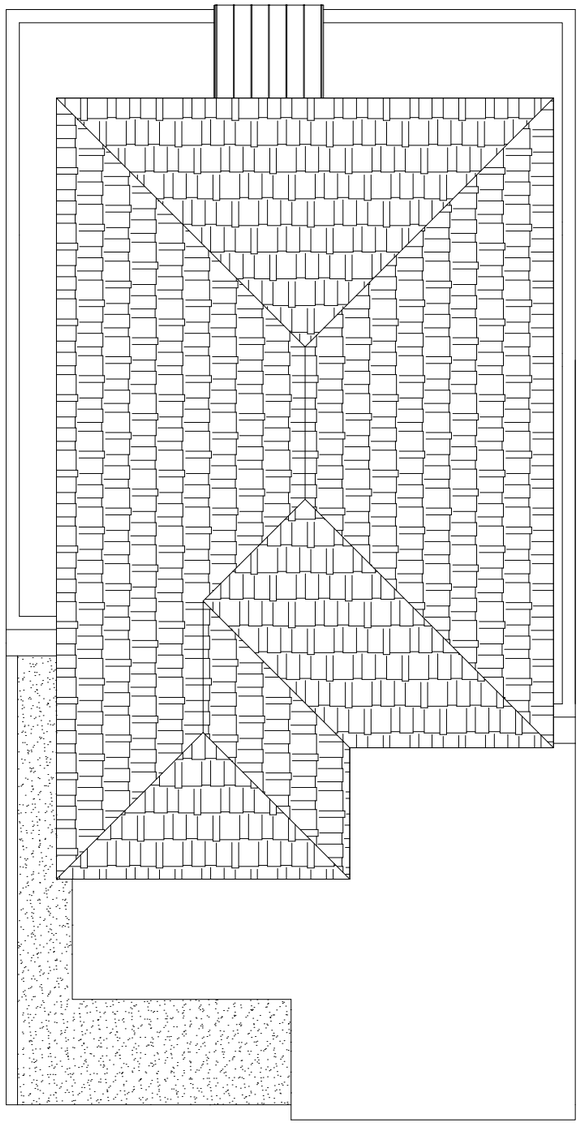

CODE
ARS

TAMPAK ATAS

SKALA 1 : 70

ARCHILLES STUDIO

KETERANGAN :

PROJECT :

PERENCANAAN RUMAH HUNIAN

LOKASI :

PRAMUKA

OWNER :


.....

PERENCANA :

ARCHILLES TEAM

JUDUL GAMBAR	SKALA

TOTAL HALAMAN	CODE	NO HALAMAN

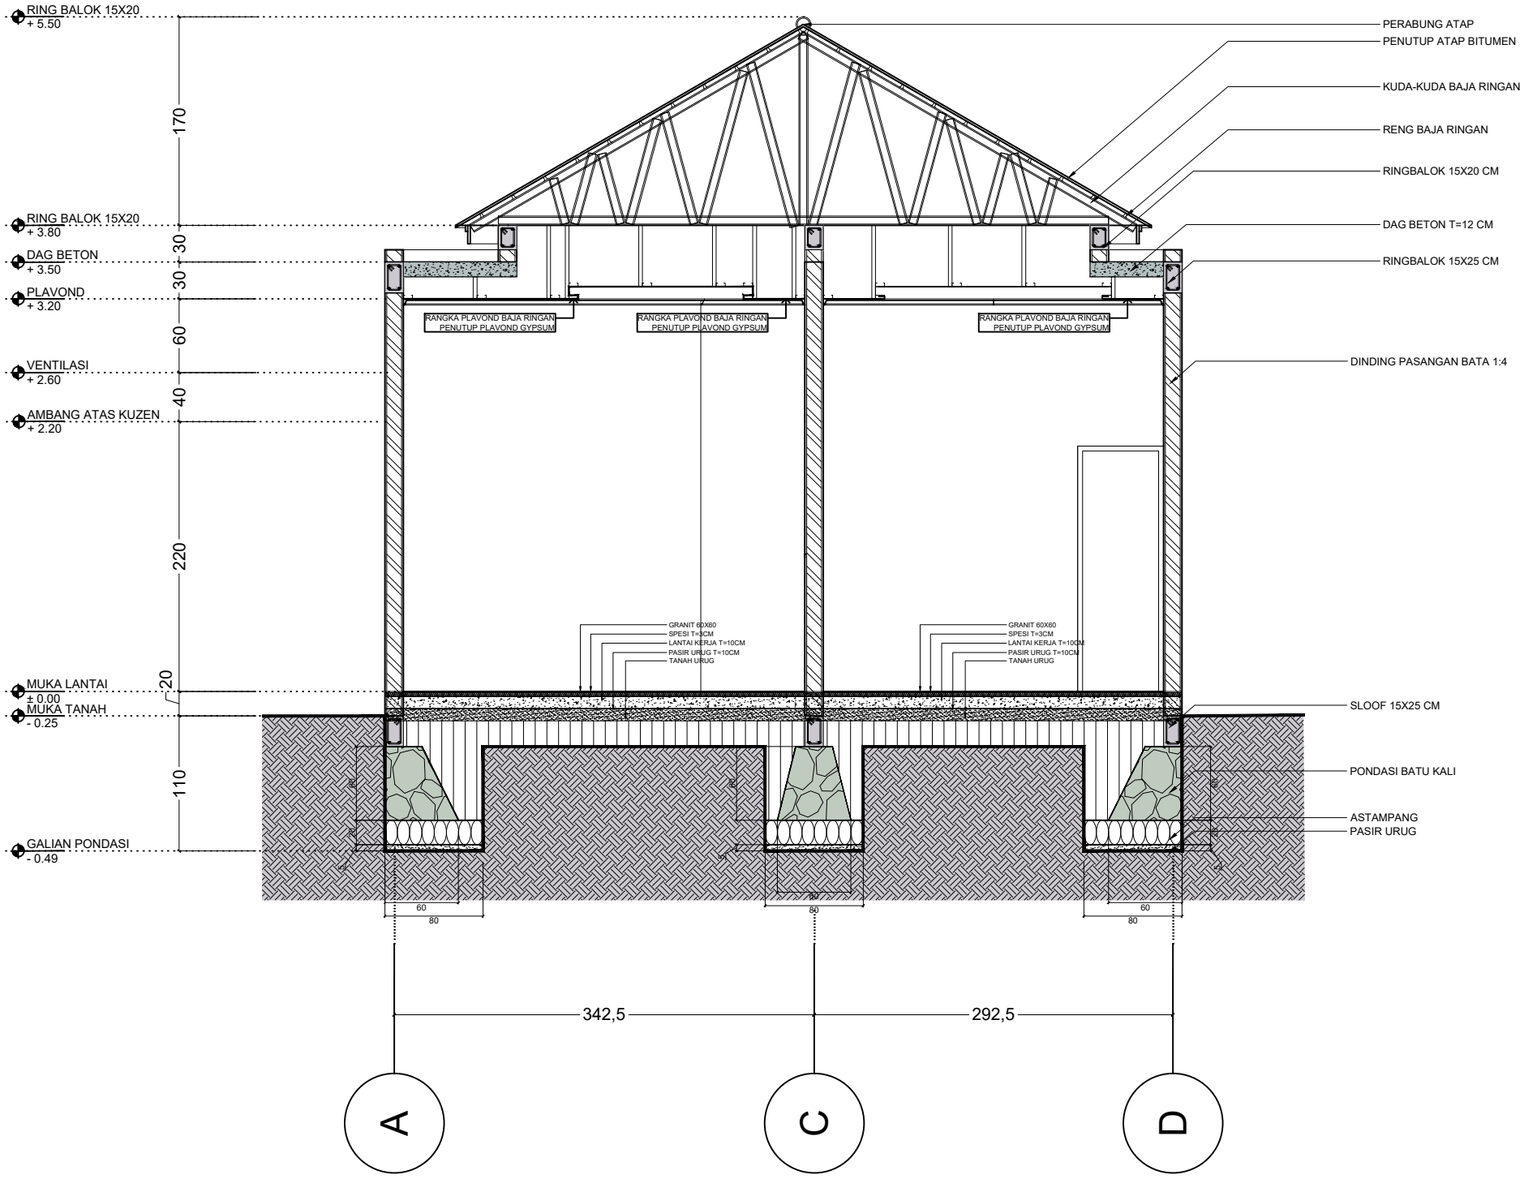

CODE
ARS

POTONGAN A-A

SKALA 1 : 50

ARCHILLES STUDIO

KETERANGAN :

PROJECT :

PERENCANAAN RUMAH HUNIAN

LOKASI :

PRAMUKA

OWNER :

.....

PERENCANA :

ARCHILLES TEAM

JUDUL GAMBAR	SKALA

TOTAL HALAMAN	CODE	NO HALAMAN



CODE
ARS

POTONGAN B-B

SKALA 1 : 60

ARCHILLES STUDIO

KETERANGAN :

PROJECT :

PERENCANAAN RUMAH HUNIAN

LOKASI :

PRAMUKA

OWNER :


.....

PERENCANA :

ARCHILLES TEAM

JUDUL GAMBAR	SKALA

TOTAL HALAMAN	CODE	NO HALAMAN

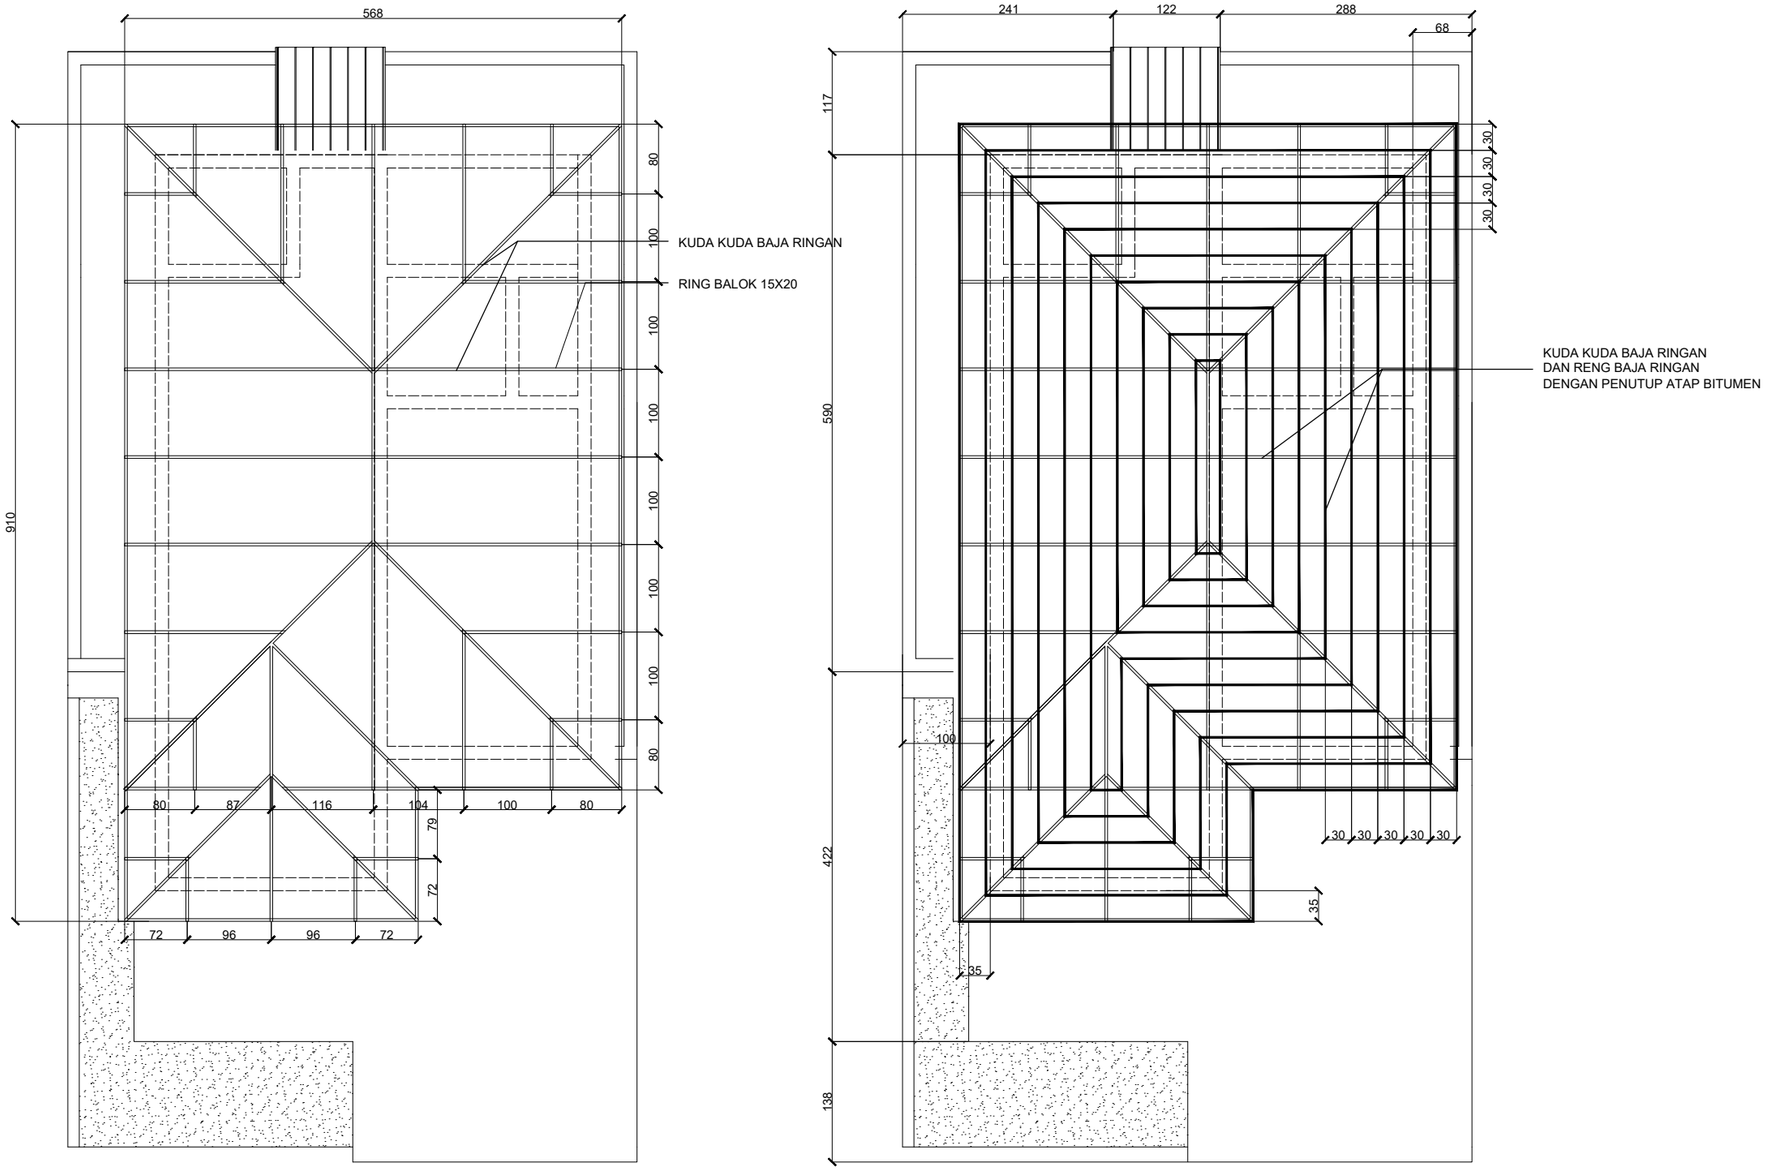

CODE ARS

DETAIL KUDA KUDA ATAP

SKALA 1 : 70

CODE ARS

DETAIL RANGKA ATAP

SKALA 1 : 70

ARCHILLES STUDIO

KETERANGAN :

PROJECT :

PERENCANAAN RUMAH HUNIAN

LOKASI :

PRAMUKA

OWNER :


.....

PERENCANA :

ARCHILLES TEAM

JUDUL GAMBAR	SKALA

TOTAL HALAMAN	CODE	NO HALAMAN

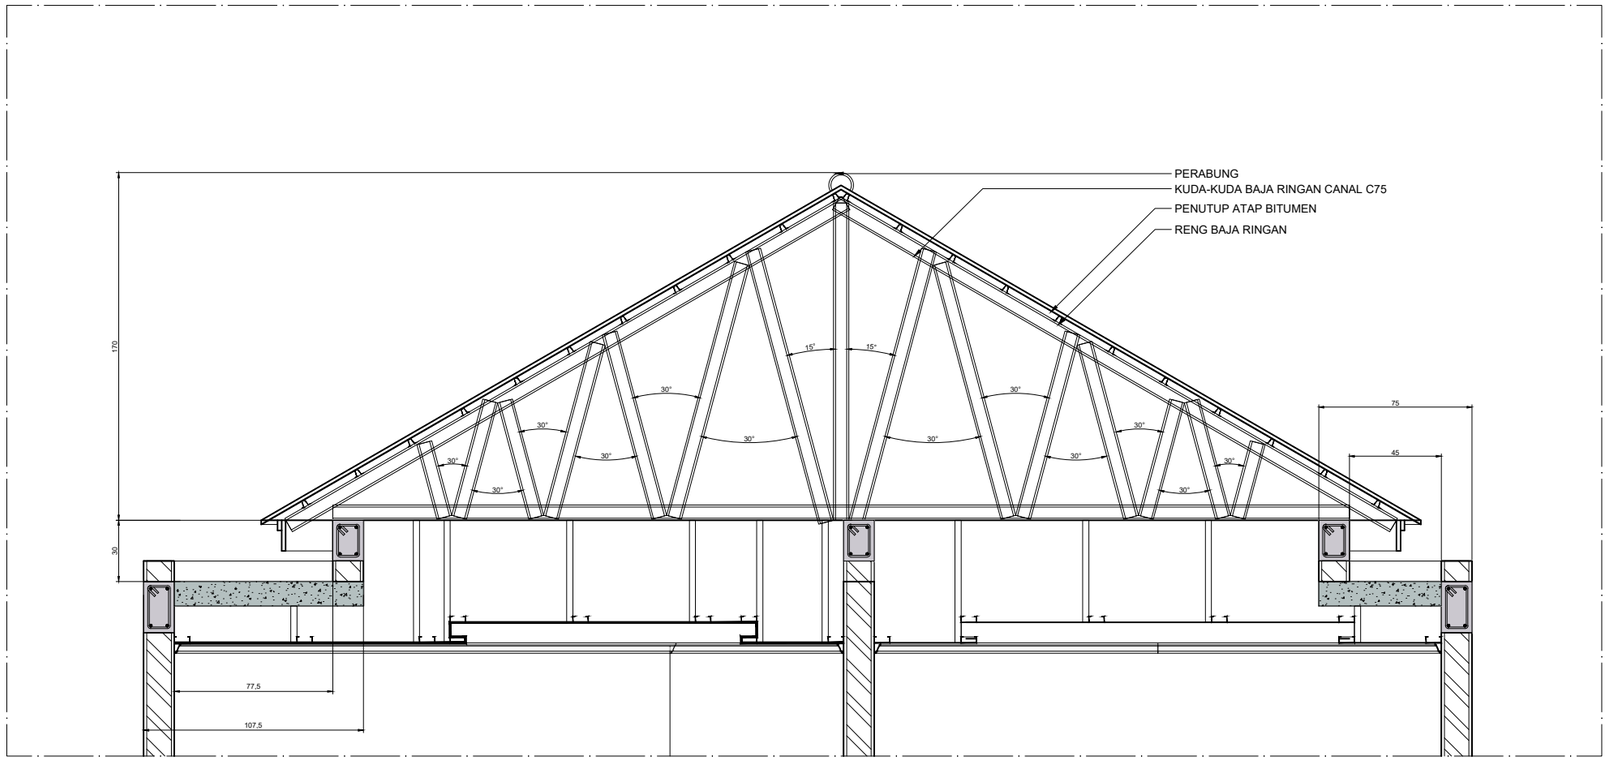

CODE
ARS

DETAIL POTONGAN ATAP

SKALA 1 : 30

ARCHILLES STUDIO

KETERANGAN :

PROJECT :

PERENCANAAN RUMAH HUNIAN

LOKASI :

PRAMUKA

OWNER :


.....


PERENCANA :

ARCHILLES TEAM

JUDUL GAMBAR	SKALA

TOTAL HALAMAN	CODE	NO HALAMAN

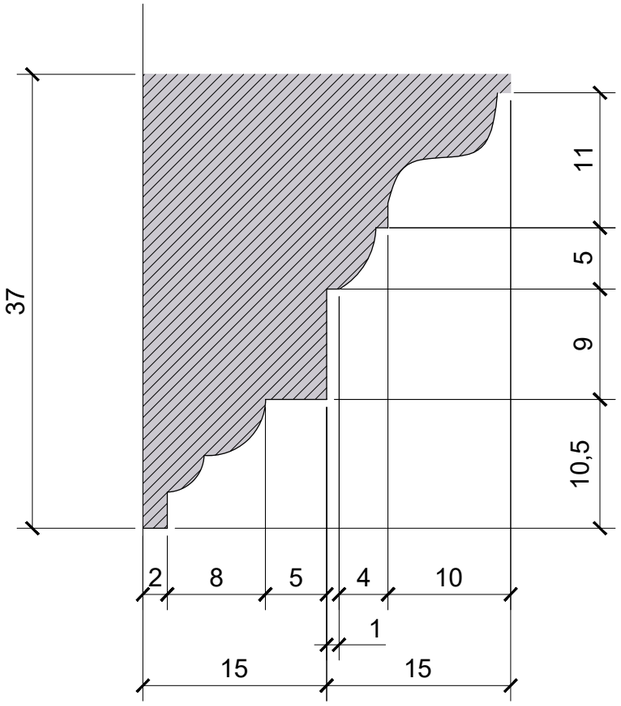

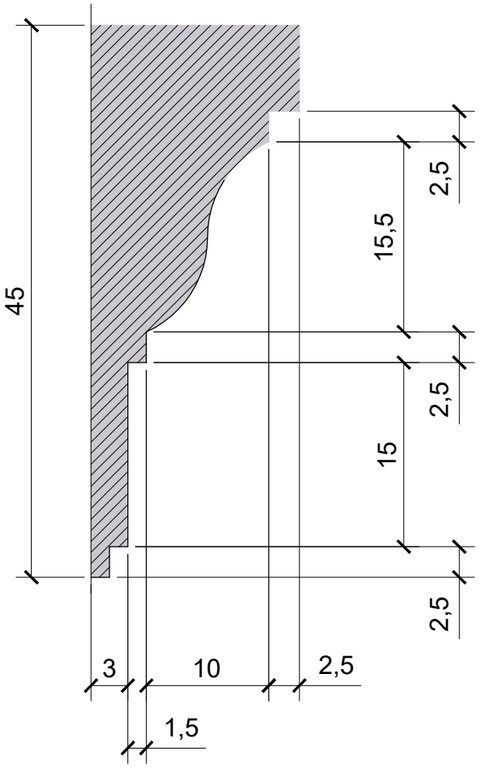

CODE
ARS

DETAIL LIST PROFIL

SKALA 1 : 5

ARCHILLES STUDIO

KETERANGAN :

PROJECT :

PERENCANAAN RUMAH HUNIAN

LOKASI :

PRAMUKA

OWNER :


.....

PERENCANA :

ARCHILLES TEAM

JUDUL GAMBAR	SKALA

TOTAL HALAMAN	CODE	NO HALAMAN

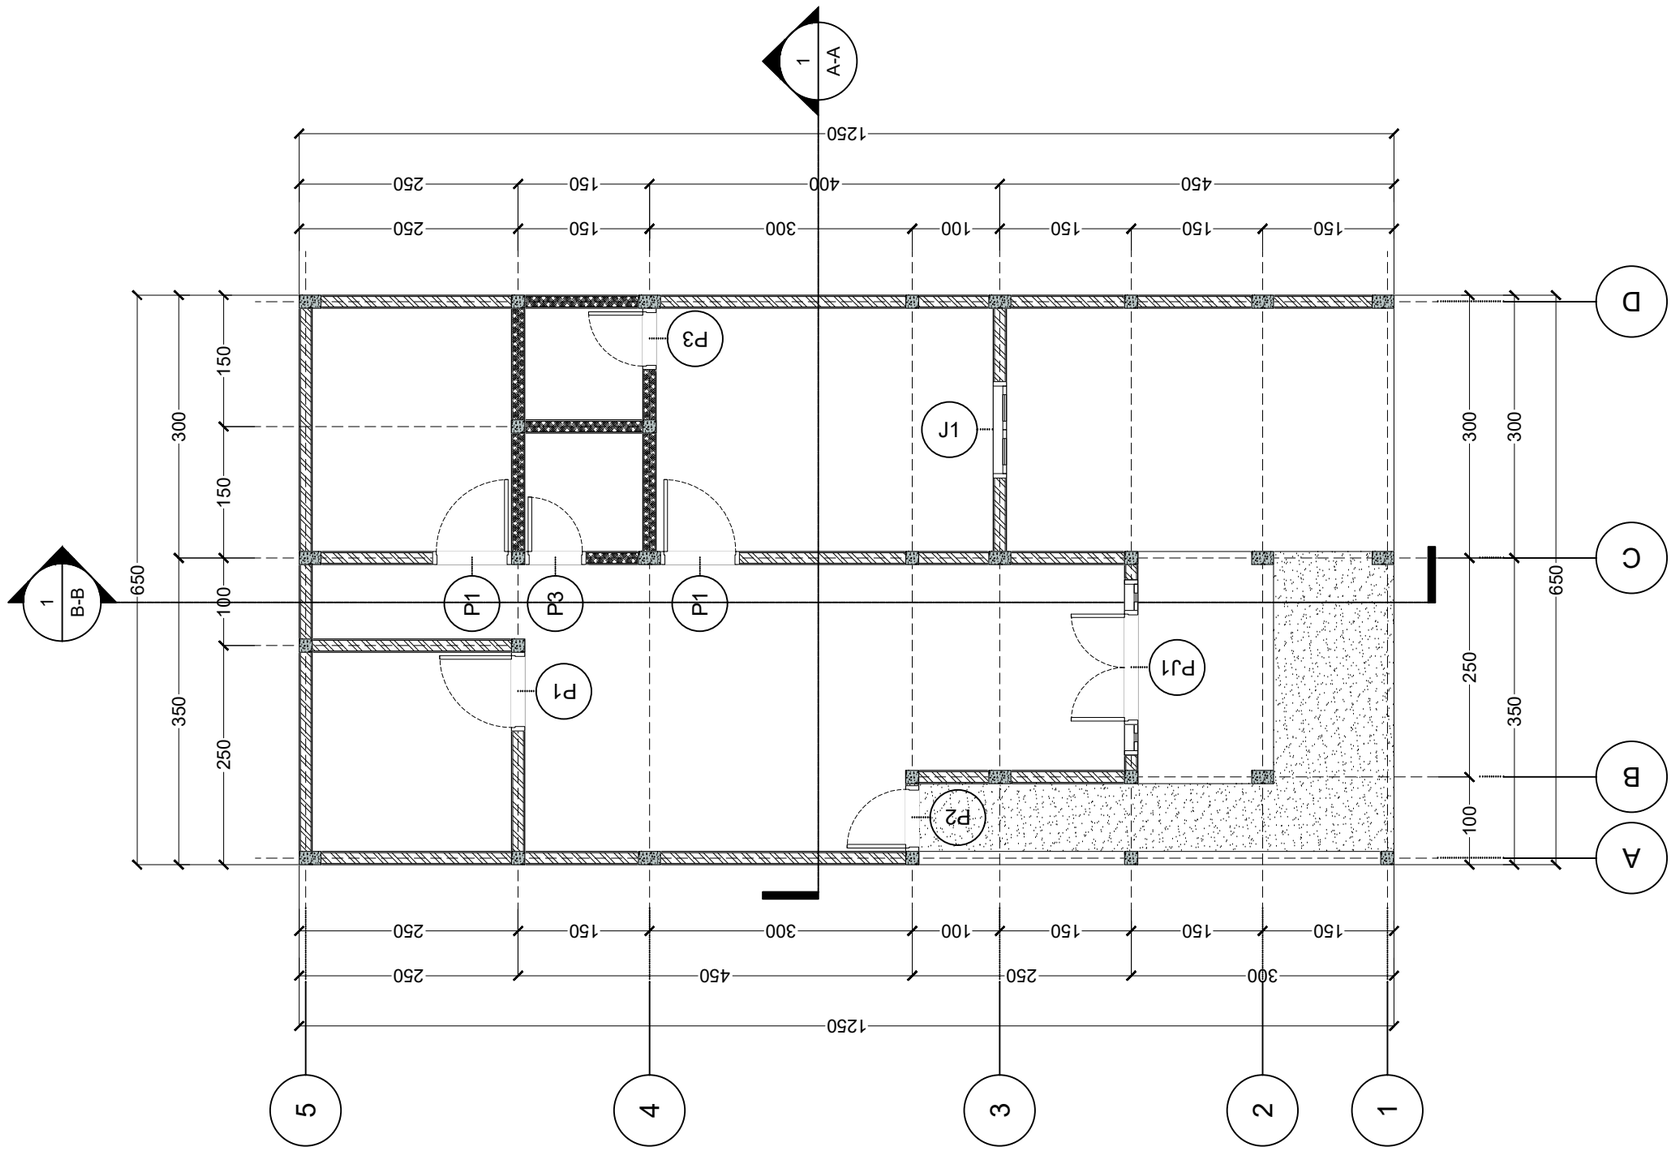

CODE
ARS

DENAH PERLETAKAN KUZEN

SKALA 1 : 70

ARCHILLES STUDIO

KETERANGAN :

PROJECT :

PERENCANAAN RUMAH HUNIAN

LOKASI :

PRAMUKA

OWNER :

.....


PERENCANA :

ARCHILLES TEAM

JUDUL GAMBAR	SKALA

TOTAL HALAMAN	CODE	NO HALAMAN

TIPE : PJ1	JUMLAH : 1

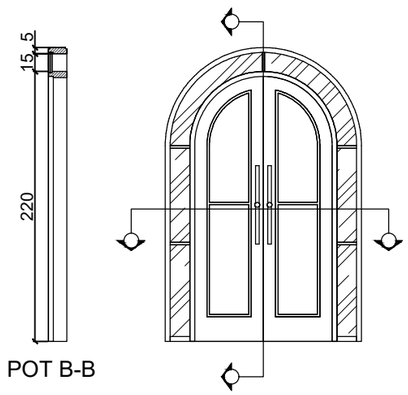

POT B-B

POT A-A


SPESIFIKASI MATERIAL	
KUZEN	KAYU BANIO
PINTU / JENDELA	KAYU SURIAN
KACA	5mm


TIPE : P1	JUMLAH : 3

TAMPAK ATAS




POT B-B

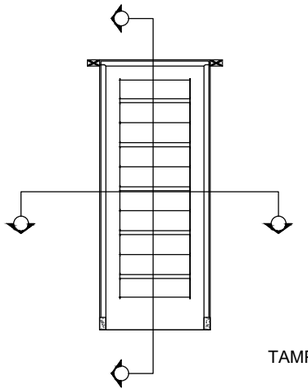

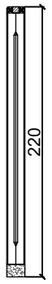

TAMPAK SAMPING

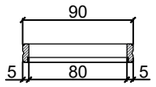

POT A-A


SPESIFIKASI MATERIAL	
KUZEN	KAYU BANIO
PINTU / JENDELA	KAYU SURIAN
KACA	-


TIPE : P2	JUMLAH : 1

TAMPAK ATAS




POT B-B

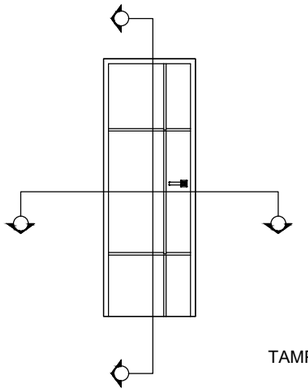

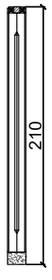

TAMPAK SAMPING

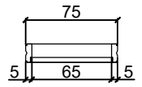

POT A-A

SPESIFIKASI MATERIAL	
KUZEN	KAYU BANIO
PINTU / JENDELA	KAYU SURIAN
KACA	-

CODE
ARS

DETAIL KUZEN

SKALA 1 : 50

ARCHILLES STUDIO

KETERANGAN :

PROJECT :

PERENCANAAN RUMAH HUNIAN

LOKASI :

PRAMUKA

OWNER :

.....


PERENCANA :

ARCHILLES TEAM


JUDUL GAMBAR	SKALA

TOTAL HALAMAN	CODE	NO HALAMAN

TIPE : J1	JUMLAH : 2

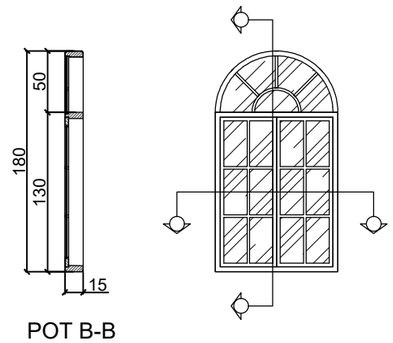


POT B-B

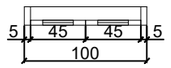


POT A-A

SPESIFIKASI MATERIAL	
KUZEN	KAYU BANIO
PINTU / JENDELA	KAYU SURIAN
KACA	5mm

TIPE : P3	JUMLAH : 2

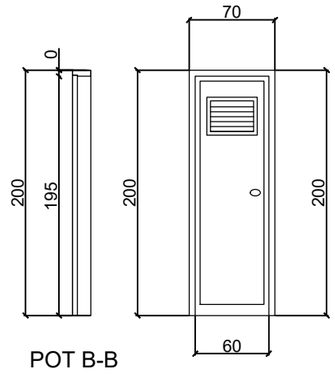

POT B-B

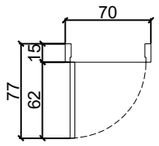

POT A-A

SPESIFIKASI MATERIAL	
KUZEN	PVC
PINTU / JENDELA	PVC
KACA	-

CODE
ARS

DETAIL KUZEN

SKALA 1 : 50

ARCHILLES STUDIO

KETERANGAN :

PROJECT :

PERENCANAAN RUMAH HUNIAN

LOKASI :

PRAMUKA

OWNER :


.....

PERENCANA :

ARCHILLES TEAM

JUDUL GAMBAR	SKALA

TOTAL HALAMAN	CODE	NO HALAMAN

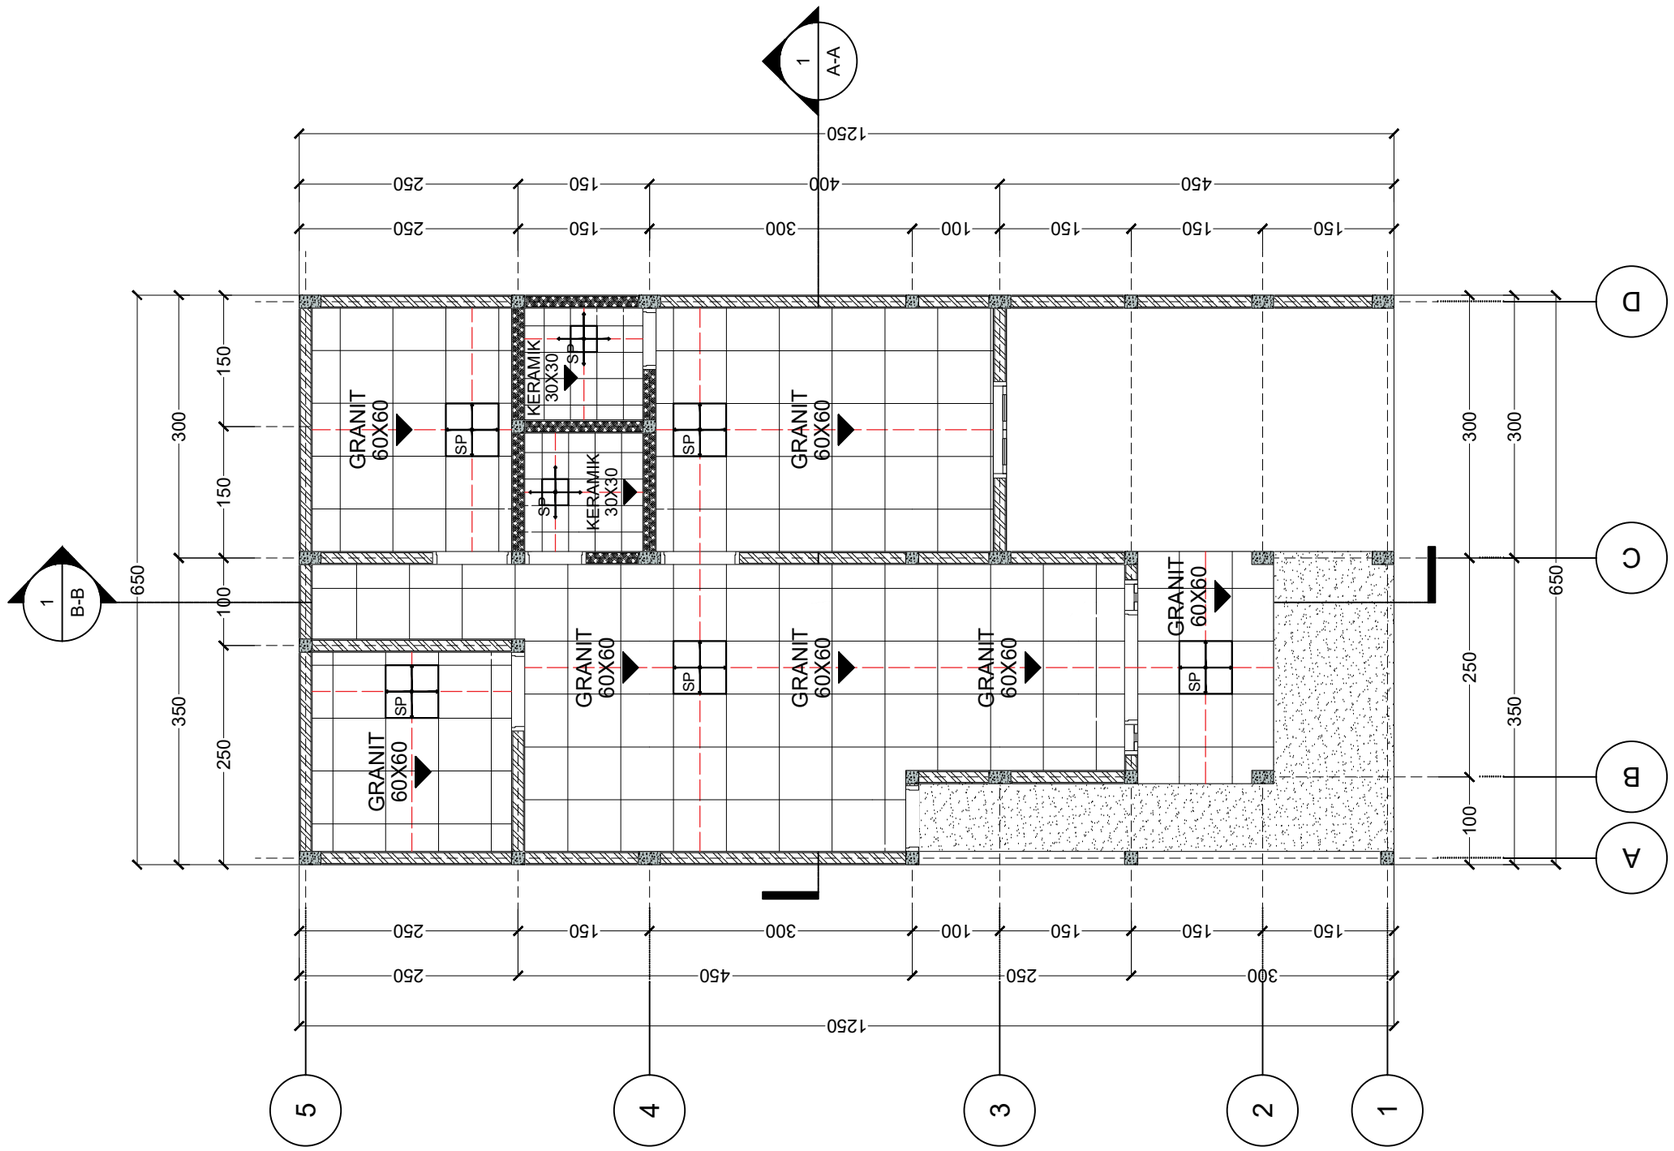

DENAH POLA LANTAI

CODE
ARS

SKALA 1 : 70

ARCHILLES STUDIO

KETERANGAN :

PROJECT :

PERENCANAAN RUMAH HUNIAN

LOKASI :

PRAMUKA

OWNER :


.....

PERENCANA :

ARCHILLES TEAM

JUDUL GAMBAR	SKALA

TOTAL HALAMAN	CODE	NO HALAMAN

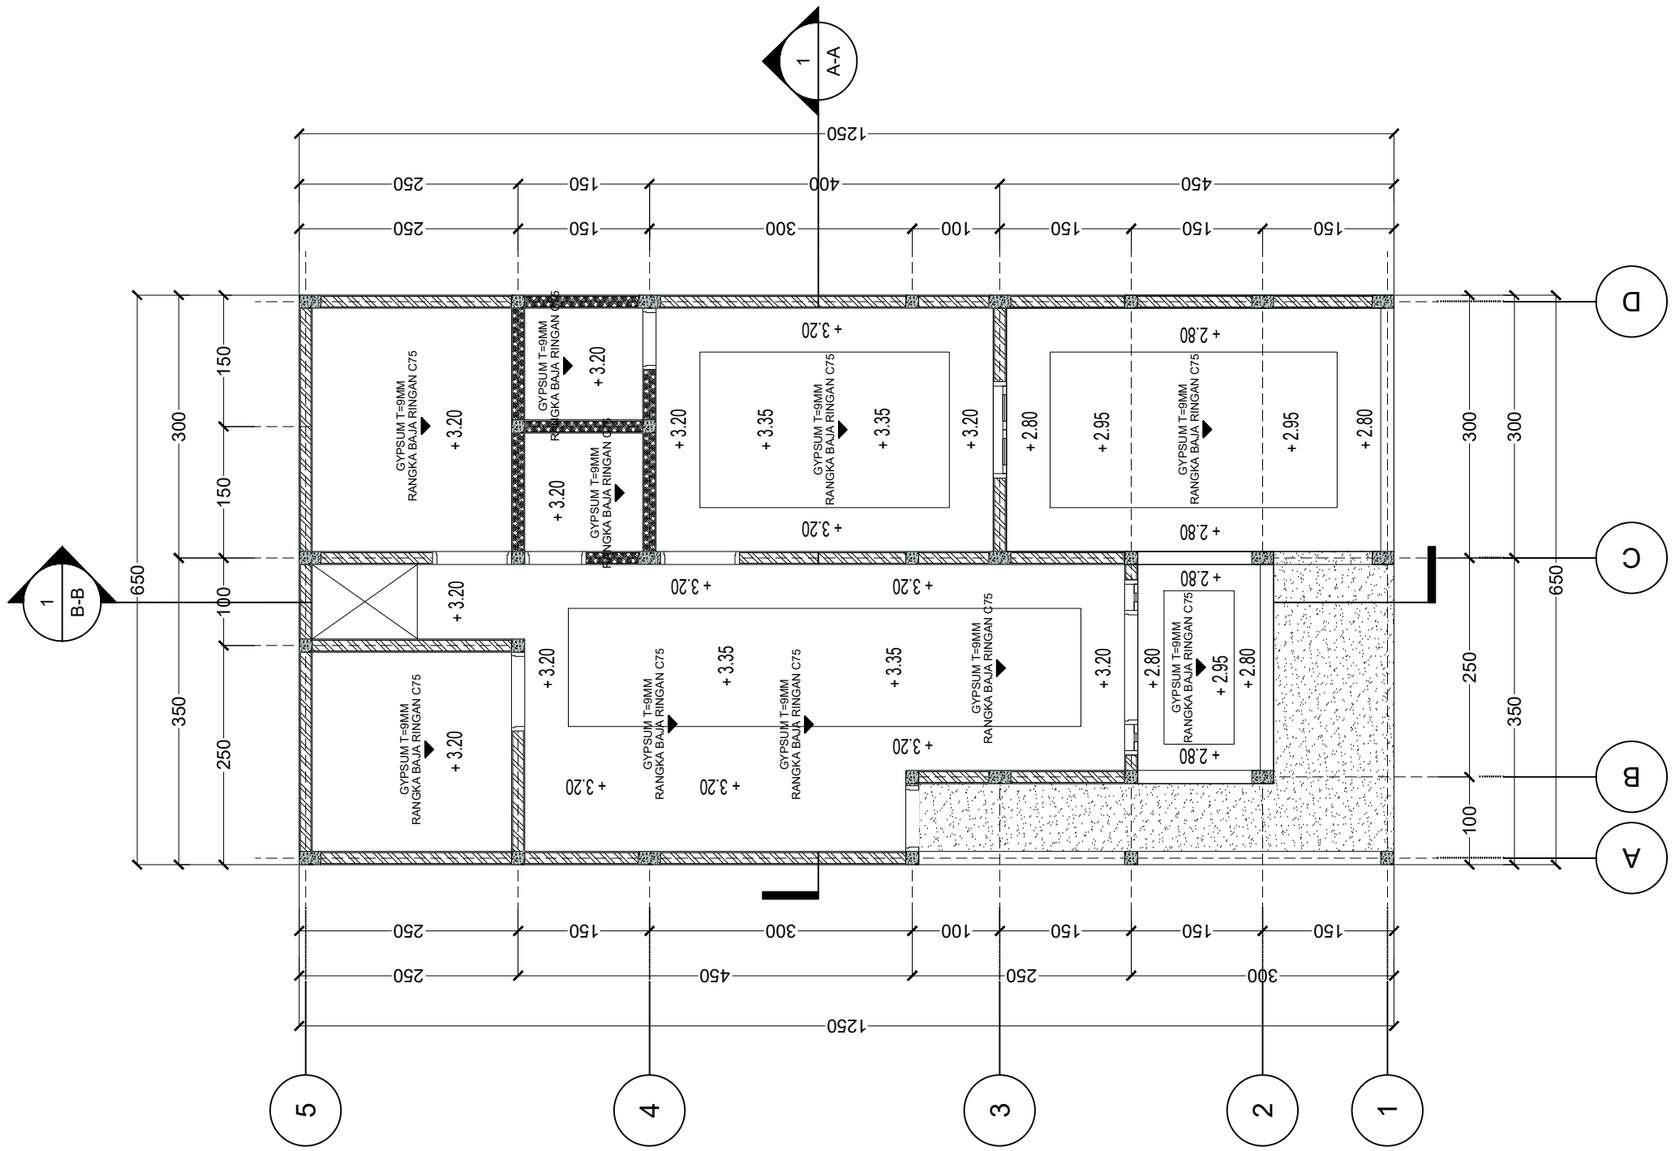

CODE
ARS

DENAH PEMASANGAN PLAVOND

SKALA 1 : 70

ARCHILLES STUDIO

KETERANGAN :

PROJECT :

PERENCANAAN RUMAH HUNIAN

LOKASI :

PRAMUKA

OWNER :


.....

PERENCANA :

ARCHILLES TEAM

JUDUL GAMBAR	SKALA

TOTAL HALAMAN	CODE	NO HALAMAN

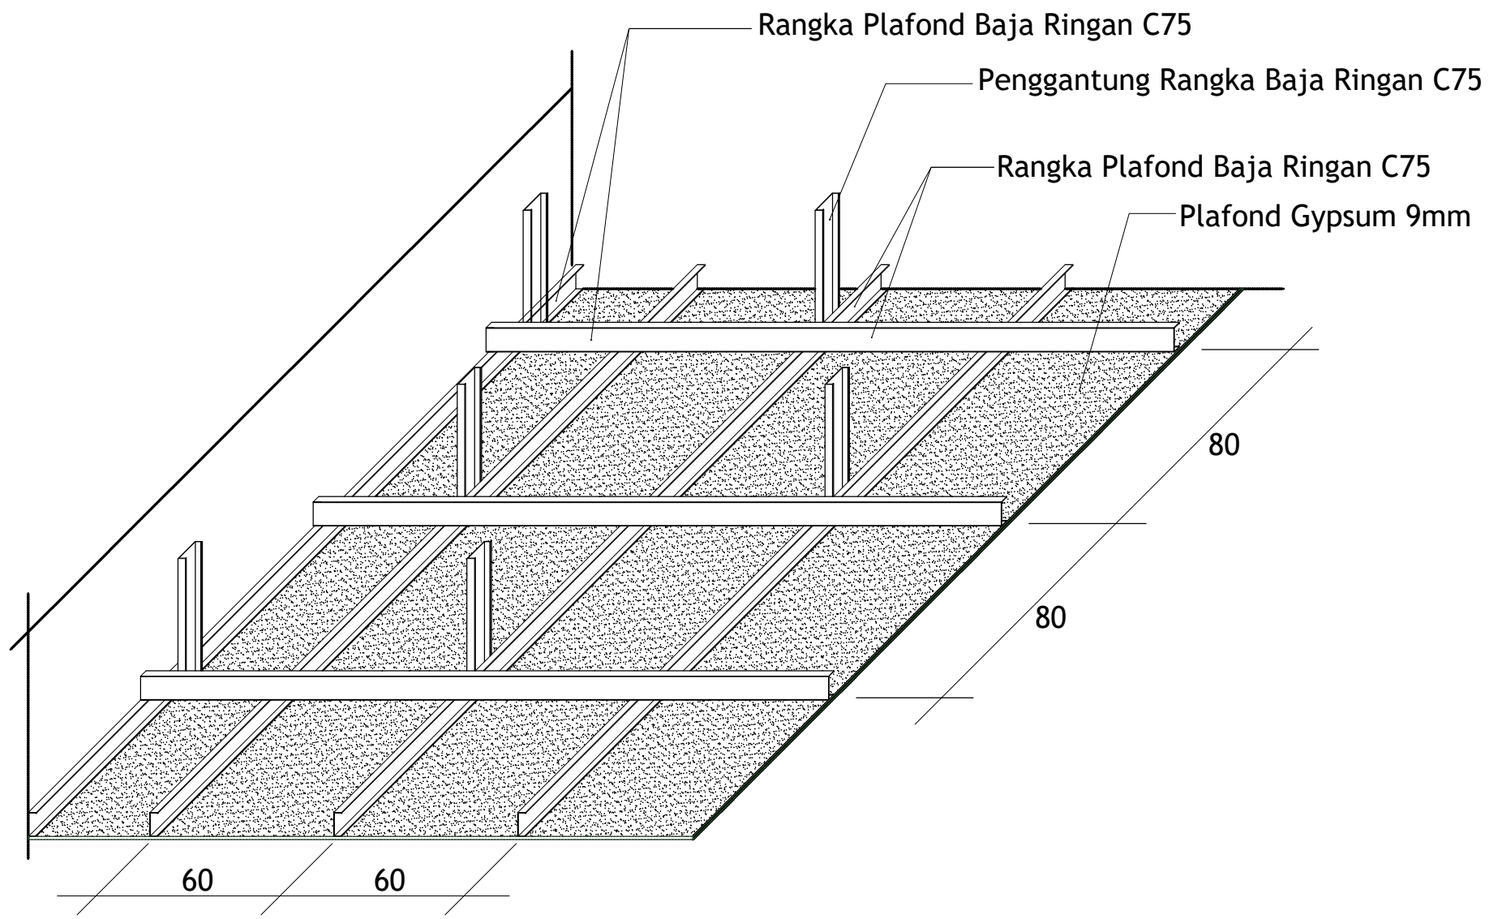

CODE
ARS

PERSPEKTIF RANGKA PLAVOND

SKALA 1 : 20

ARCHILLES STUDIO

KETERANGAN :

PROJECT :

PERENCANAAN RUMAH HUNIAN

LOKASI :

PRAMUKA

OWNER :

.....

PERENCANA :

ARCHILLES TEAM

JUDUL GAMBAR	SKALA


TOTAL HALAMAN	CODE	NO HALAMAN

ARCHILLES
STUDIO

STRUKTUR

CODE :

STR

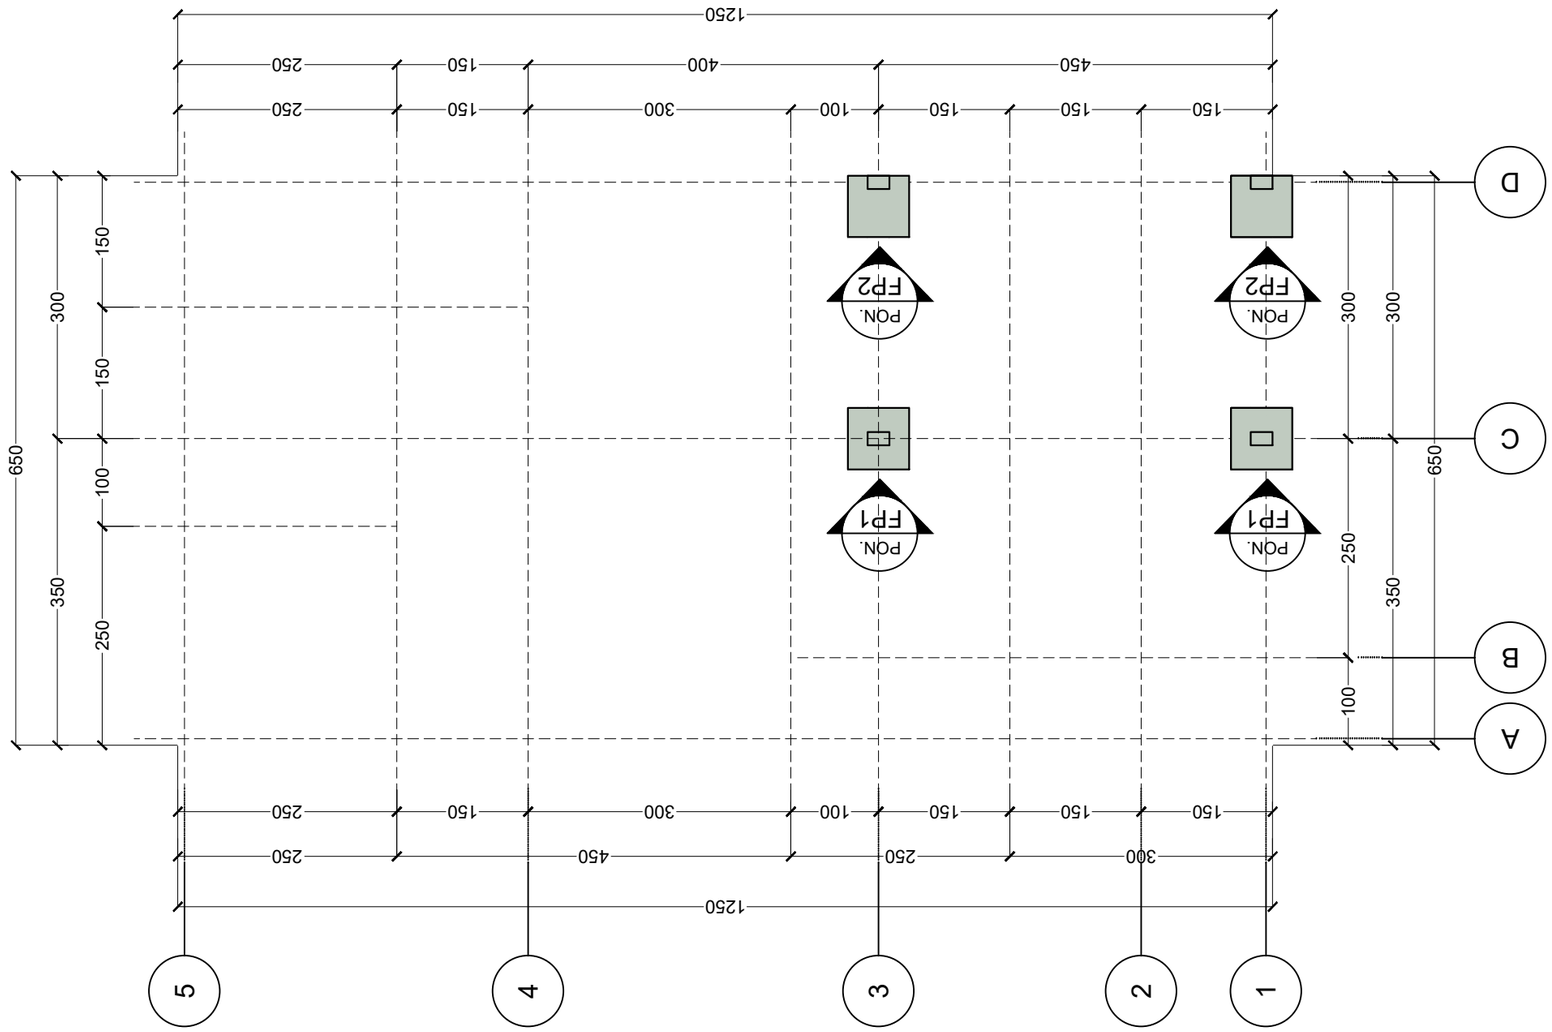

DENAH PONDASI FOOTPLATE

CODE
STR

SKALA 1 : 70

ARCHILLES STUDIO

KETERANGAN :

PROJECT :

PERENCANAAN RUMAH HUNIAN

LOKASI :

PRAMUKA

OWNER :


.....

PERENCANA :

ARCHILLES TEAM

JUDUL GAMBAR	SKALA

TOTAL HALAMAN	CODE	NO HALAMAN

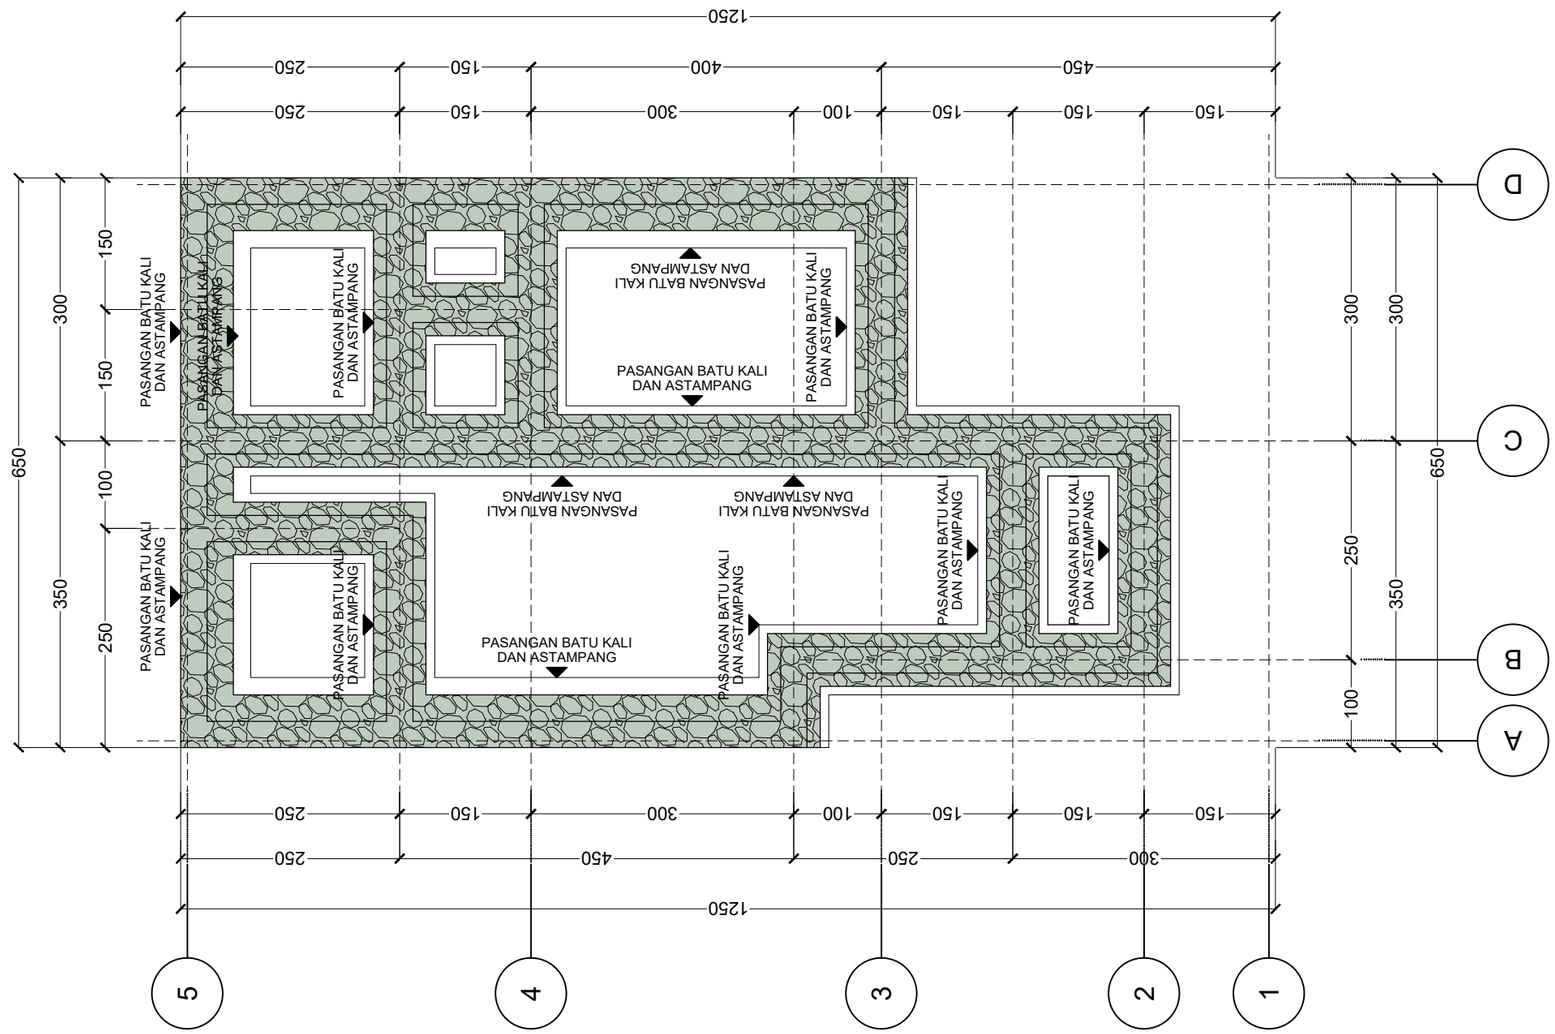

CODE
STR

DENAH PONDASI BATU KALI

SKALA 1 : 70

ARCHILLES STUDIO

KETERANGAN :

PROJECT :

PERENCANAAN RUMAH HUNIAN

LOKASI :

PRAMUKA

OWNER :


.....

PERENCANA :

ARCHILLES TEAM

JUDUL GAMBAR	SKALA

TOTAL HALAMAN	CODE	NO HALAMAN

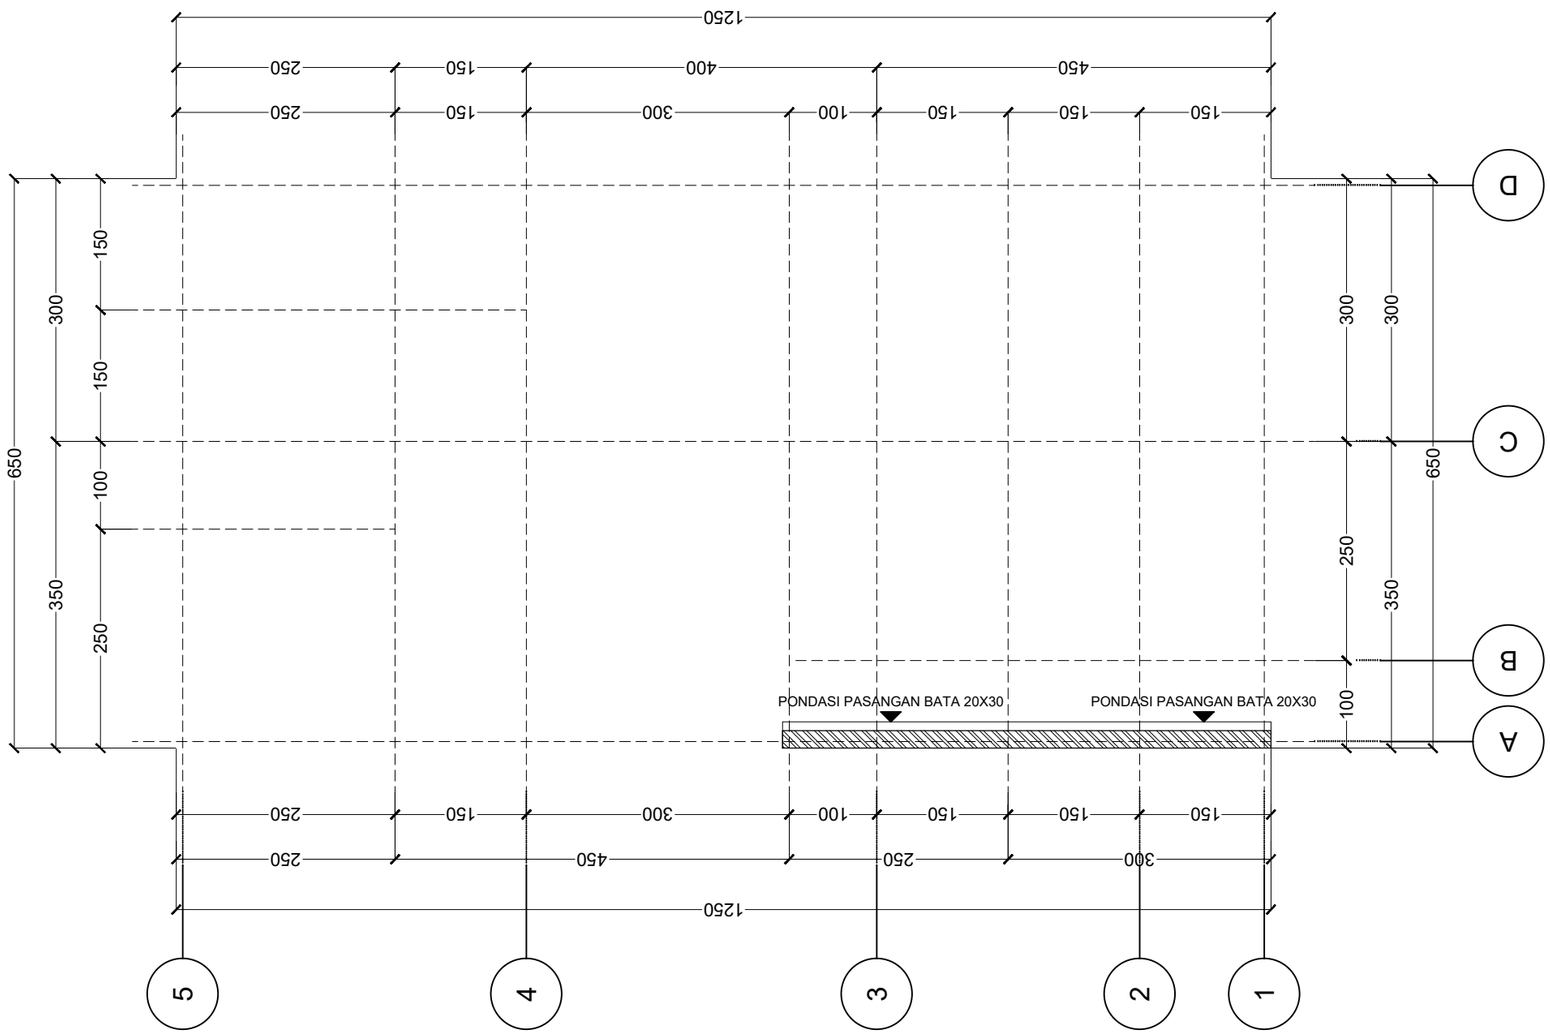

CODE
STR

DENAH PONDASI PASANGAN BATA

SKALA 1 : 70

ARCHILLES STUDIO

KETERANGAN :

PROJECT :

PERENCANAAN RUMAH HUNIAN

LOKASI :

PRAMUKA

OWNER :


.....


PERENCANA :

ARCHILLES TEAM

JUDUL GAMBAR	SKALA

TOTAL HALAMAN	CODE	NO HALAMAN

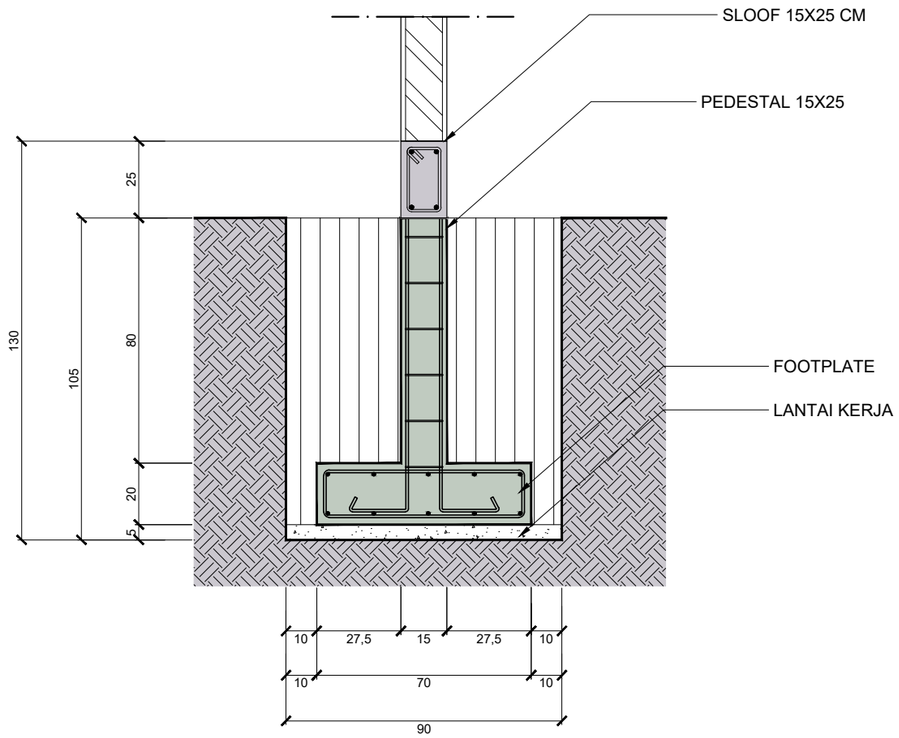


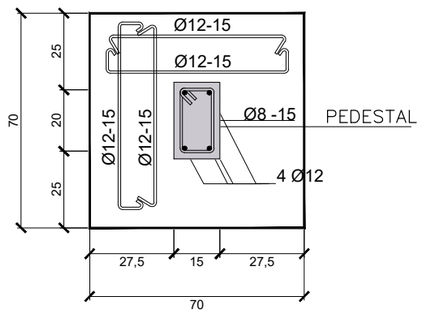


CODE STR

DETAIL PONDASI FOOTPLATE FP1

SKALA 1 : 20

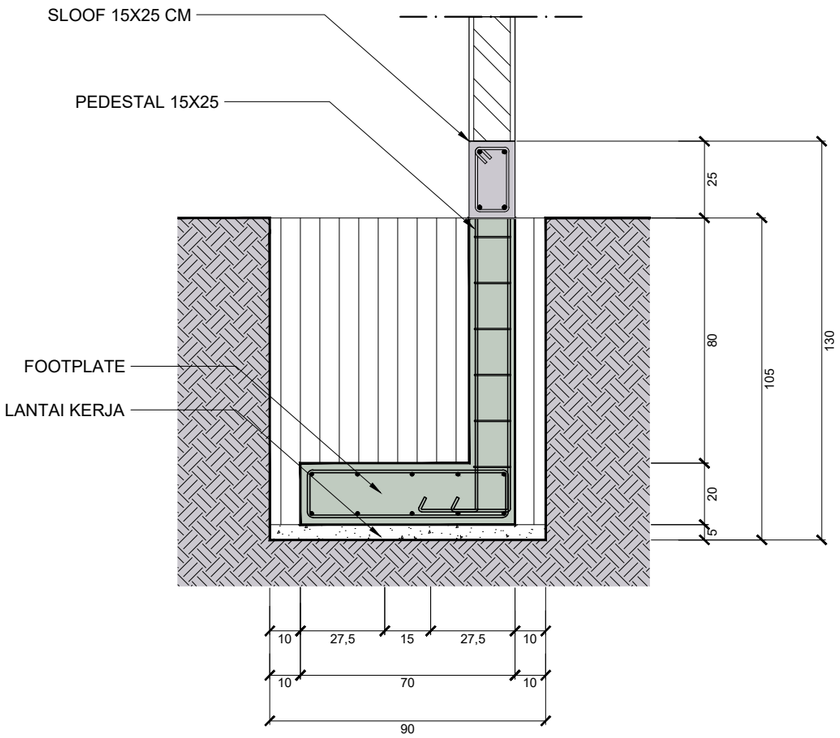

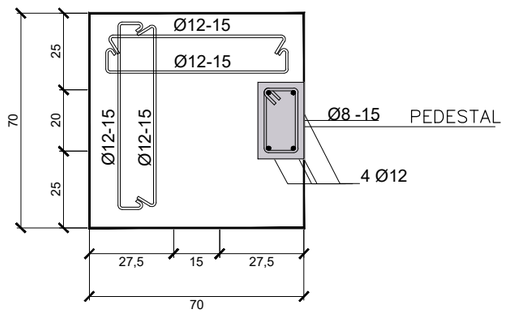

CODE STR

DETAIL PONDASI FOOTPLATE FP2

SKALA 1 : 20

ARCHILLES STUDIO

KETERANGAN :

PROJECT :

PERENCANAAN RUMAH HUNIAN

LOKASI :

PRAMUKA

OWNER :


.....


PERENCANA :


ARCHILLES TEAM


JUDUL GAMBAR	SKALA

TOTAL HALAMAN	CODE	NO HALAMAN

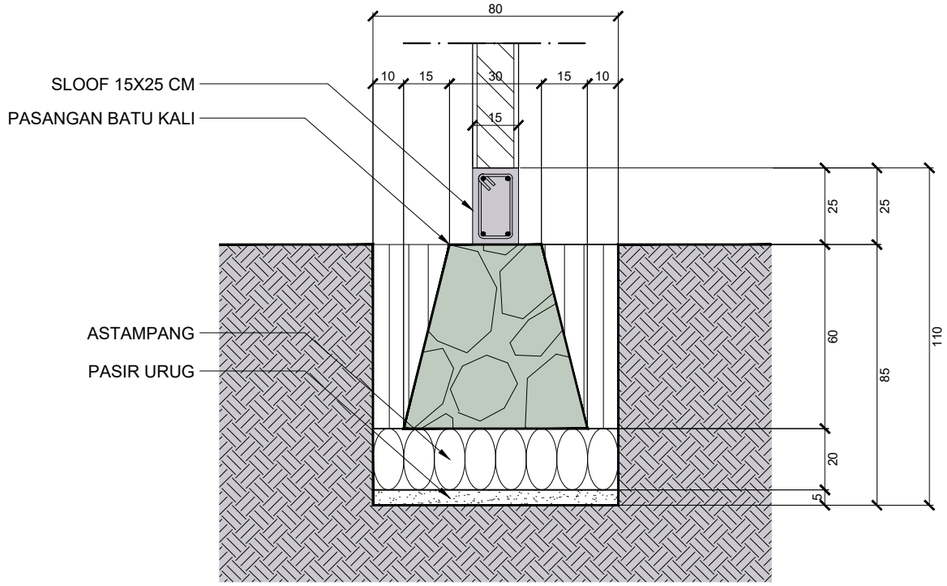

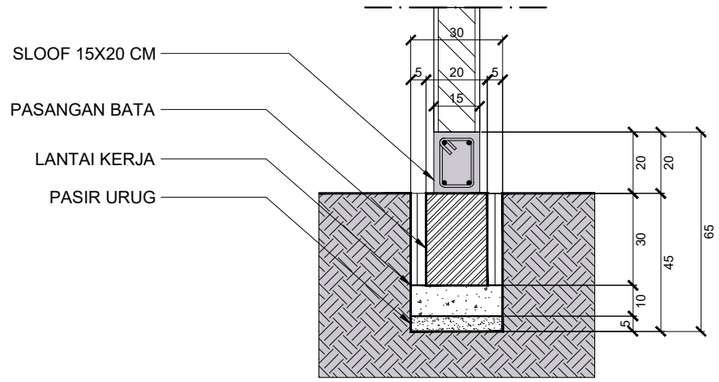

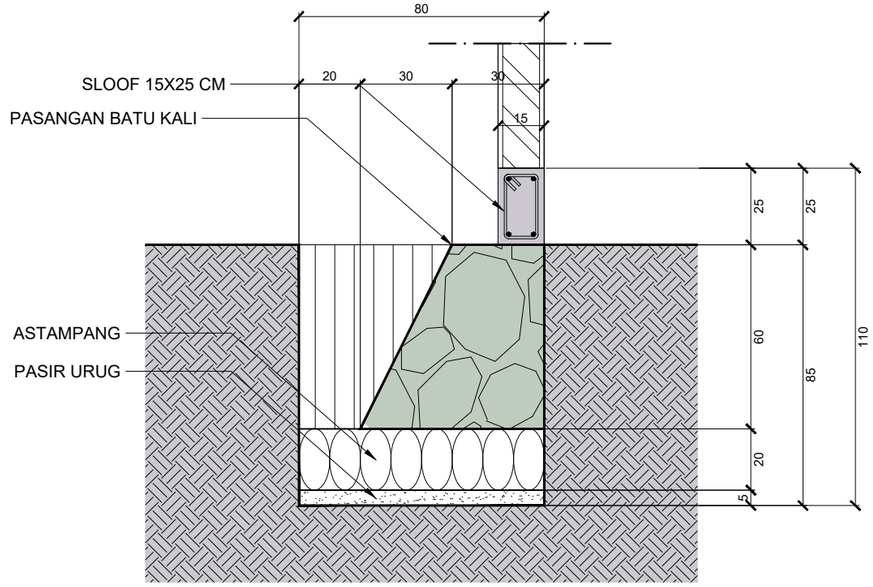

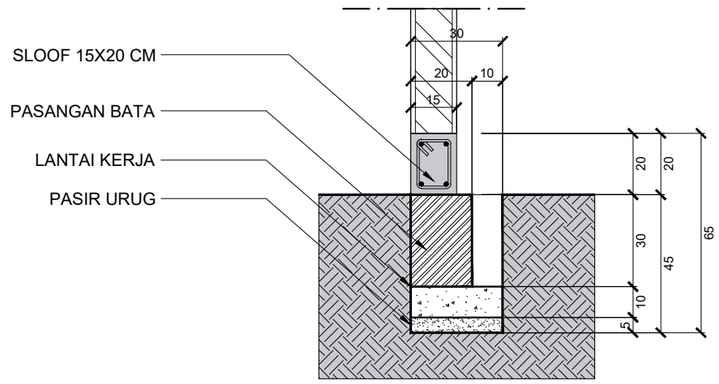

CODE STR

DETAIL PONDASI PASANGAN BATU KALI

SKALA 1 : 20

CODE STR

DETAIL PONDASI PASANGAN BATU BATA

SKALA 1 : 20

ARCHILLES STUDIO

KETERANGAN :

PROJECT :

PERENCANAAN RUMAH HUNIAN

LOKASI :

PRAMUKA

OWNER :


.....

PERENCANA :

ARCHILLES TEAM

JUDUL GAMBAR	SKALA

TOTAL HALAMAN	CODE	NO HALAMAN

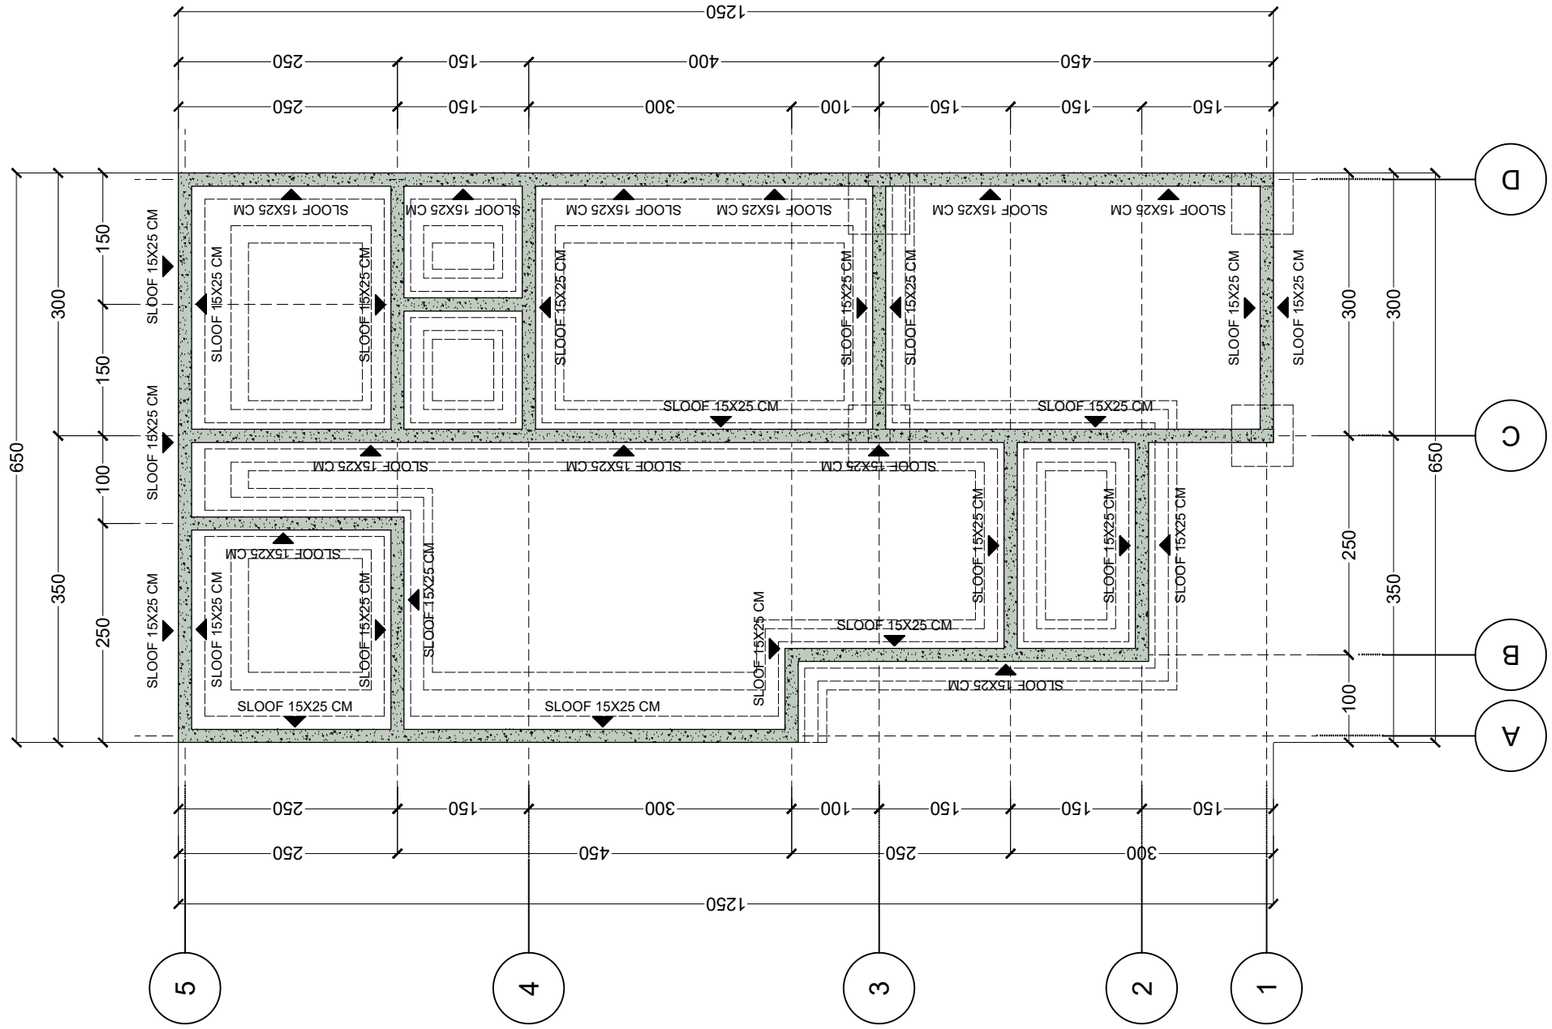

CODE
STR

DENAH SLOOF 15X25

SKALA 1 : 70

GEOMETRI SLOOF SLF1		
DIMENSI	15 x 25	
TUL. ATAS	2 Ø 12	2 Ø 12
TUL.TENGAH	-	-
TUL. BAWAH	2 Ø 12	2 Ø 12
JARAK BEUGEL	¼ H	½ H
	Ø8 - 10	Ø8 - 20

ARCHILLES STUDIO

KETERANGAN :

PROJECT :

PERENCANAAN RUMAH HUNIAN

LOKASI :

PRAMUKA

OWNER :


.....

PERENCANA :

ARCHILLES TEAM

JUDUL GAMBAR	SKALA

TOTAL HALAMAN	CODE	NO HALAMAN

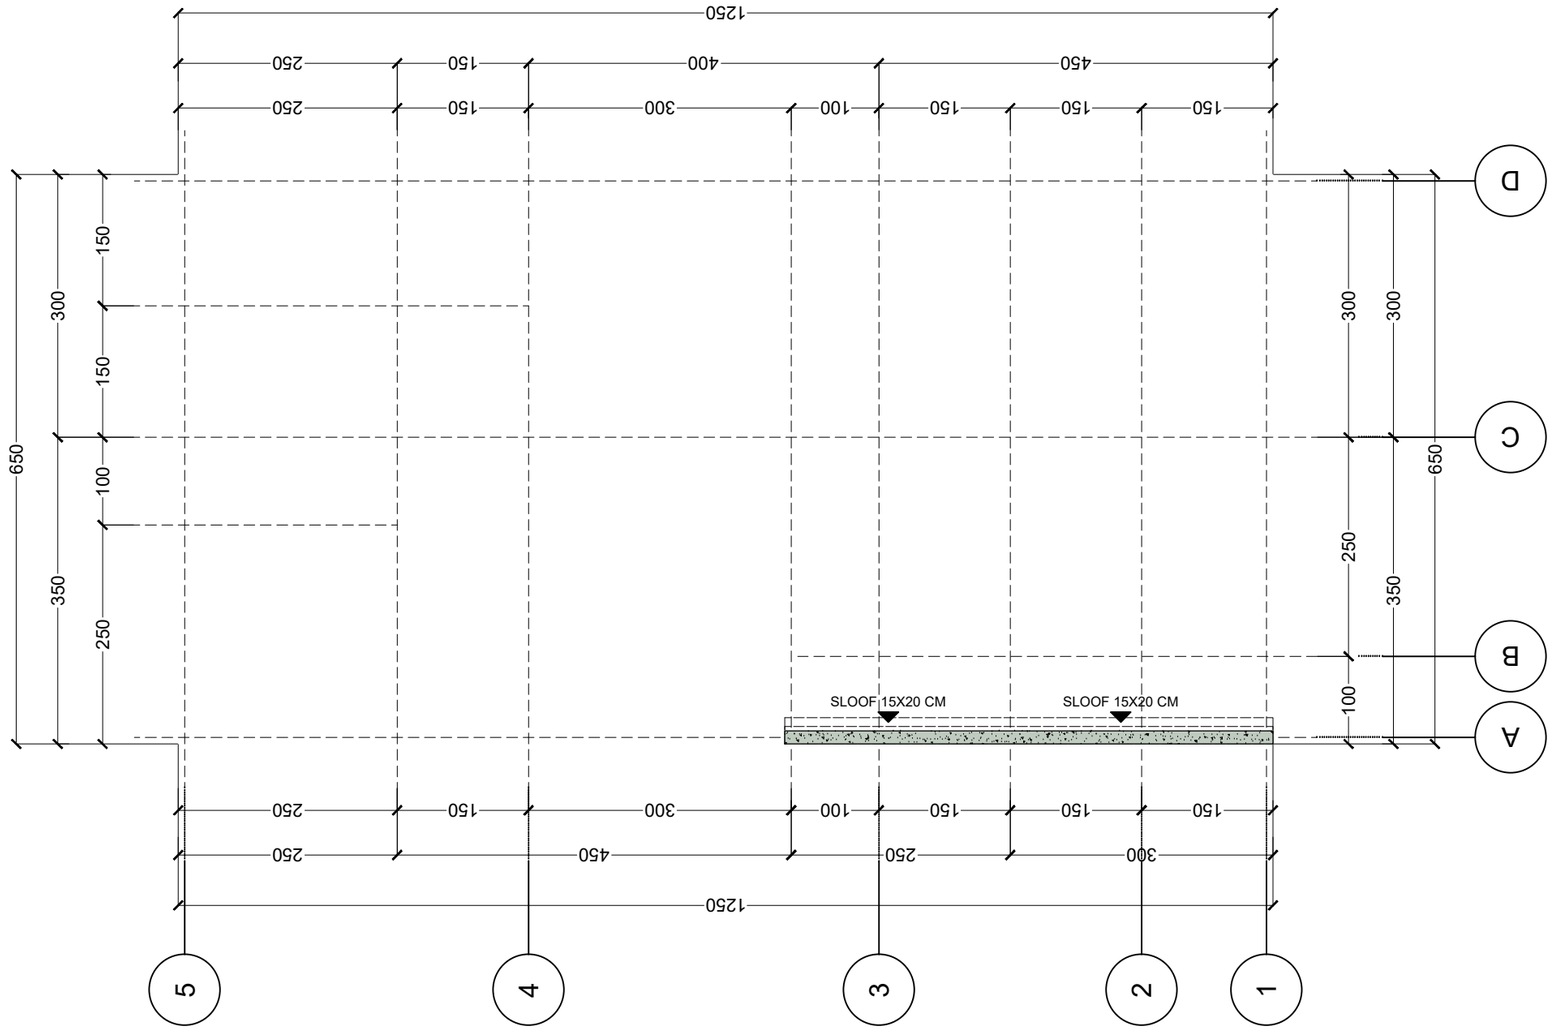

CODE
STR

DENAH SLOOF 15X20

SKALA 1 : 70

GEOMETRI SLOOF SLF 2		
DIMENSI	15 x 20	
TUL. ATAS	2 Ø 12	2 Ø 12
TUL.TENGAH	-	-
TUL. BAWAH	2 Ø 12	2 Ø 12
JARAK BEUGEL	¼ H	½ H
	Ø8 - 10	Ø8 - 20

ARCHILLES STUDIO

KETERANGAN :

PROJECT :

PERENCANAAN RUMAH HUNIAN

LOKASI :

PRAMUKA

OWNER :


.....

PERENCANA :

ARCHILLES TEAM

JUDUL GAMBAR	SKALA

TOTAL HALAMAN	CODE	NO HALAMAN

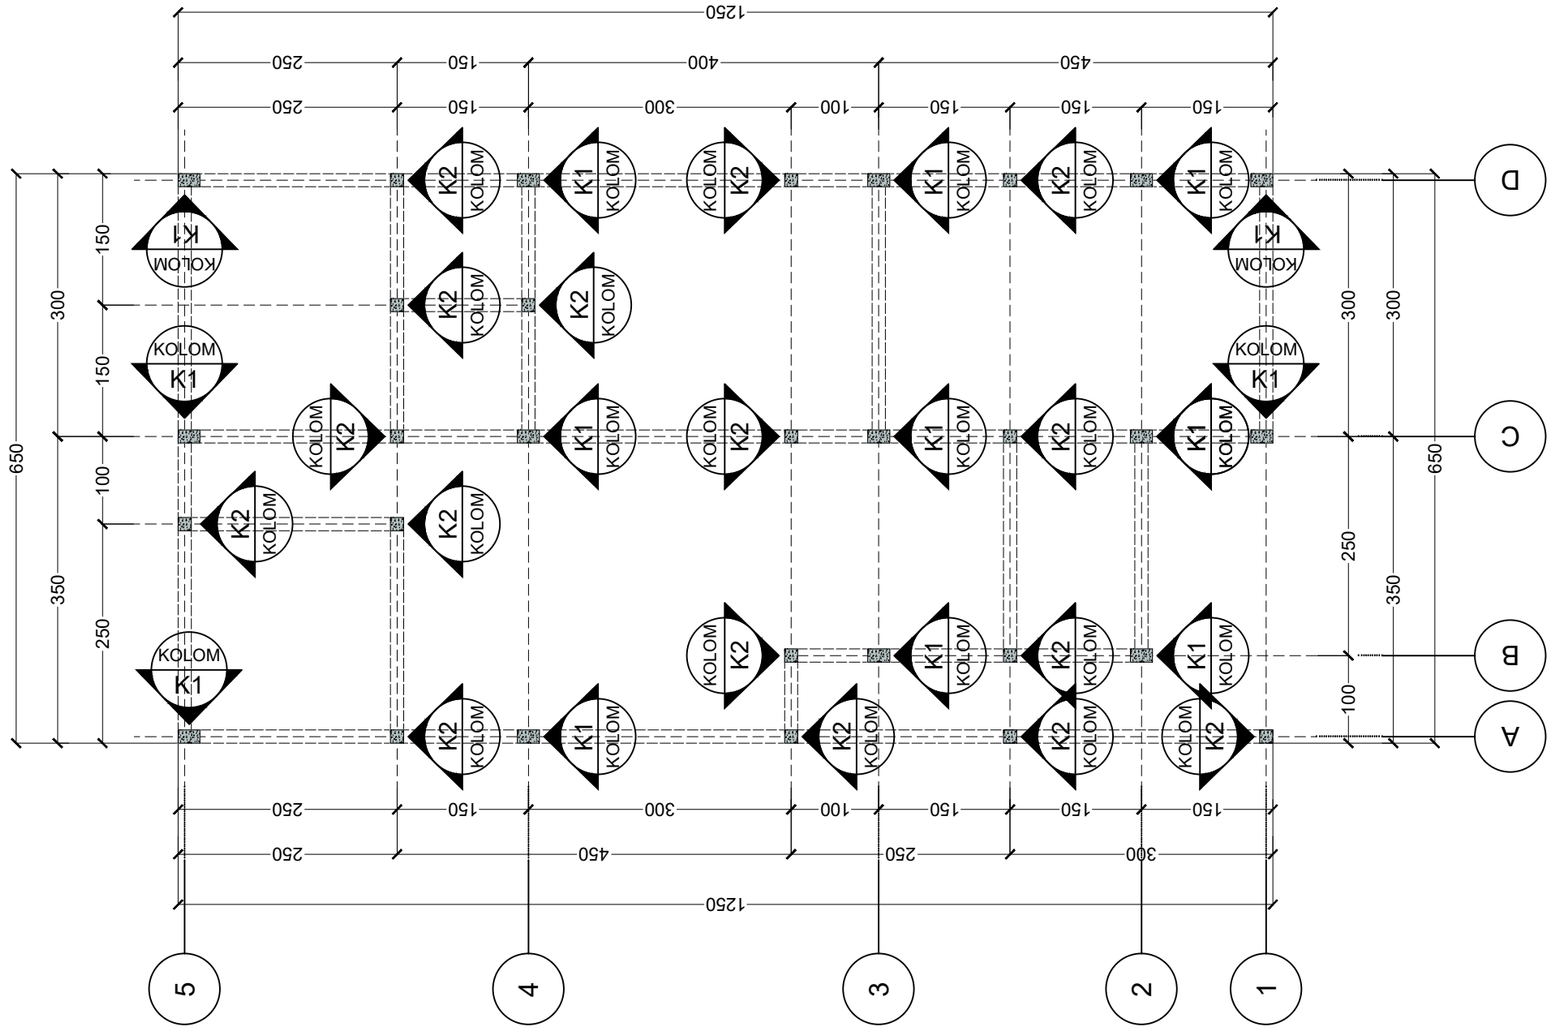

DENAH KOLOM

CODE
STR

SKALA 1 : 70

GEOMETRI KOLOM K1		
DIMENSI	15 x 25	
TUL. ATAS	2 Ø 12	2 Ø 12
TUL.TENGAH	-	-
TUL. BAWAH	2 Ø 12	2 Ø 12
JARAK BEUGEL	¼ H	½ H
	Ø8 - 10	Ø8 - 15

GEOMETRI KOLOM K2		
DIMENSI	15 x 15	
TUL. ATAS	2 Ø 12	2 Ø 12
TUL.TENGAH	-	-
TUL. BAWAH	2 Ø 12	2 Ø 12
JARAK BEUGEL	¼ H	½ H
	Ø8 - 10	Ø8 - 15

ARCHILLES STUDIO

KETERANGAN :

PROJECT :

PERENCANAAN RUMAH HUNIAN

LOKASI :

PRAMUKA

OWNER :


.....

PERENCANA :

ARCHILLES TEAM

JUDUL GAMBAR	SKALA

TOTAL HALAMAN	CODE	NO HALAMAN

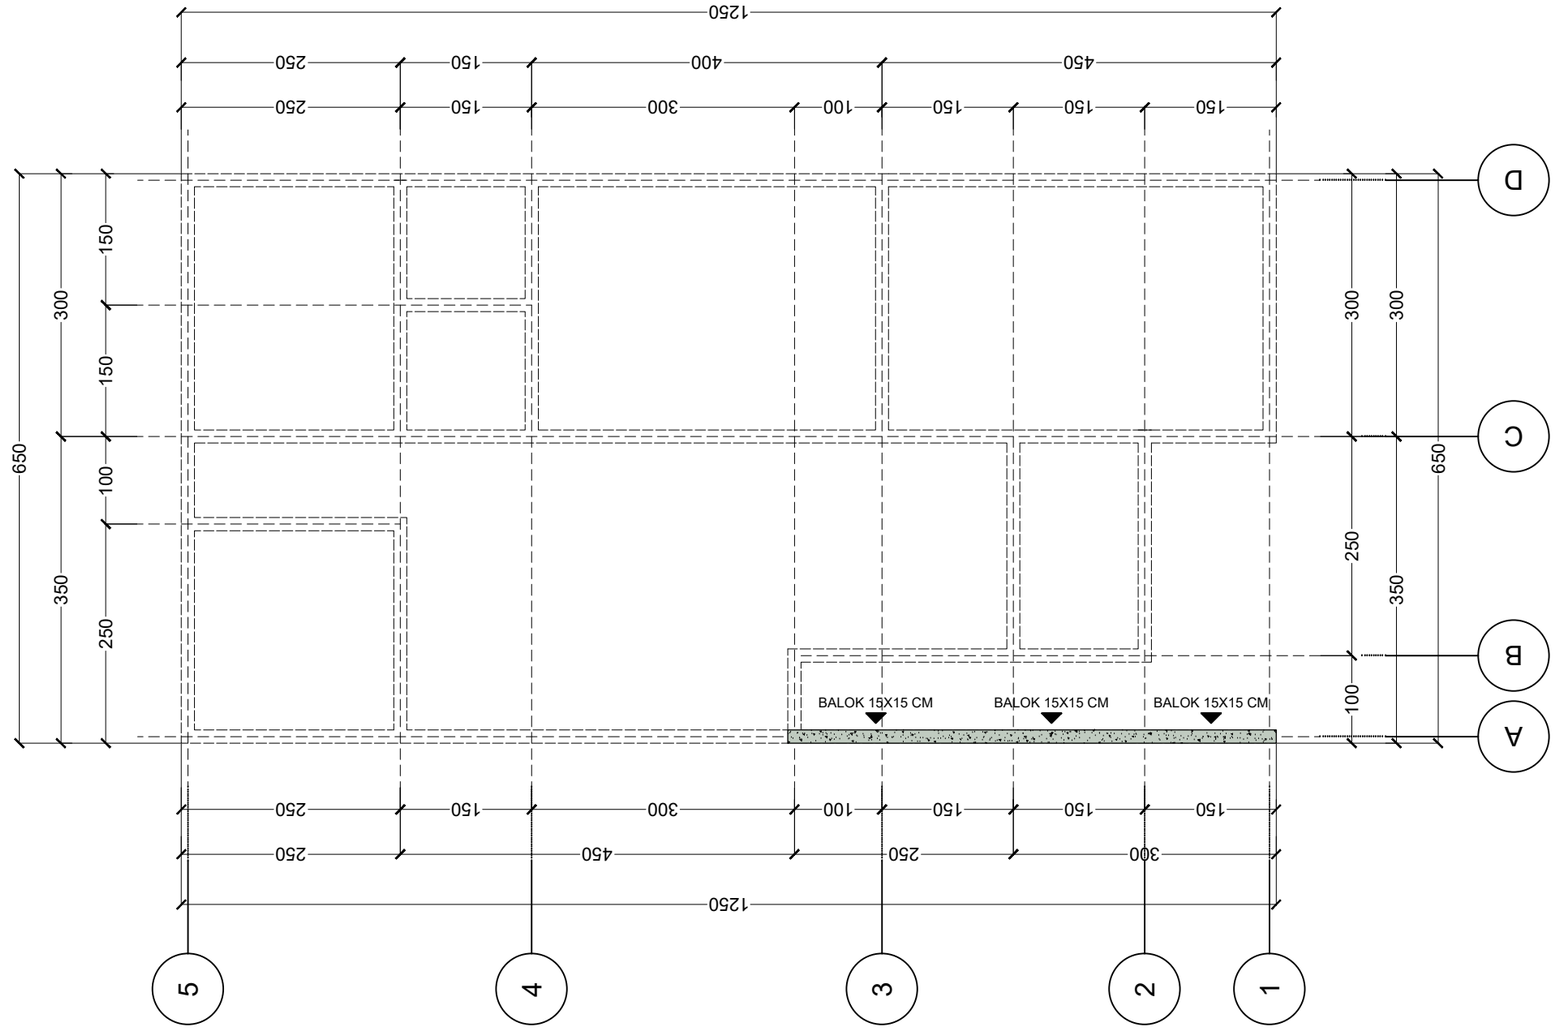

CODE
STR

DENAH BALOK ELEV +2.00

SKALA 1 : 70

GEOMETRI KOLOM K2	▣	▣
DIMENSI	15 x 15	
TUL. ATAS	2 Ø 12	2 Ø 12
TUL.TENGAH	-	-
TUL. BAWAH	2 Ø 12	2 Ø 12
JARAK BEUGEL	¼ H	½ H
	Ø8 - 10	Ø8 - 15

ARCHILLES STUDIO

KETERANGAN :

PROJECT :

PERENCANAAN RUMAH HUNIAN

LOKASI :

PRAMUKA

OWNER :


.....

PERENCANA :

ARCHILLES TEAM

JUDUL GAMBAR	SKALA

TOTAL HALAMAN	CODE	NO HALAMAN

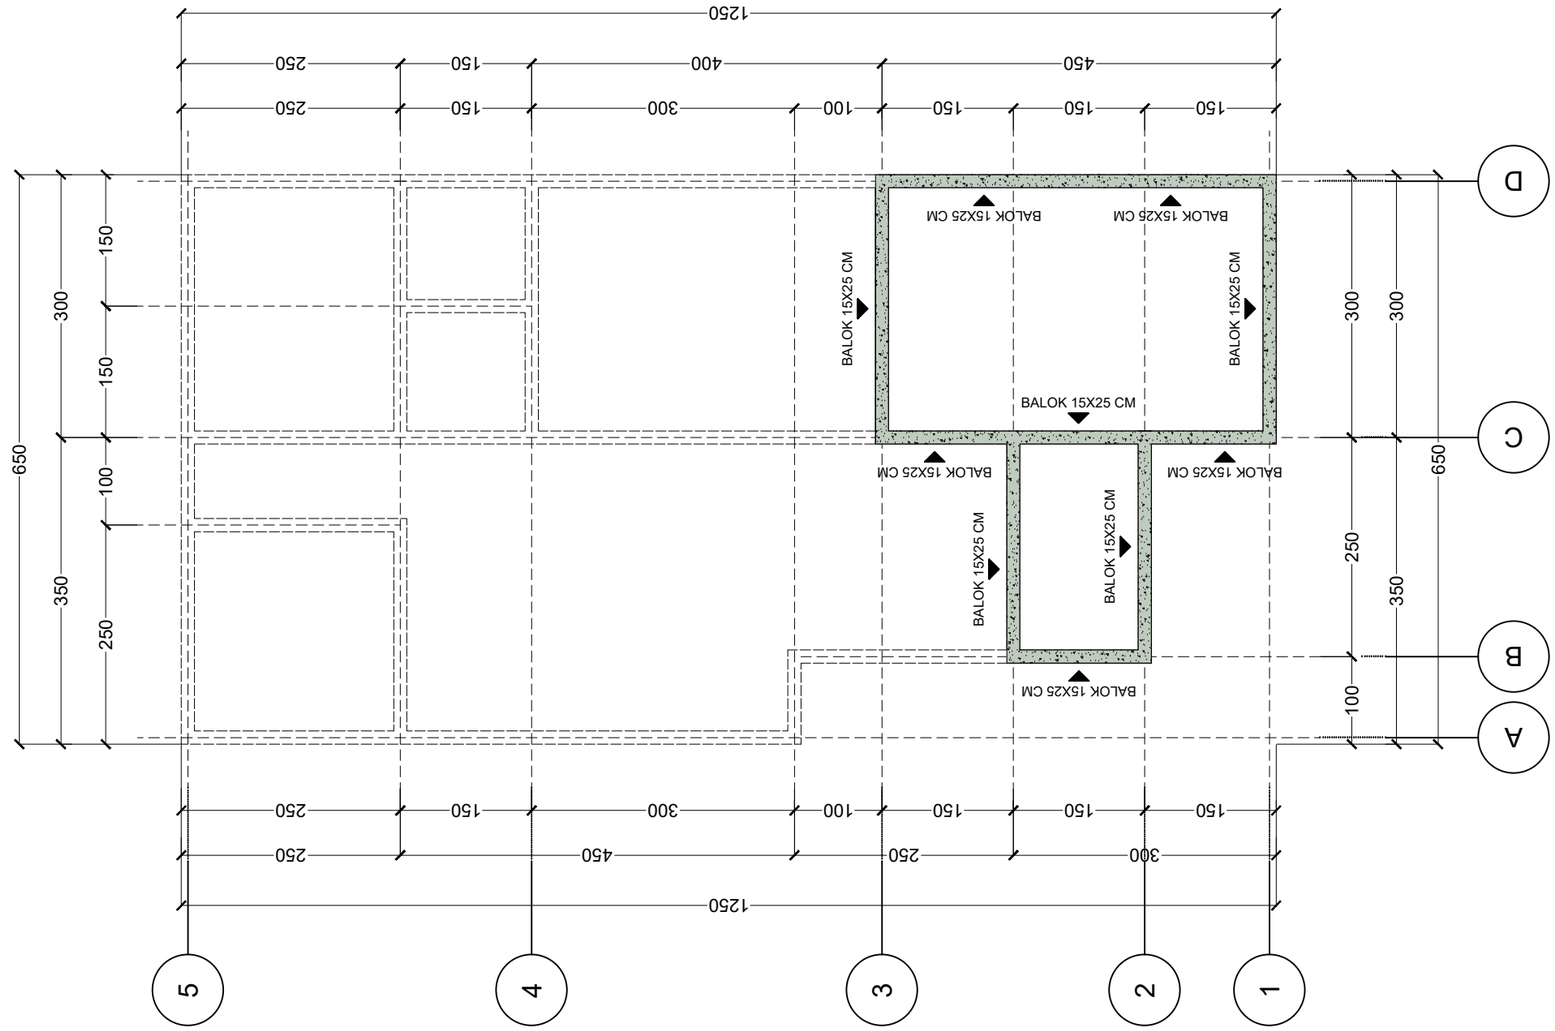

CODE
STR

DENAH BALOK ELEVASI + 3.00

SKALA 1 : 70

GEOMETRI BALOK B1		
DIMENSI	15 x 25	
TUL. ATAS	2 Ø 12	2 Ø 12
TUL.TENGAH	-	-
TUL. BAWAH	2 Ø 12	2 Ø 12
JARAK BEUGEL	¼ H	½ H
	Ø8 - 10	Ø8 - 15

ARCHILLES STUDIO

KETERANGAN :

PROJECT :

PERENCANAAN RUMAH HUNIAN

LOKASI :

PRAMUKA

OWNER :


.....

PERENCANA :

ARCHILLES TEAM

JUDUL GAMBAR	SKALA

TOTAL HALAMAN	CODE	NO HALAMAN

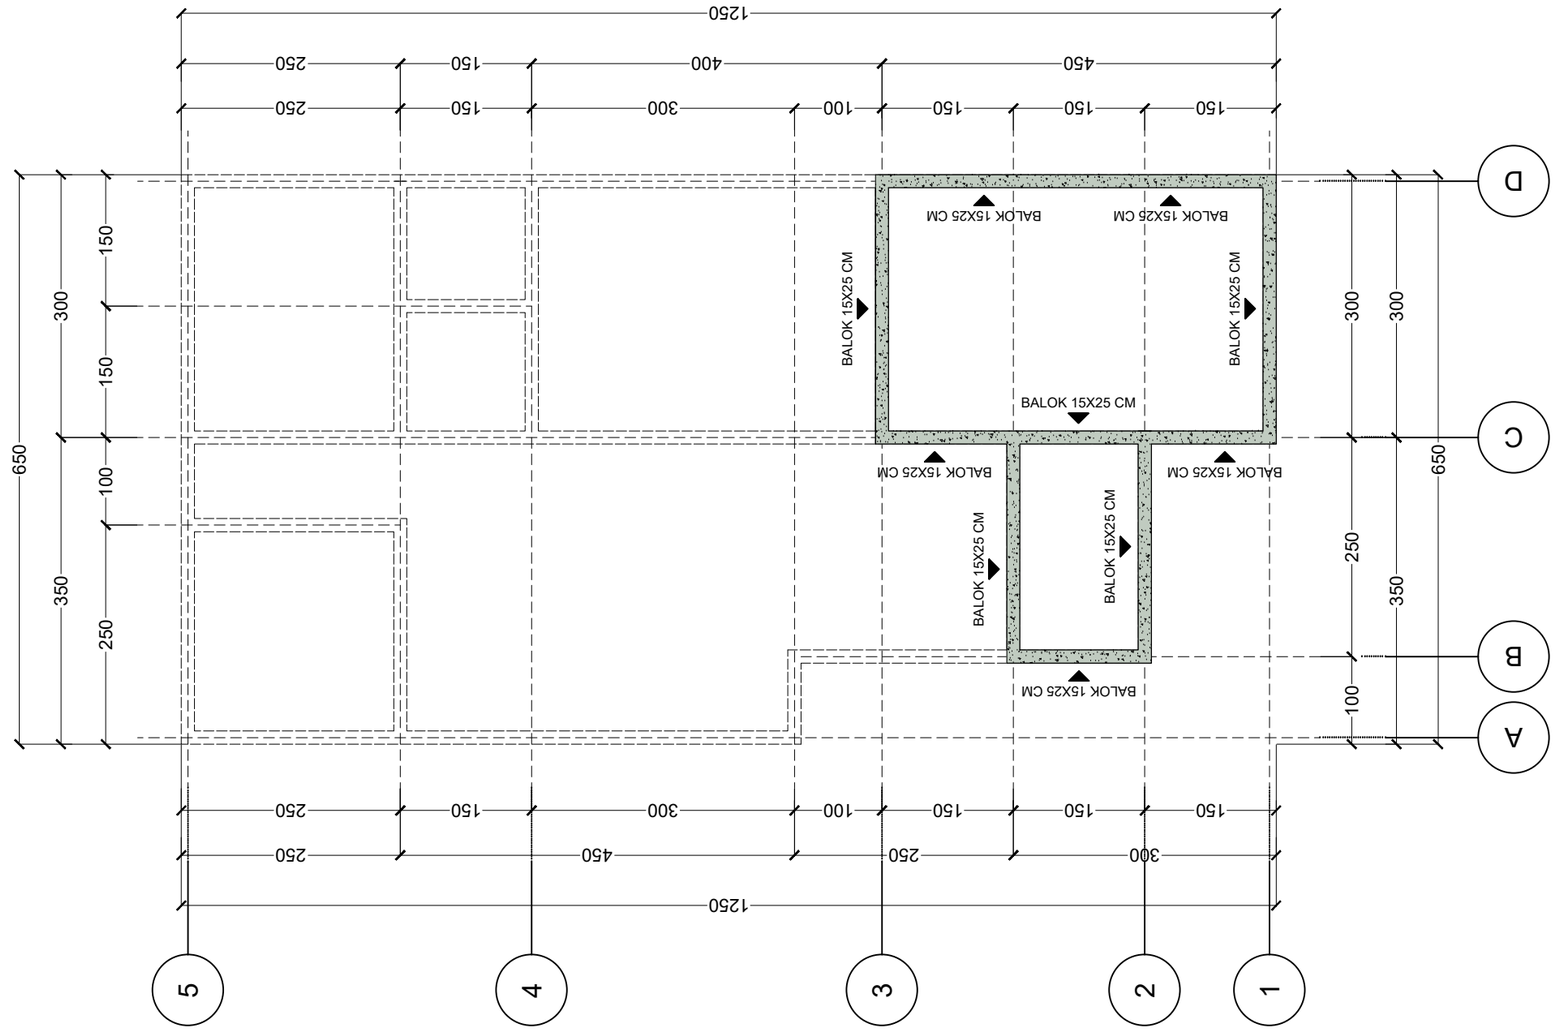

CODE
STR

DENAH BALOK ELEVASI + 3.00

SKALA 1 : 70

GEOMETRI BALOK B1		
DIMENSI	15 x 25	
TUL. ATAS	2 Ø 12	2 Ø 12
TUL.TENGAH	-	-
TUL. BAWAH	2 Ø 12	2 Ø 12
JARAK BEUGEL	¼ H	½ H
	Ø8 - 10	Ø8 - 15

ARCHILLES STUDIO

KETERANGAN :

PROJECT :

PERENCANAAN RUMAH HUNIAN

LOKASI :

PRAMUKA

OWNER :


.....

PERENCANA :

ARCHILLES TEAM

JUDUL GAMBAR	SKALA

TOTAL HALAMAN	CODE	NO HALAMAN

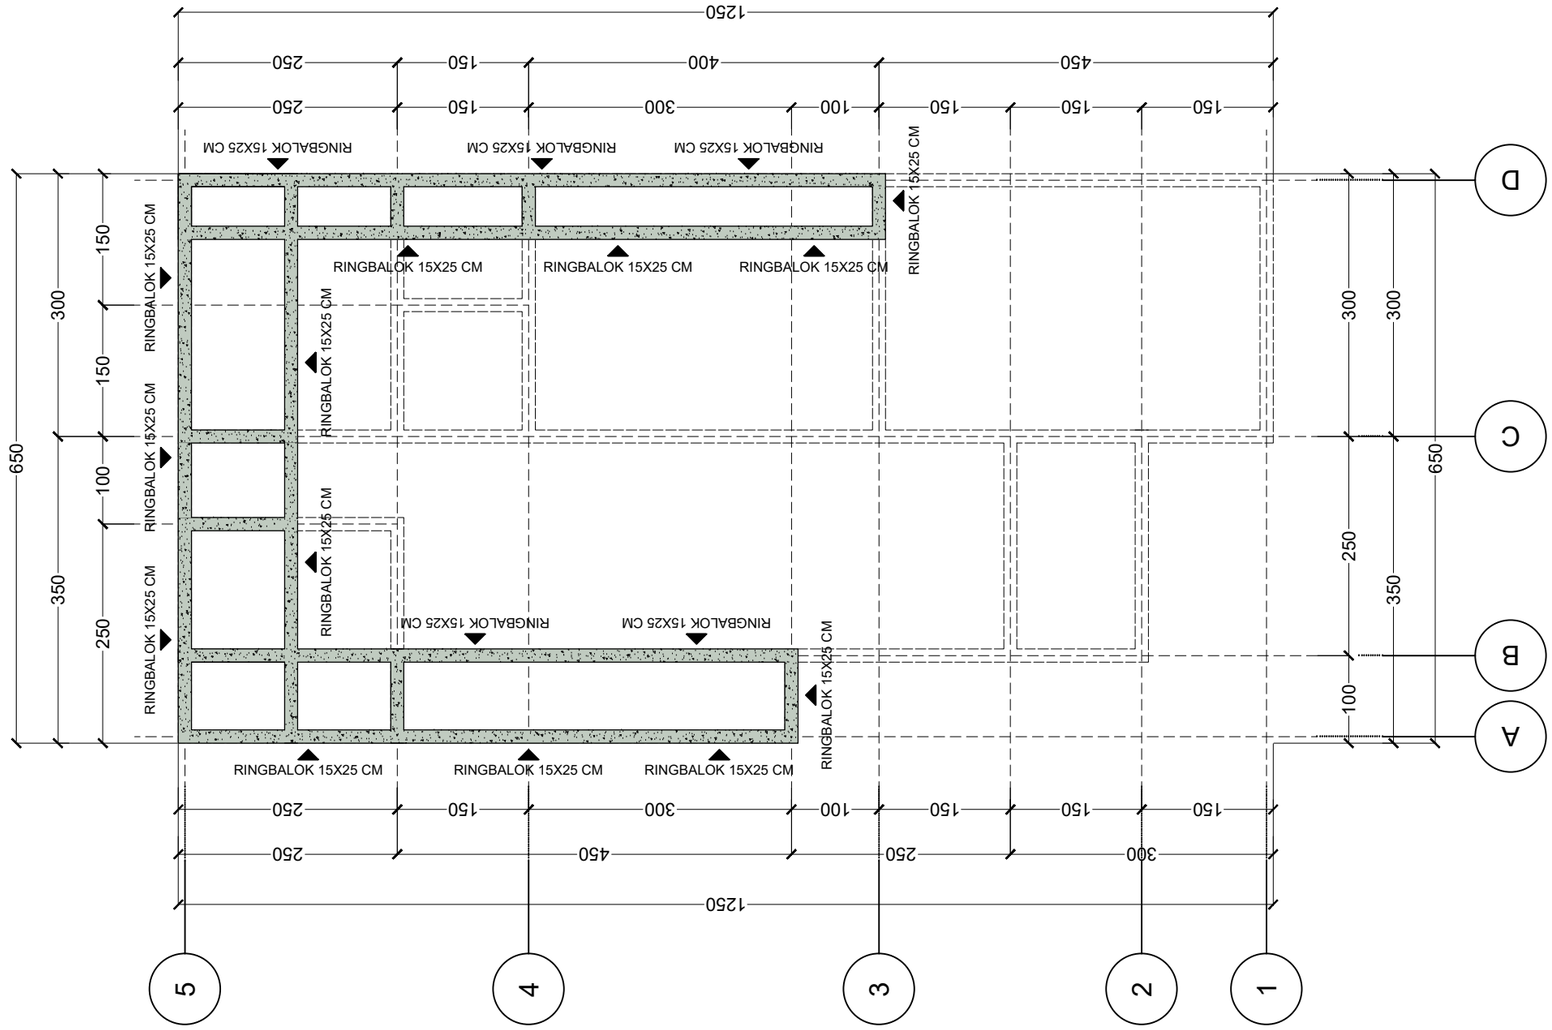

CODE
STR

DENAH BALOK ELEVASI + 3.50

SKALA 1 : 70

GEOMETRI RING BALOK RB1		
DIMENSI	15 x 25	
TUL. ATAS	2 Ø 12	2 Ø 12
TUL.TENGAH	-	-
TUL. BAWAH	2 Ø 12	2 Ø 12
JARAK BEUGEL	¼ H	½ H
	Ø8 - 10	Ø8 - 20

ARCHILLES STUDIO

KETERANGAN :

PROJECT :

PERENCANAAN RUMAH HUNIAN

LOKASI :

PRAMUKA

OWNER :


.....

PERENCANA :

ARCHILLES TEAM

JUDUL GAMBAR	SKALA

TOTAL HALAMAN	CODE	NO HALAMAN

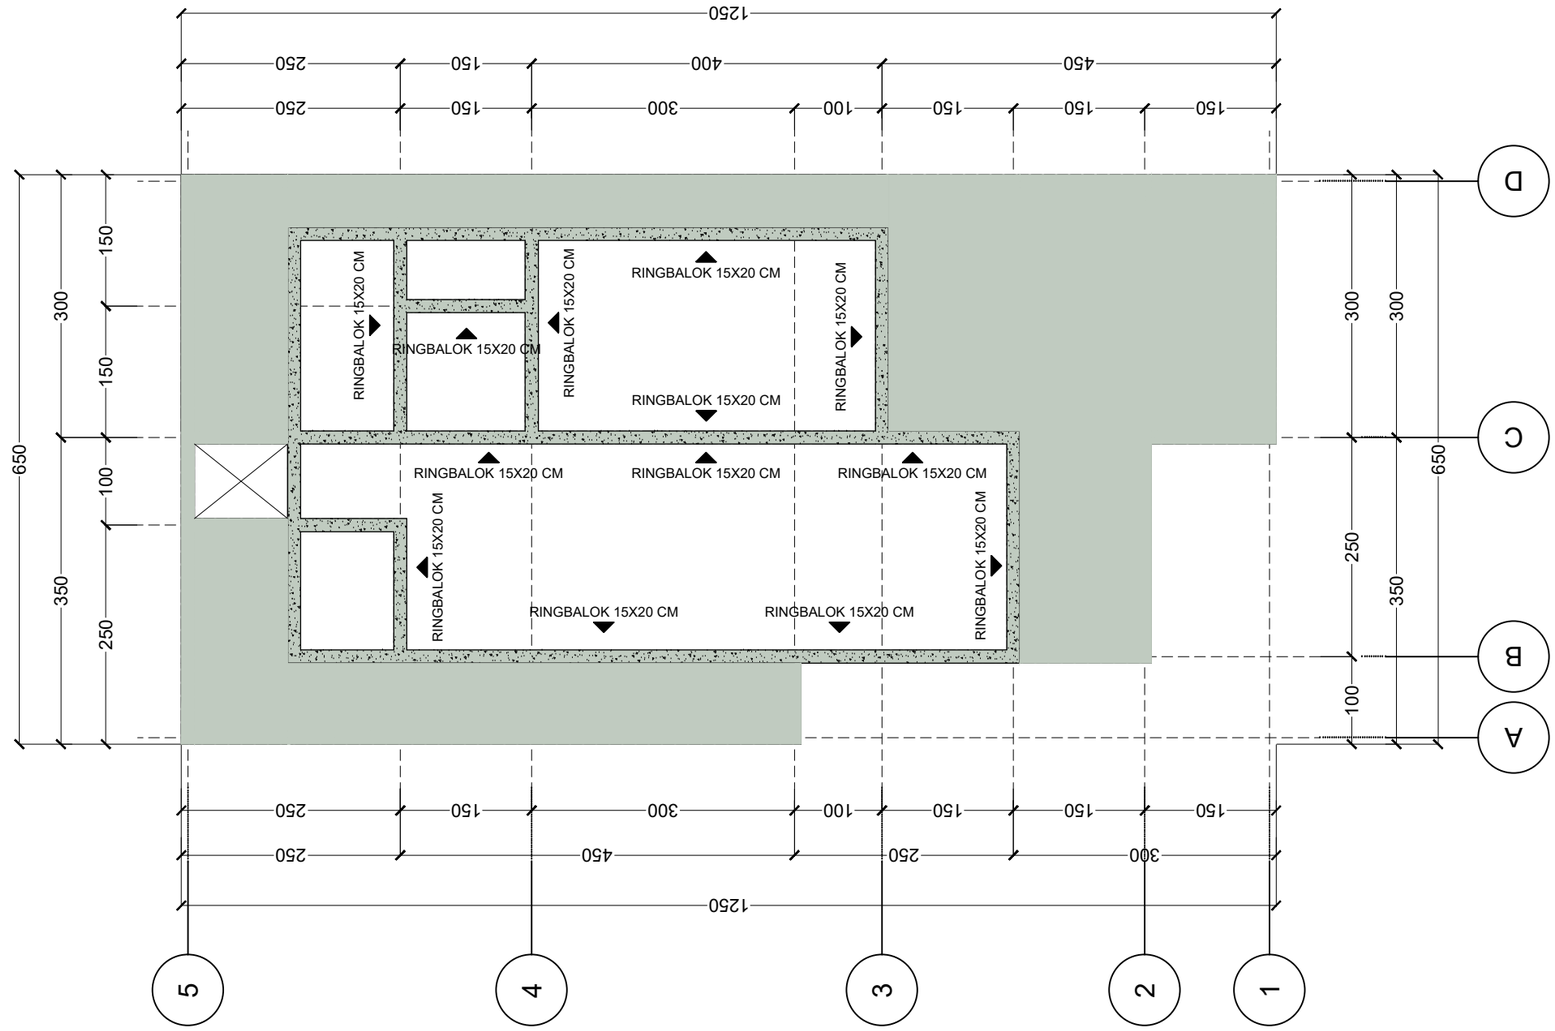

CODE
STR

DENAH BALOK ELEVASI + 3.80

SKALA 1 : 70

GEOMETRI RING BALOK RB2		
DIMENSI	15 x 20	
TUL. ATAS	2 Ø 12	2 Ø 12
TUL.TENGAH	-	-
TUL. BAWAH	2 Ø 12	2 Ø 12
JARAK BEUGEL	¼ H	½ H
	Ø8 - 10	Ø8 - 20

ARCHILLES STUDIO

KETERANGAN :

PROJECT :

PERENCANAAN RUMAH HUNIAN

LOKASI :

PRAMUKA

OWNER :


.....

PERENCANA :

ARCHILLES TEAM

JUDUL GAMBAR	SKALA

TOTAL HALAMAN	CODE	NO HALAMAN

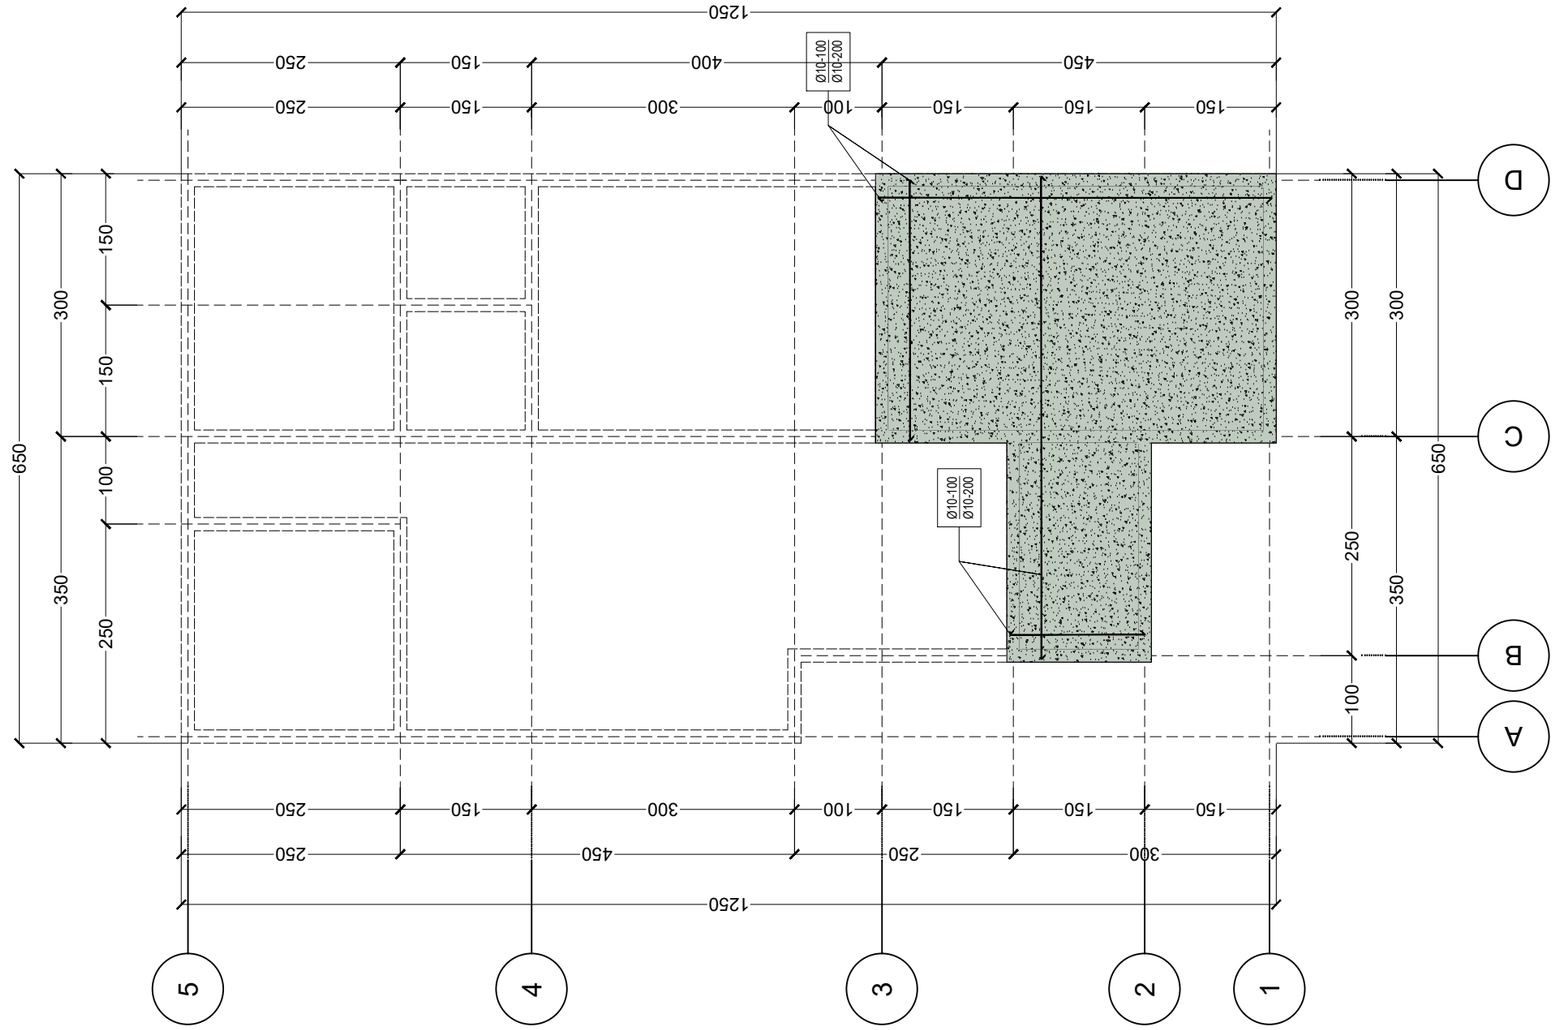

CODE
STR

DENAH DAK BETON ELEVASI +3.00

SKALA 1 : 70

ARCHILLES STUDIO

KETERANGAN :

PROJECT :

PERENCANAAN RUMAH HUNIAN

LOKASI :

PRAMUKA

OWNER :


.....

PERENCANA :

ARCHILLES TEAM

JUDUL GAMBAR	SKALA

TOTAL HALAMAN	CODE	NO HALAMAN

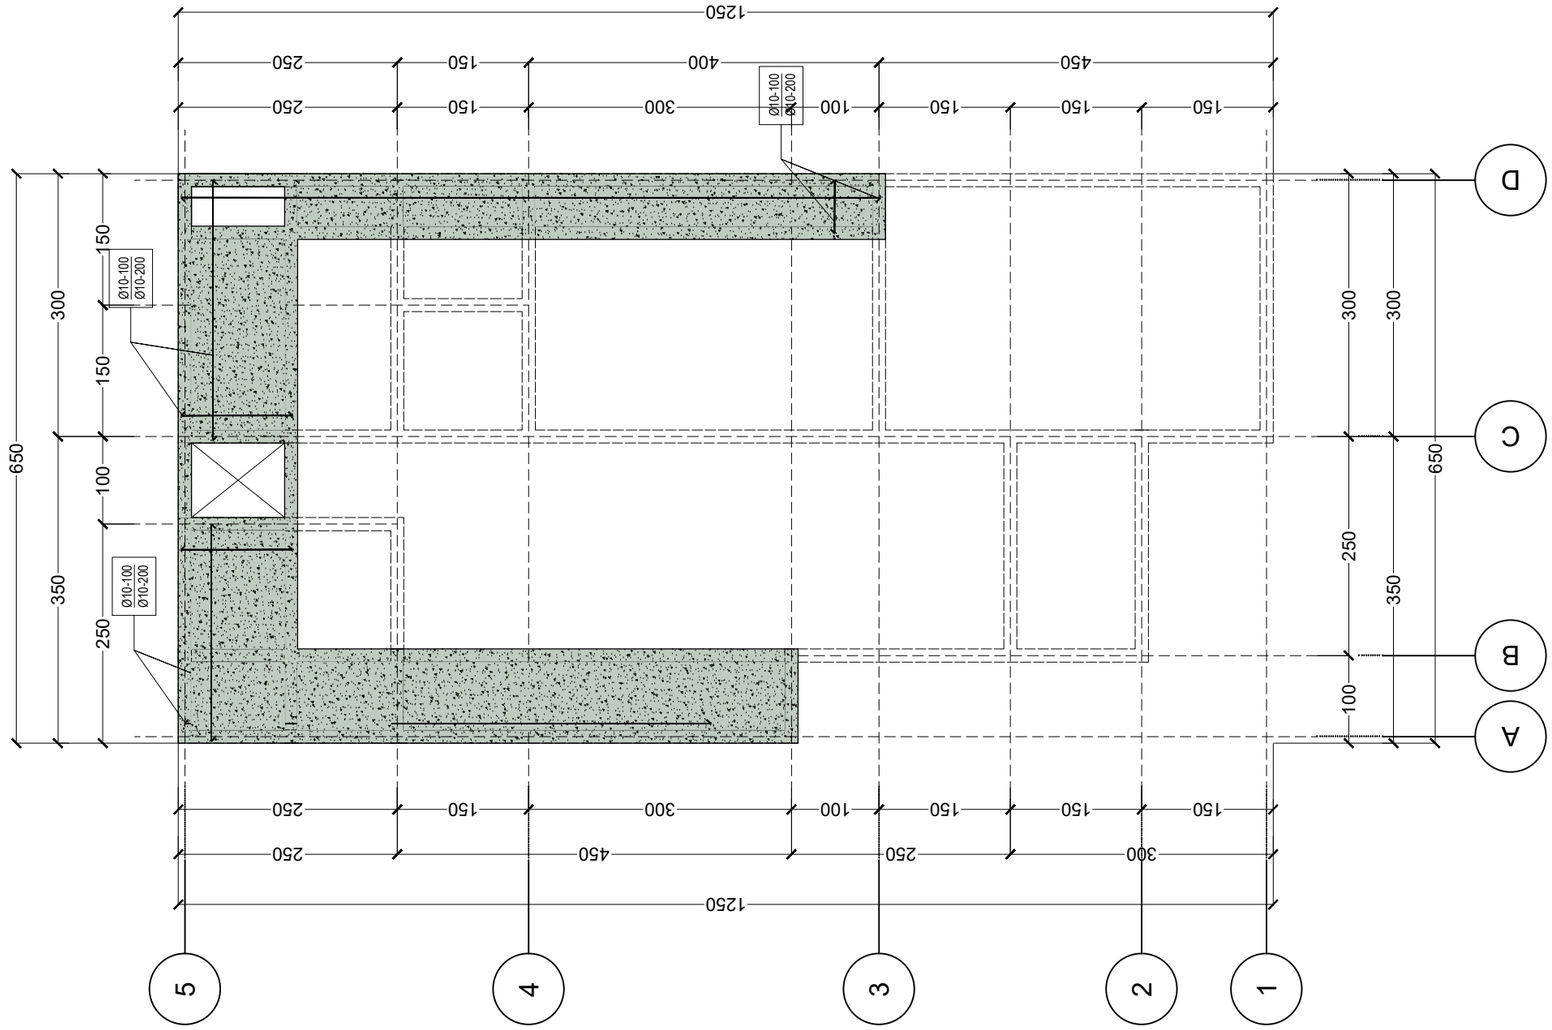

CODE
STR

DENAH DAK BETON ELEVASI +3.50

SKALA 1 : 70

ARCHILLES STUDIO

KETERANGAN :

PROJECT :

PERENCANAAN RUMAH HUNIAN

LOKASI :

PRAMUKA

OWNER :


.....

PERENCANA :

ARCHILLES TEAM

JUDUL GAMBAR	SKALA

TOTAL HALAMAN	CODE	NO HALAMAN

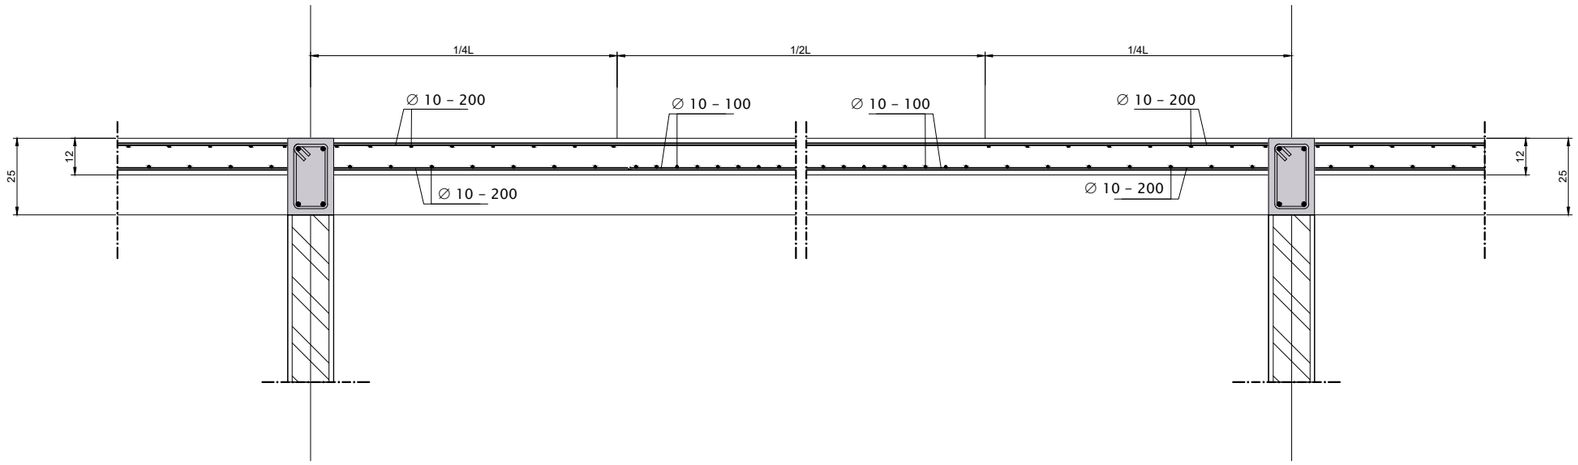

CODE
STR

DETAIL POTONGAN DAK

SKALA 1 : 20

ARCHILLES STUDIO

KETERANGAN :

PROJECT :

PERENCANAAN RUMAH HUNIAN

LOKASI :

PRAMUKA

OWNER :

.....

PERENCANA :

ARCHILLES TEAM


JUDUL GAMBAR	SKALA

TOTAL HALAMAN	CODE	NO HALAMAN

ARCHILLES
STUDIO

MECHANICAL, ELECTRICAL, AND PLUMBING

CODE :
MEP

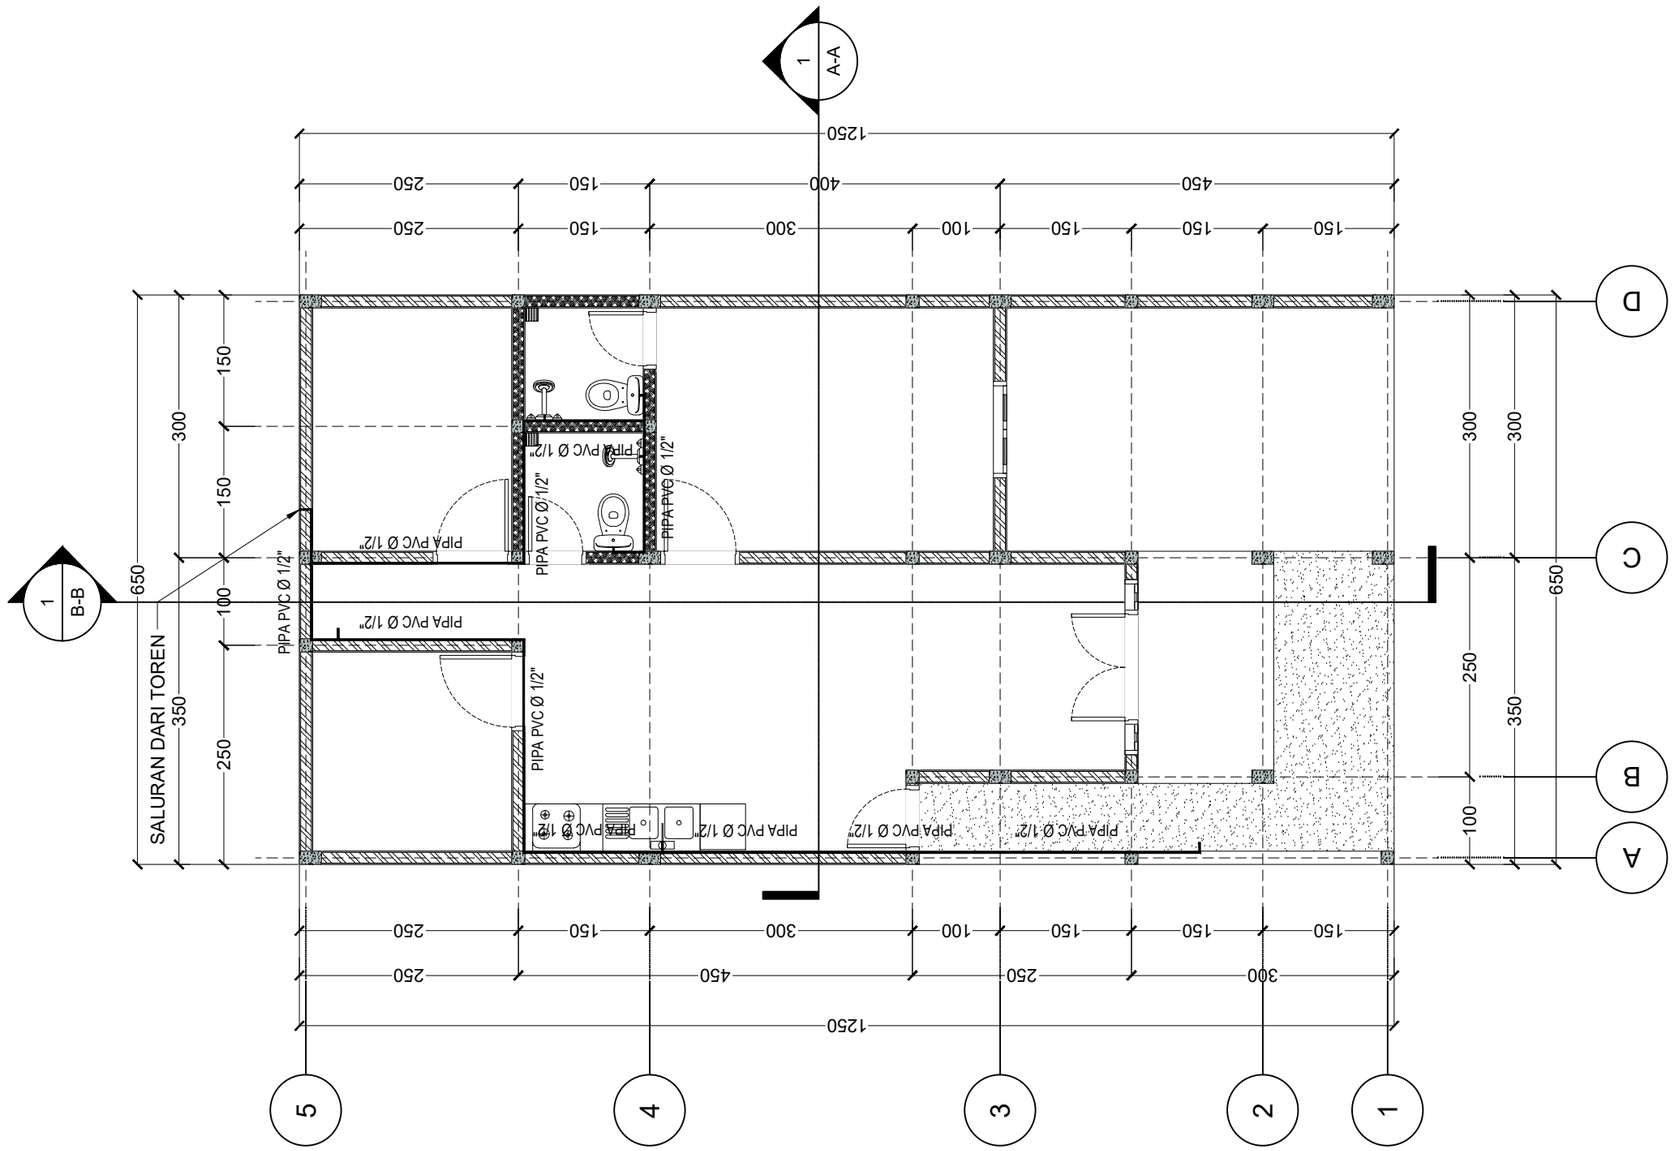

CODE
MEP

DENAH SANITASI AIR BERSIH

SKALA 1 : 70

ARCHILLES STUDIO

KETERANGAN :

PROJECT :

PERENCANAAN RUMAH HUNIAN

LOKASI :

PRAMUKA

OWNER :


.....

PERENCANA :

ARCHILLES TEAM

JUDUL GAMBAR	SKALA

TOTAL HALAMAN	CODE	NO HALAMAN

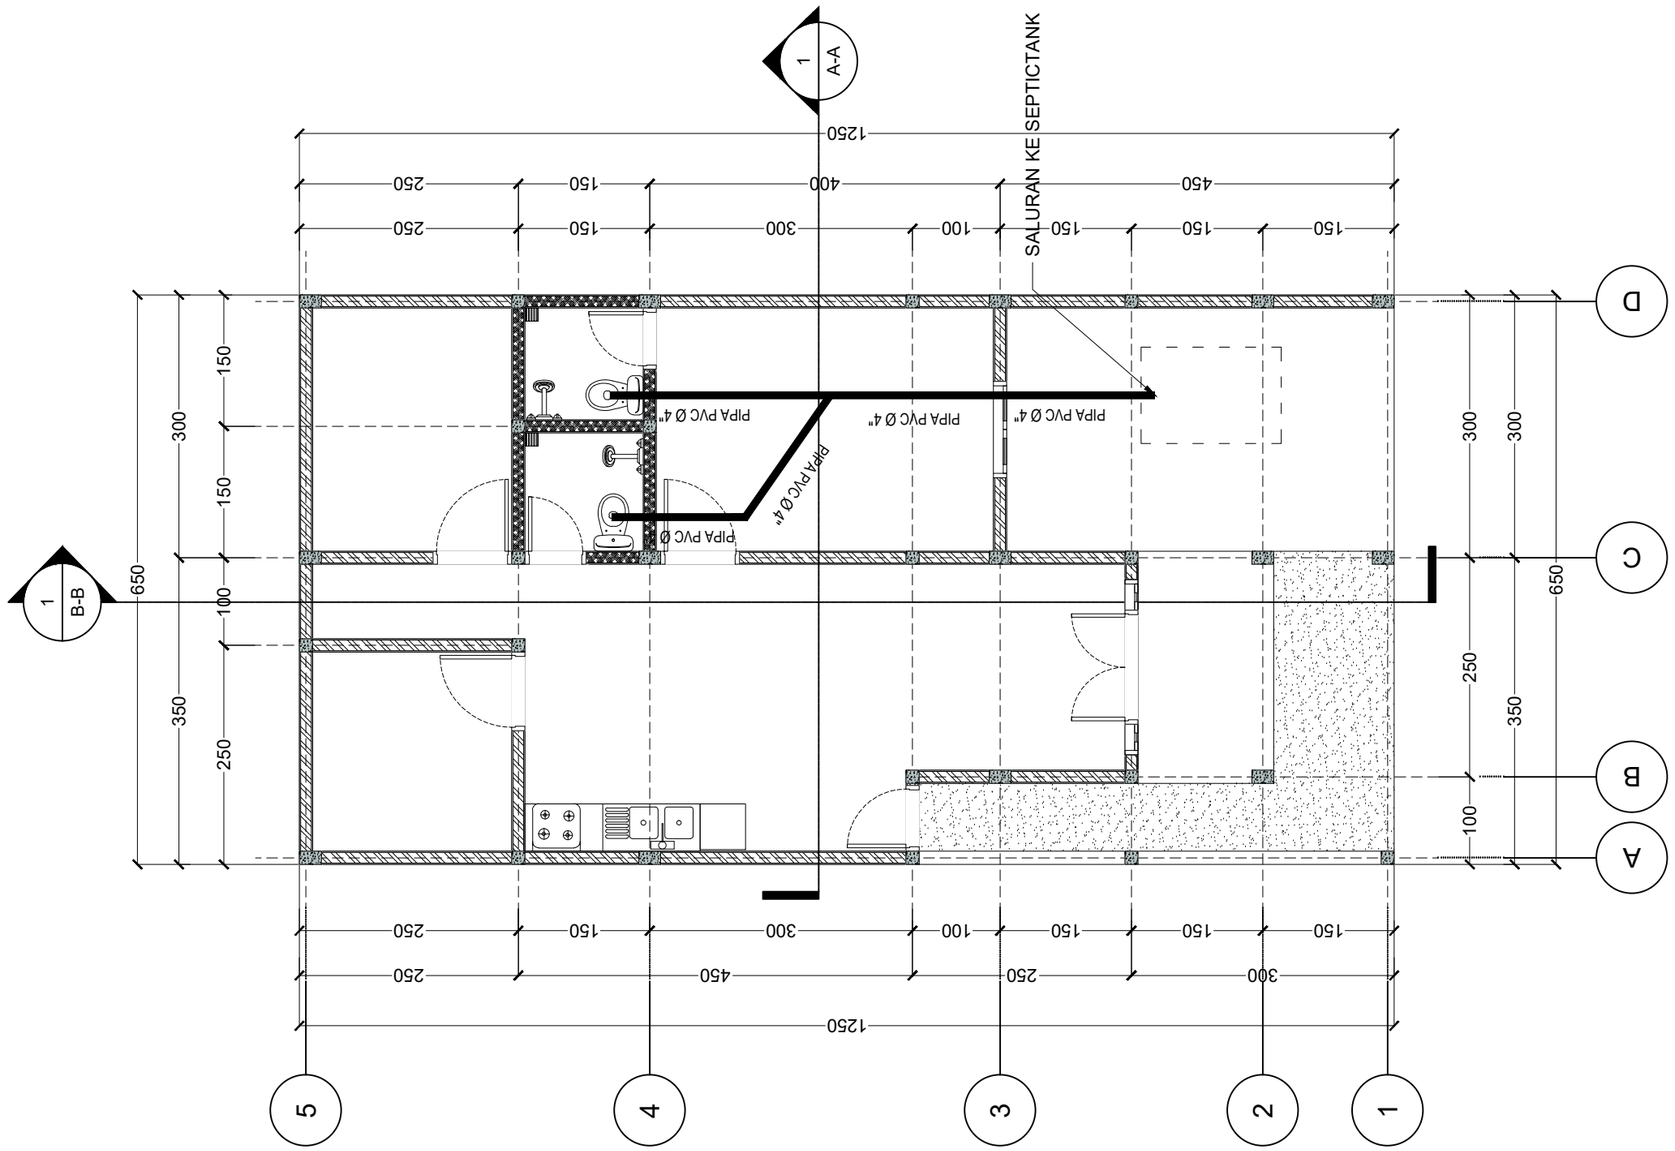

CODE
MEP

DENAH SANITASI PEMBUANGAN TINJA

SKALA 1 : 70

ARCHILLES STUDIO

KETERANGAN :

PROJECT :

PERENCANAAN RUMAH HUNIAN

LOKASI :

PRAMUKA

OWNER :


.....

PERENCANA :

ARCHILLES TEAM

JUDUL GAMBAR	SKALA

TOTAL HALAMAN	CODE	NO HALAMAN

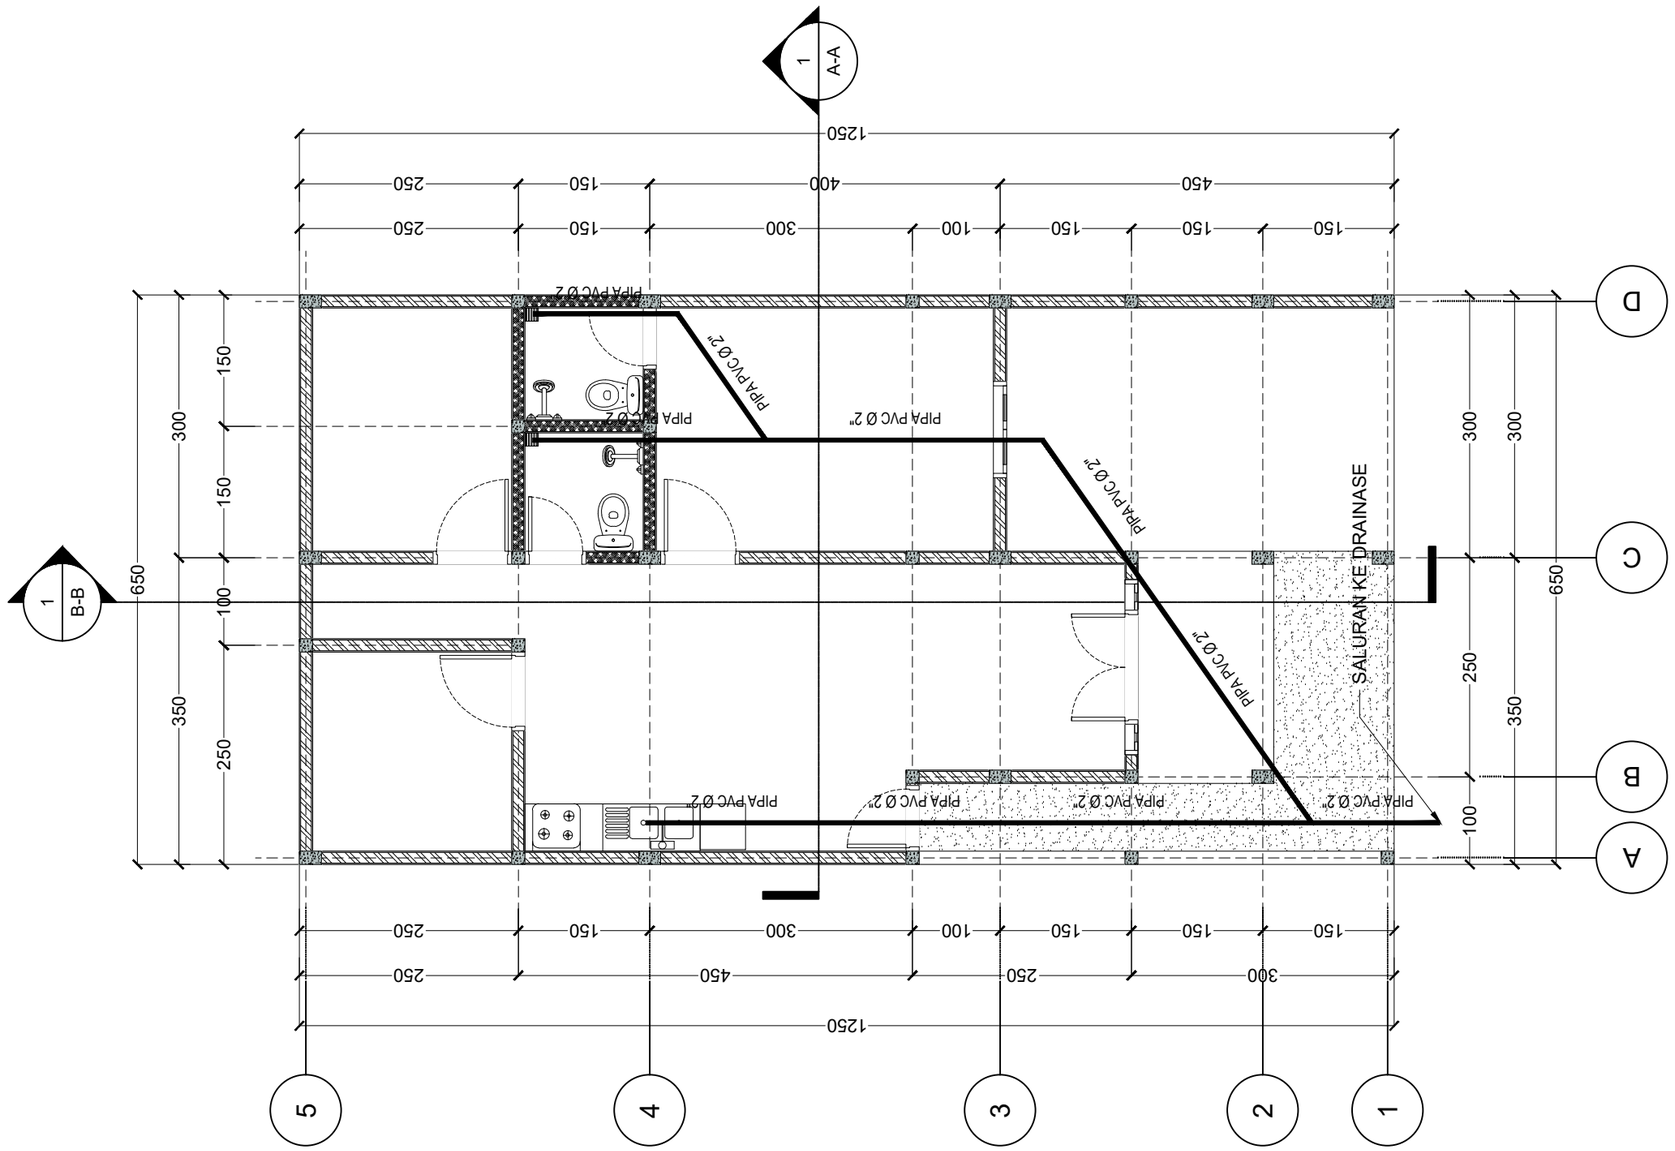

CODE
MEP

DENAH SANITASI AIR KOTOR

SKALA 1 : 70

ARCHILLES STUDIO

KETERANGAN :

PROJECT :

PERENCANAAN RUMAH HUNIAN

LOKASI :

PRAMUKA

OWNER :


.....

PERENCANA :

ARCHILLES TEAM


JUDUL GAMBAR	SKALA

TOTAL HALAMAN	CODE	NO HALAMAN

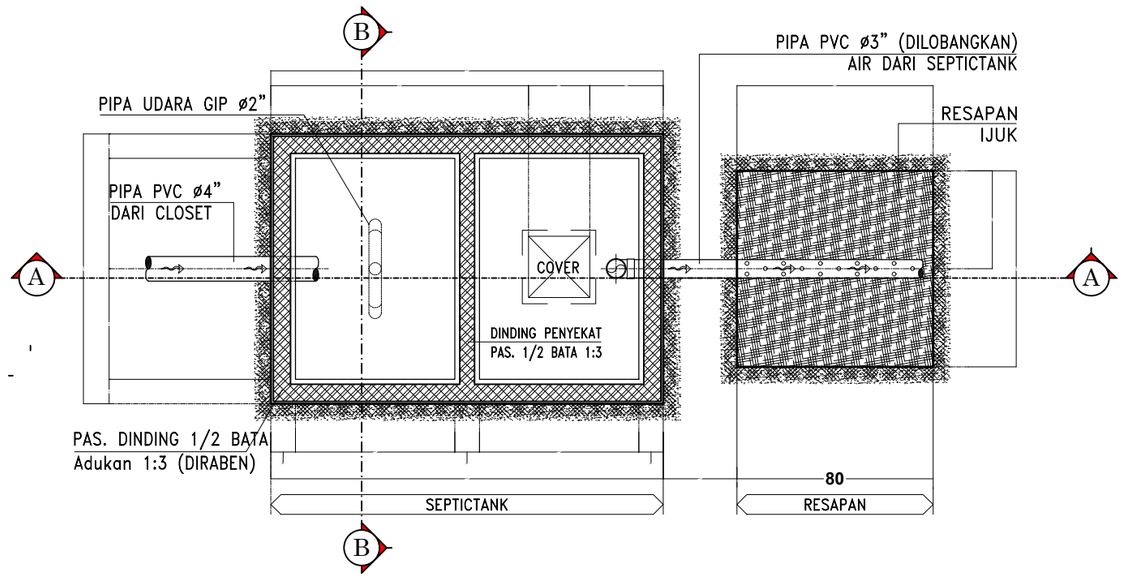


3 MEP — DENAH SEPTIC TANK

SKALA 1 : 25 I LB 300 M2

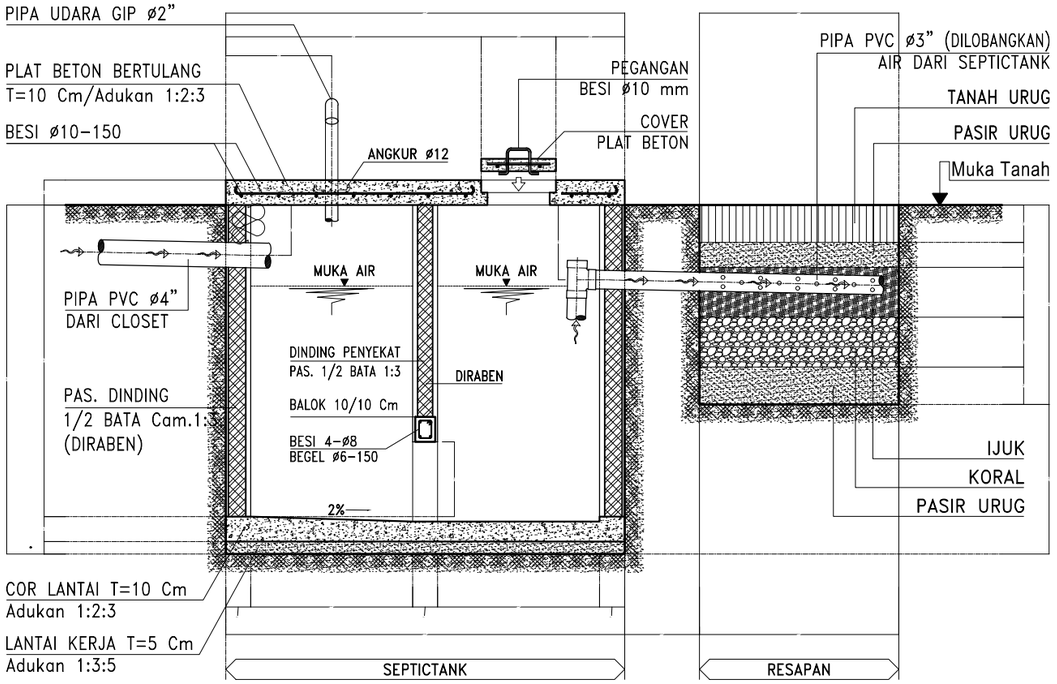

3 MEP — POTONGAN A-A

SKALA 1 : 25 I LB 300 M2

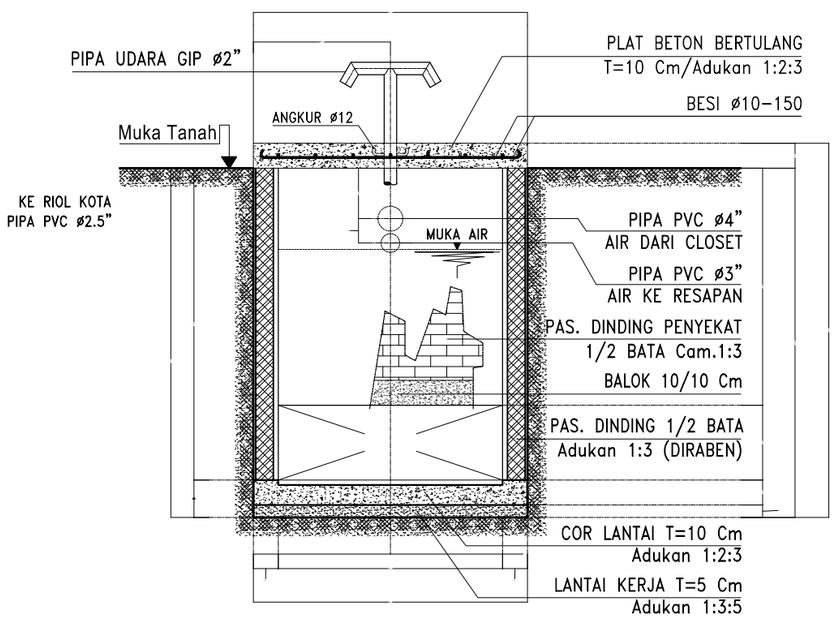

3 MEP — POTONGAN B-B

SKALA 1 : 25 I LB 300 M2

ARCHILLES STUDIO

KETERANGAN :

PROJECT :

PERENCANAAN RUMAH HUNIAN

LOKASI :

PRAMUKA

OWNER :


.....

PERENCANA :

ARCHILLES TEAM

JUDUL GAMBAR	SKALA

TOTAL HALAMAN	CODE	NO HALAMAN

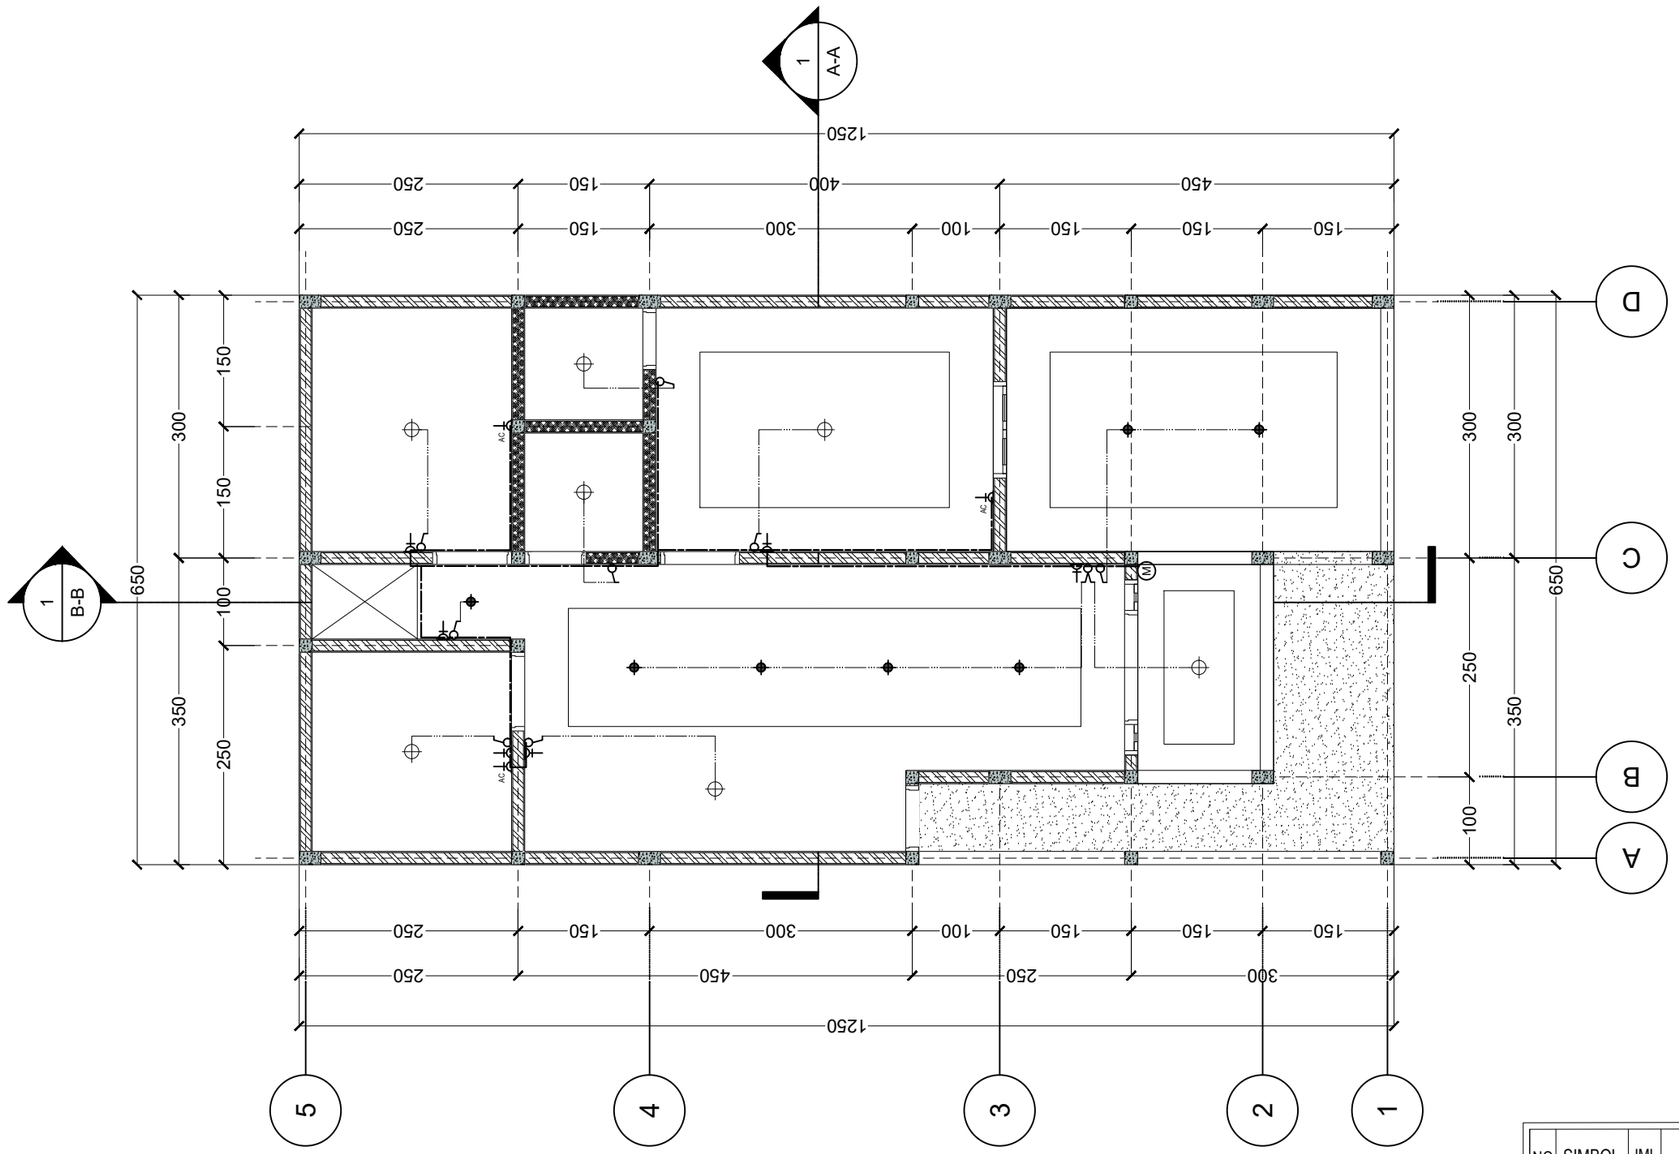

NO	SIMBOL	JML	KETERANGAN
1		7	LAMPU 40 WATT
2		8	SAKLAR TUNGGAL ELEV + 1.50
3		1	SAKLAR DOUBLE ELEV + 1.50
4		6	STOP KONTAK ELEV + 1.50
5	AC	3	STOP KONTAK AC ELEV + 2.80
5	M	1	METERAN LISTRIK DAN MCB
6		7	LAMPU DOWN LIGHT

ARCHILLES STUDIO

KETERANGAN :

PROJECT :

PERENCANAAN RUMAH HUNIAN

LOKASI :

PRAMUKA

OWNER :

.....

PERENCANA :

ARCHILLES TEAM

JUDUL GAMBAR	SKALA

TOTAL HALAMAN	CODE	NO HALAMAN

ARCHILLES
STUDIO

Instagram : archilles_studio